Secteur Lebon-Lamartine
MAITRISE D'OEUVRE URBAINE

Permis d'aménager

Notice sécurité incendie

LEGENDE

REMARQUES

MAÎTRISE D'OUVRAGE :

EPT GOSB
11 Avenue Henri Farman
BP 748
94398 Orly Aérogare Cedex

MAÎTRISE D'OEUVRE :

Marniquet Aubouin
21 rue Pixérécourt - 75020 Paris
tel : 01 48 05 53 25 - fax : 01 48 05 55 14
@ : atelier@marniquetaubouin.com

SAS TRANS-FAIRE
3 PASSAGE BOUTET - 94110 ARCUEIL
Tel : 01 45 36 15 00
contact@trans-faire.net
www.trans-faire.net

TPFI
Bâtiment B 3 rue de la Renaissance
92160 ANTONY
Tel : 01 55 52 10 09
paris@tpfi.fr

Echelle : 1/500

Date: **Janvier 2025**

Planche N°
Indice : PA-

Sommaire

Introduction 3

1. Contexte du projet 4

Desserte incendie existante 8

2. Conserver le fonctionnement du quartier 12

Plan de superposition existant – projet 12
Une future accessibilité pompier inchangée 14
Fonctionnement à terme 16
Détails bâtiments existants conservés 18
Détails desserte ilots constructibles 20
Vision globale 22
Les modes d'habiter 24

Introduction

La présente notice porte sur le projet de renouvellement urbain du quartier Lamartine, qui comprend :

- La réhabilitation et la résidentialisation des 4 tours (300 logements sociaux) ;
- La démolition des 3 barres (263 logements sociaux) et le relogement des locataires, ainsi que la démolition des boxes de stationnement et de la chaufferie ;
- La construction d'environ 460 nouveaux logements diversifiés (logements sociaux, accession à prix maitrisés, accession libre, locatif libre), portant l'ensemble du quartier à terme à environ 760 logements ;
- La requalification de l'ensemble des espaces extérieurs (création d'espaces verts et désimperméabilisés, rendus libres grâce aux parkings souterrains, plantation d'arbres, reprise de la Rue Lamartine pour la rendre apaisée et sécurisée pour les piétons et vélos, requalification de la coulée verte avec un parvis entre les deux écoles) ;
- L'extension-réhabilitation de la crèche ;
- La création d'une cour EVEIL végétalisée et aux usages diversifiés dans l'école Lebon ;
- La création de locaux dédiés à des activités d'économie sociale en rez-de-chaussée des tours ;
- La construction d'un tiers-lieu dédié à la jeunesse, abritant également la Maison des projets (opération déjà livrée).

Le présent dossier porte uniquement sur la défense incendie des bâtiments conservés et des bâtiments envisagés pour lesquels des dossiers de PC seront déposés ultérieurement.

1. Contexte du projet

Localisation

Le site de projet est situé au Sud de la commune de Villejuif, limitrophe par la coulée verte avec l'Haÿ-les-Roses.
Un tissu largement hétérogène occupe le site et ses abords, où des tours et des barres (R+13) côtoient des maisons de ville (R+1).

Desserte

Le site est bien desservi en transport en commun :

- par la proximité de la ligne de métro 7 (Villejuif – Louis Aragon)
- par une station de tramway T7 (Lamartine), au pied du site
- par de nombreux arrêts de bus localisés sur la Départementale 7 (N22 + 286 sur la rue Sainte-Colombe)

Ce quartier est aujourd'hui connecté au reste de la ville par la Rue Lamartine, une unique rue qui connecte la Départementale à la rue Sainte-Colombe.

Dimension sociale et architecturale

Il porte une dimension sociale forte depuis sa construction. C'est une part importante de son identité, aujourd'hui comme hier, et qui perdurera à travers le projet de renouvellement urbain.

C'est un quartier homogène qui a été conçu selon les principes d'aménagement de l'époque de la reconstruction : des grands collectifs organisés en 4 tours à R+13 et 3 barres à R+9, qui offrent des vues lointaines et des pièces d'eau confortables. Les 'vides' entre les bâtiments sont destinés à accueillir les équipements de proximité et des jardins généreux. Et inévitablement, des nappes de stationnement aux pieds des bâtiments.

Photographie aérienne du site

L’homogénéité du quartier : la limite de sa capacité à évoluer avec le reste de la ville et de la société

Le quartier Lebon Lamartine est un quartier de son époque, avec les avantages et inconvénients qui en sont inhérents. On retrouve les éléments disqualifiants génériques de ces quartiers :

- un quartier mono fonctionnel de logements sociaux, en rupture d’échelle et de forme avec les quartiers voisins
- une ambiguïté sur la propriété foncière entre les espaces publics et les espaces résidentiels du bailleur Valdevy
- une nappe de parking en entrée de quartier qui installe un espace de mise à distance avec l’environnement du quartier, des sols imperméabilisés avec des revêtements en enrobés vieillis et disqualifiants
- un rapport au sol inexistant

Mais c’est aussi un quartier qui bénéficie de qualités importantes sur lesquelles le projet de renouvellement va s’appuyer :

- un patrimoine paysager très présent : les arbres ont été plantés au moment de la construction du quartier. Ils ont pu se développer dans de bonnes conditions, en pleine terre, et sont aujourd’hui à pleine maturité. Les espaces de jardin donnent des vues changeantes depuis les logements, qui sont appréciées des habitants.
- un patrimoine bâti dont la réhabilitation va permettre la permanence et l’amélioration du confort de vie des habitants avec la rénovation thermique, l’adjonction de balcons et le réaménagement des espaces de rez de chaussée pour accueillir des locaux communs, vélo et locaux à destination d’activités en lien avec l’Economie Sociale et Solidaire

Desserte incendie existante

Actuellement, les bâtiments sur le site se composent principalement de barres et de tours avec une hauteur maximale à R+13 au niveau des tours.

- **la défense incendie des tours et des barres est assurée par une voie échelle**
- **la défense incendie de l'école est assurée par une voie échelle**
- **la défense incendie de la crèche est assurée par une voie engin (bloquée par des stationnements illicites)**
- **la défense incendie des box est assurée par des voies engins.**

De plus, **5 bornes incendie**s sont localisées dans le secteur à -50m des colonnes sèches des tours.

L'objectif du projet est de conserver le fonctionnement de défense incendie actuel du secteur pour les bâtiments non-démolis (tours, crèche, école).

Lebon Lamartine – schéma de principe de desserte incendie existante

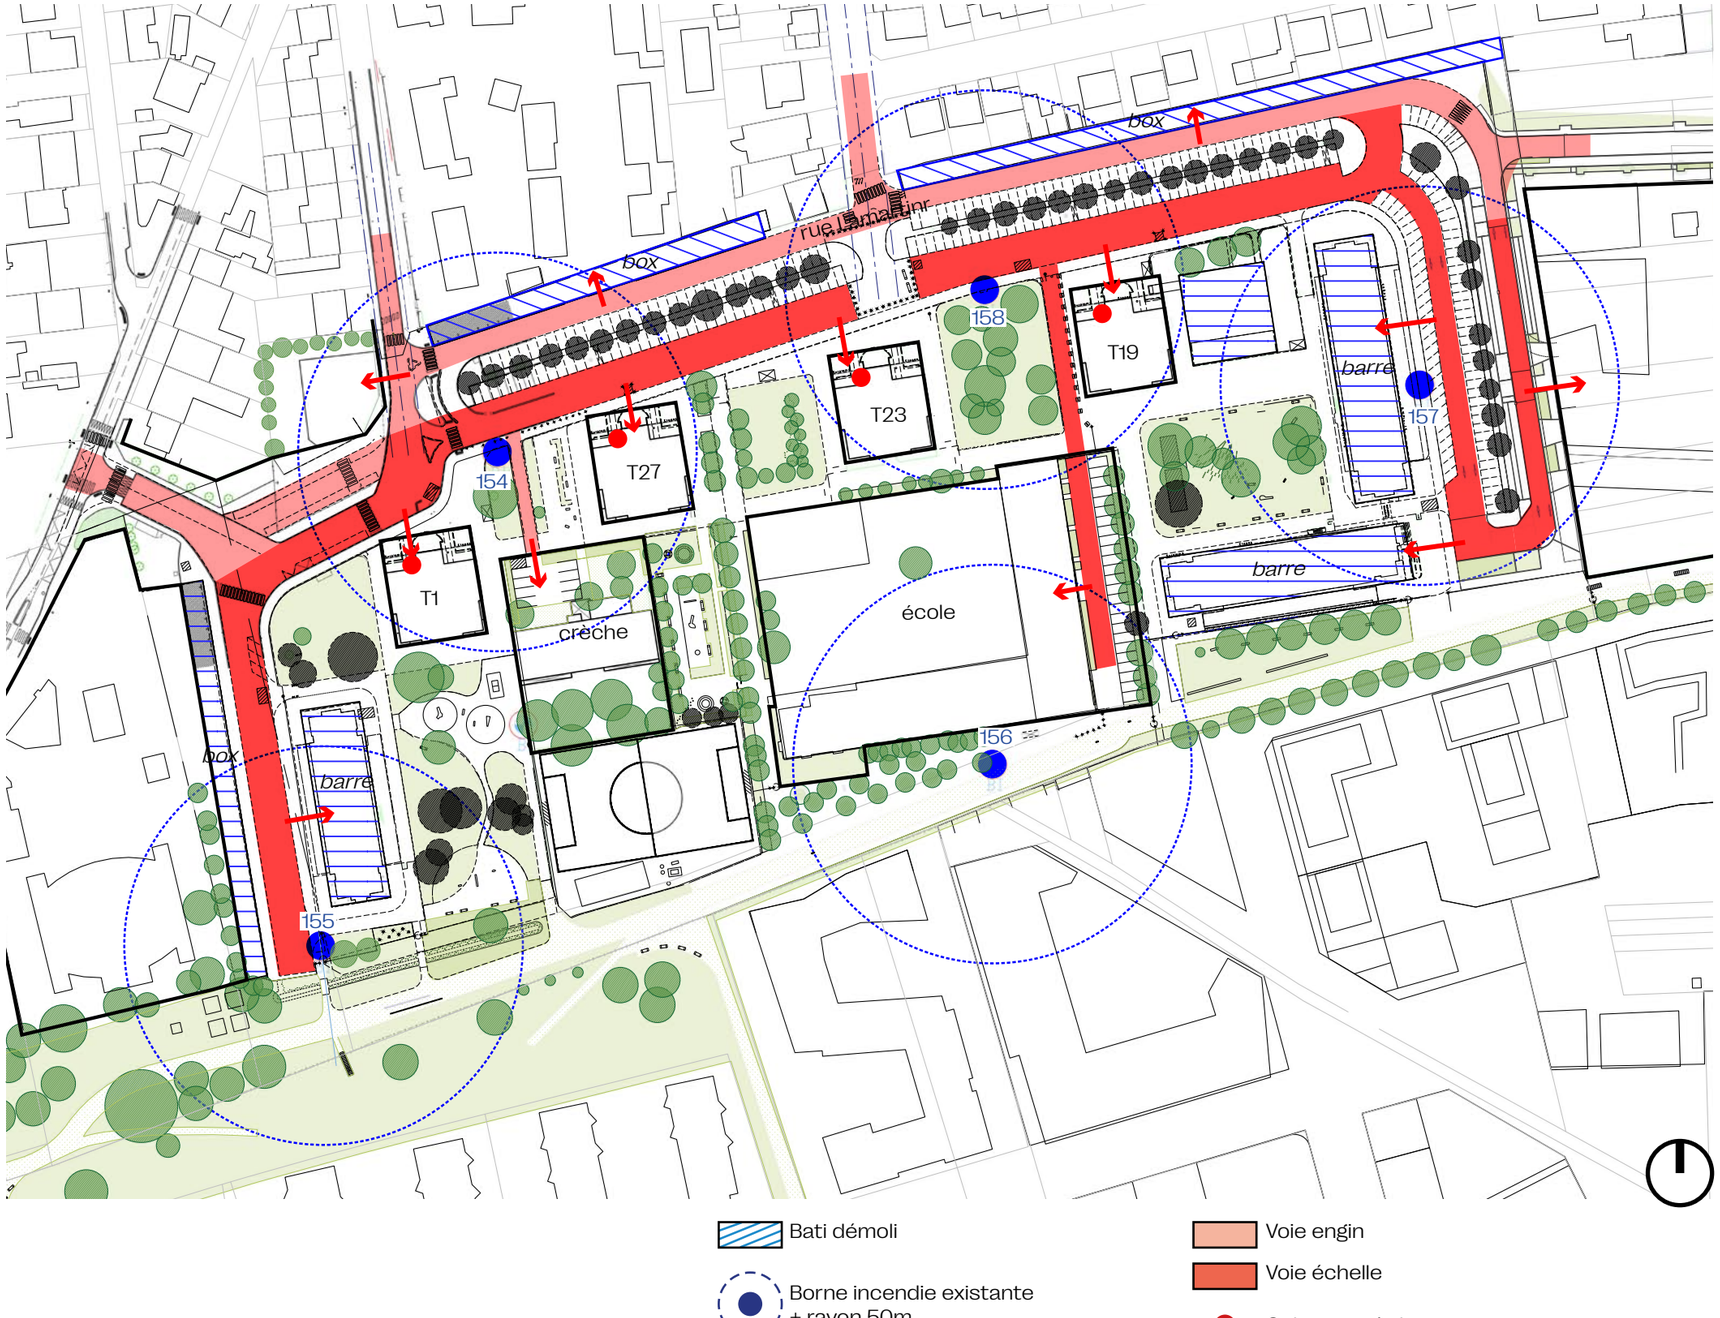

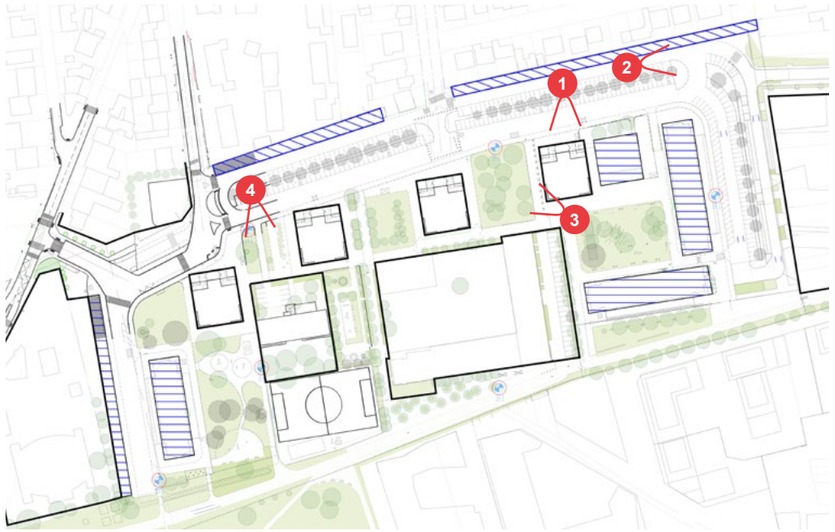

1. Rue Lamartine – vers la tours 19
2. Rue Lamartine – box de stationnement
3. Voie de desserte sécurité incendie école
4. Voie de desserte sécurité incendie crèche

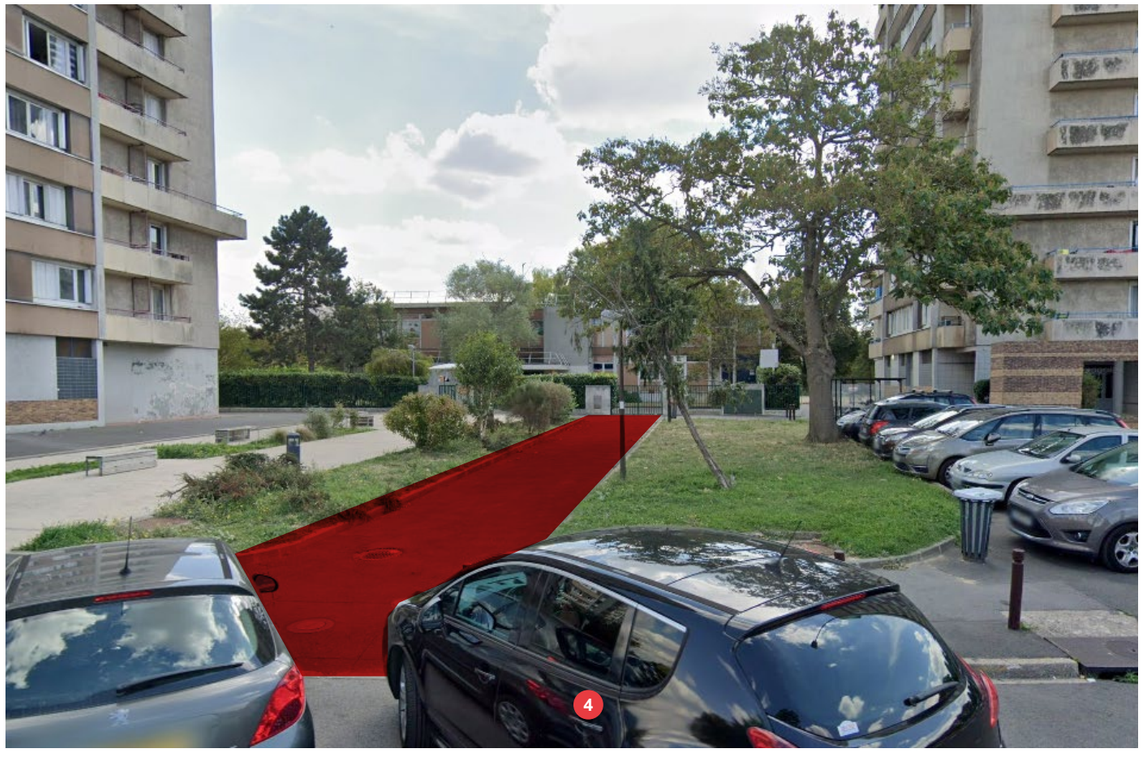

2. Conserver le fonctionnement du quartier

Plan de superposition existant - projet

Lebon Lamartine – plan de superposition existant / projet

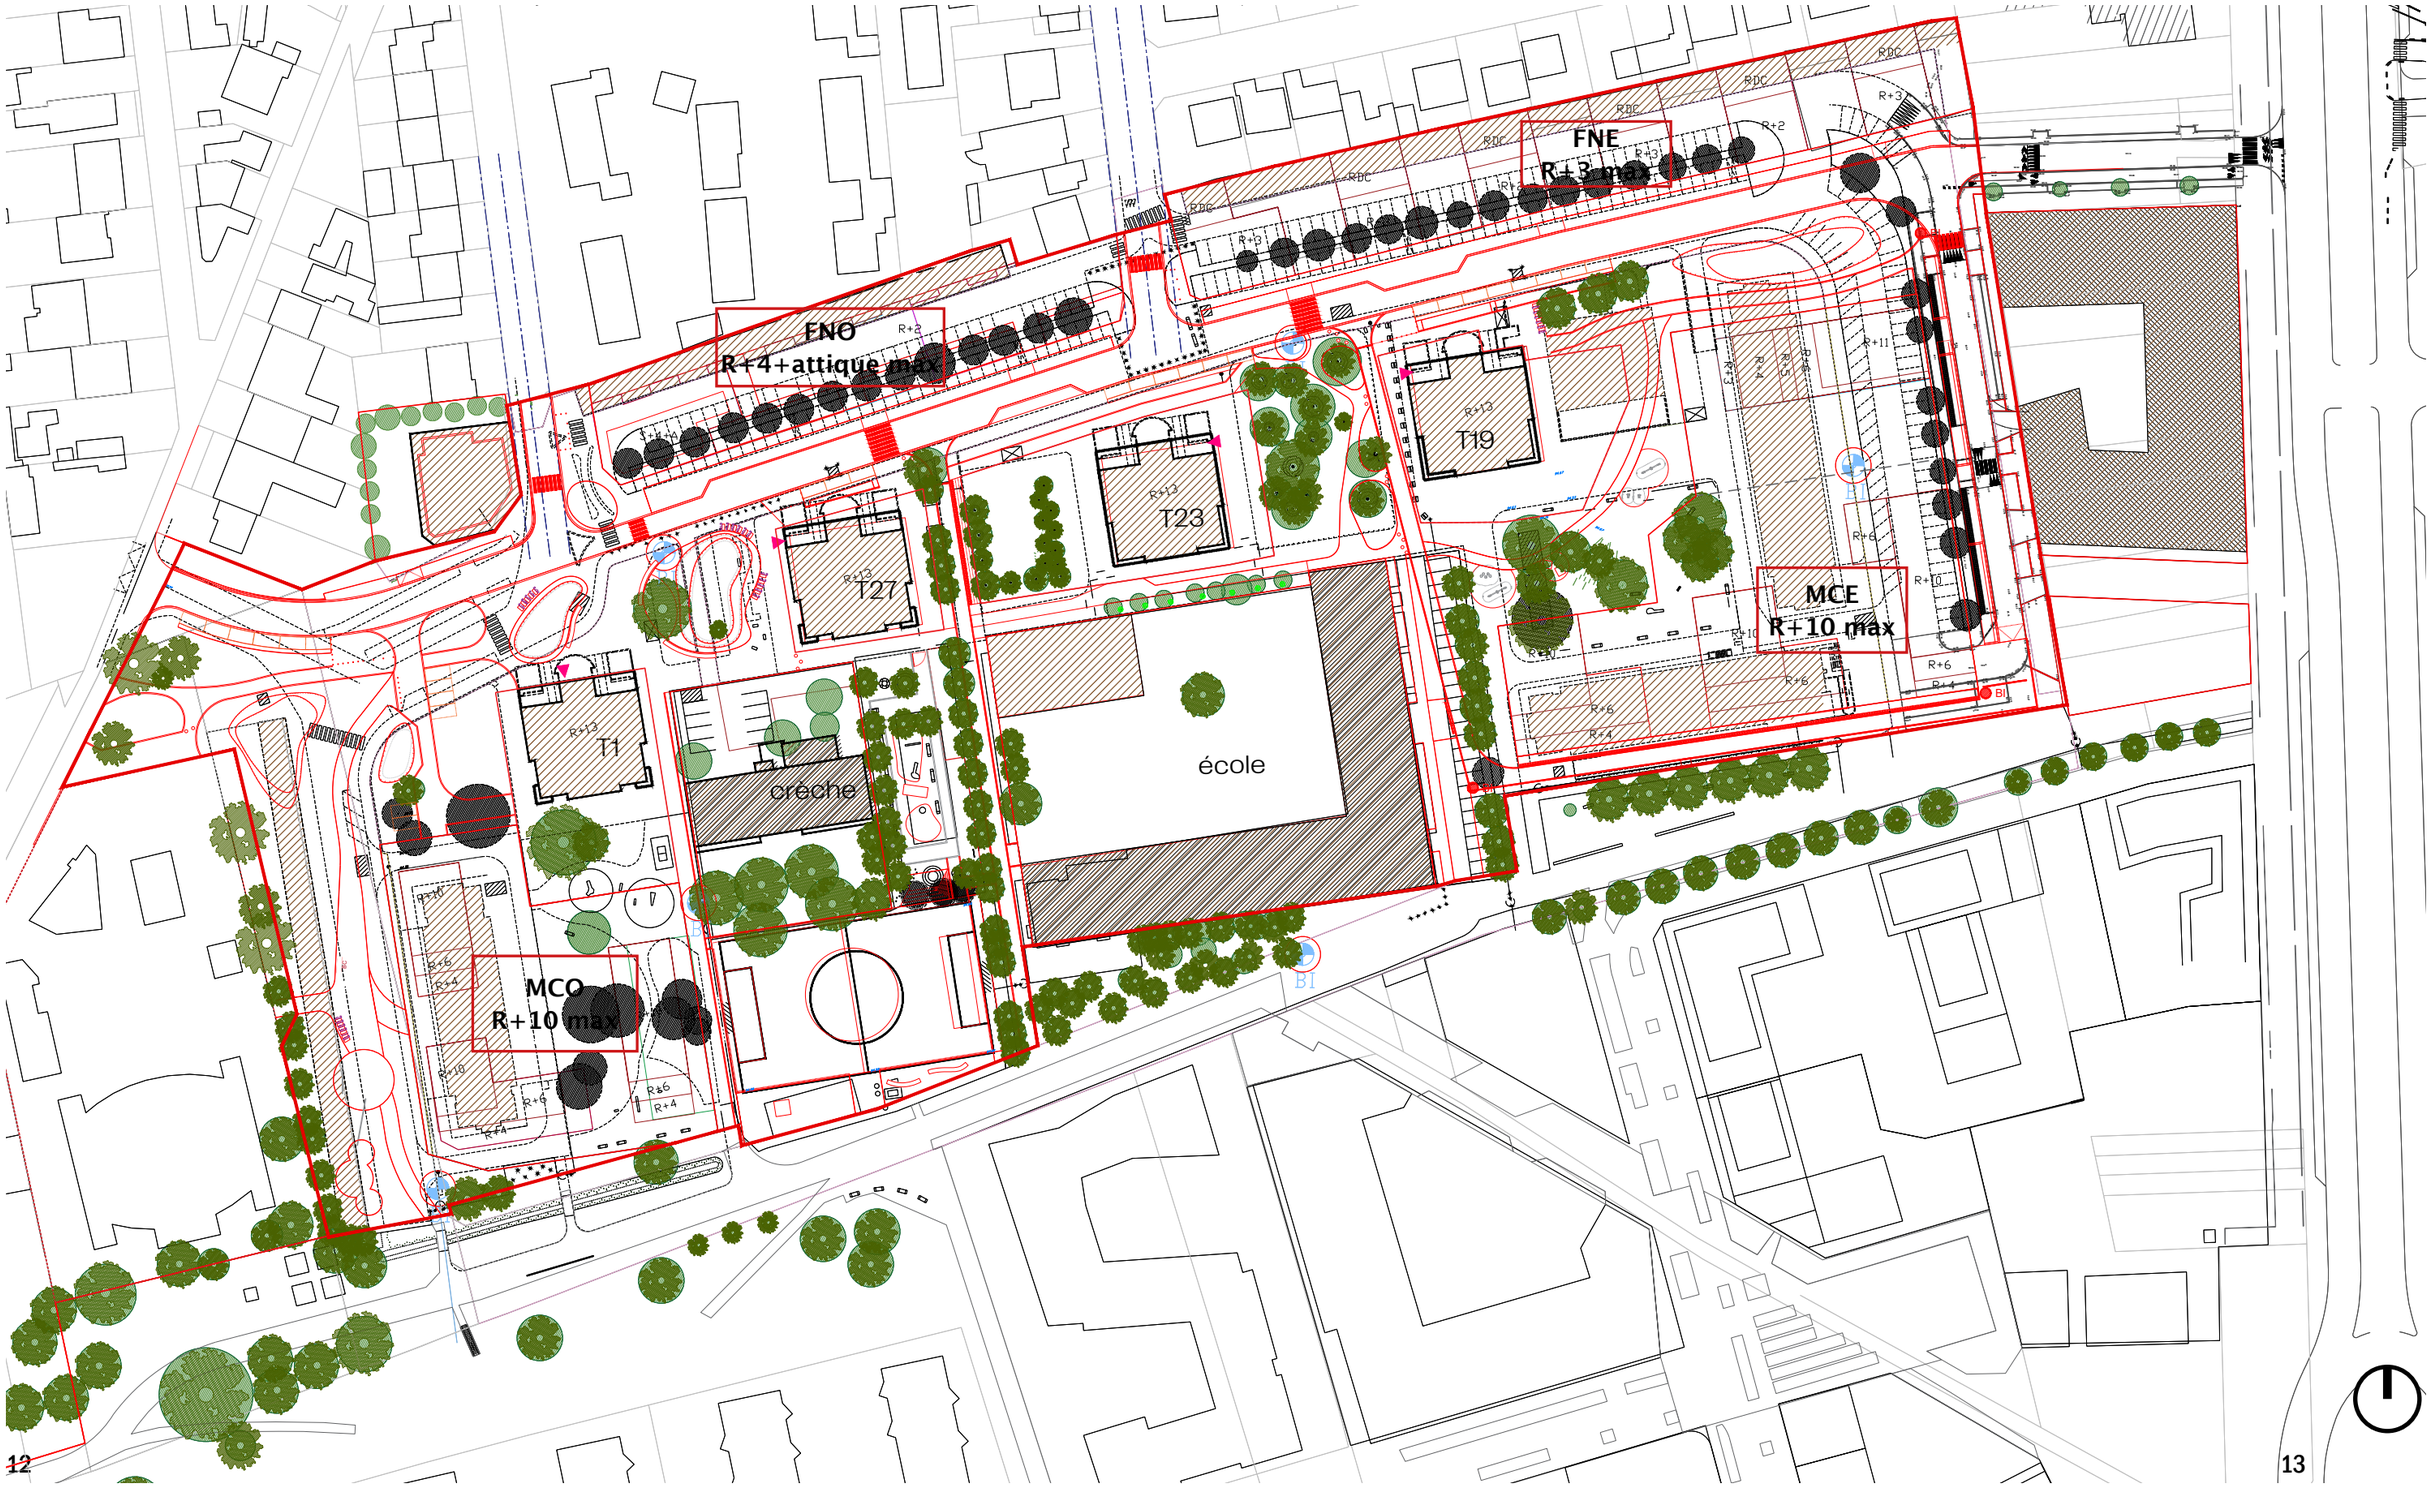

Une future accessibilité pompier inchangée

Lebon Lamartine – plan existant

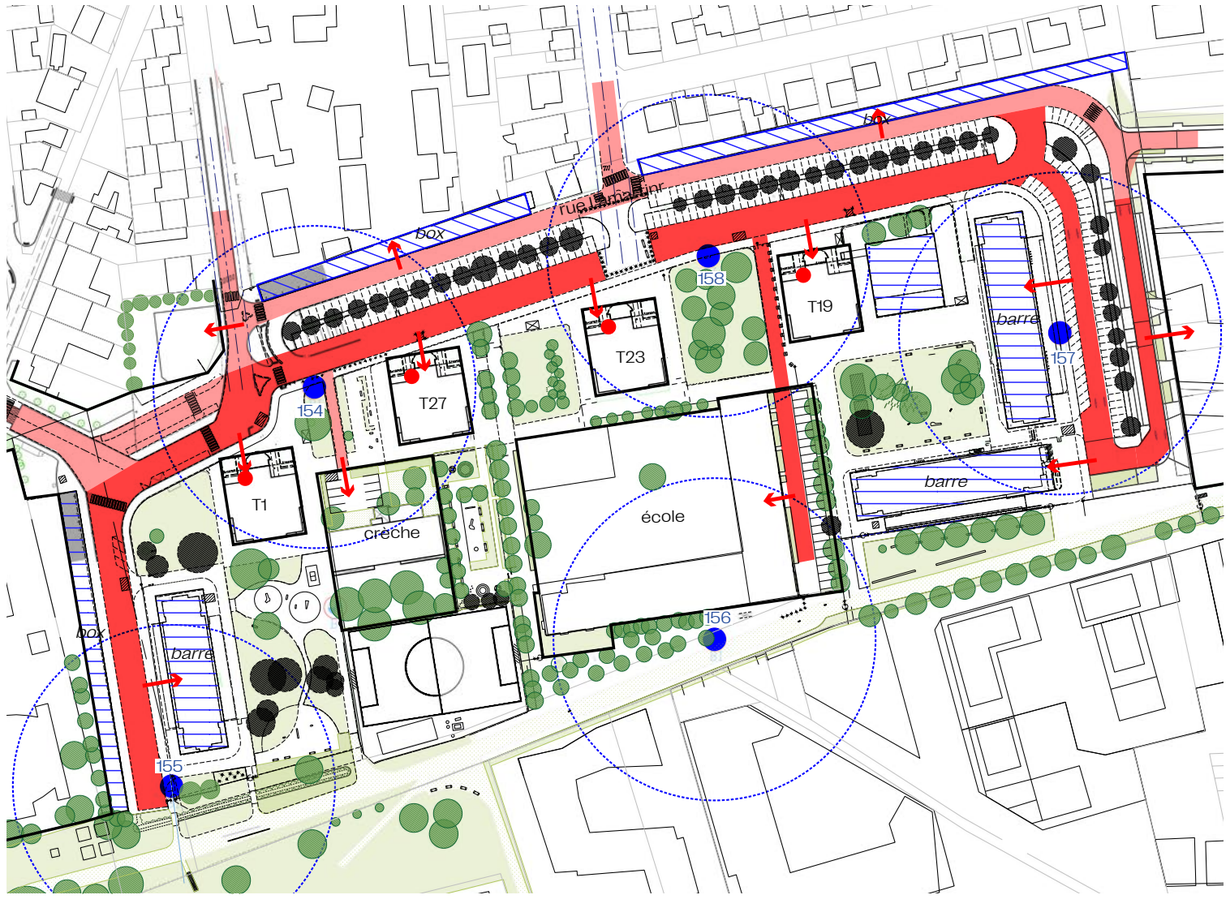

Lebon Lamartine – plan projeté

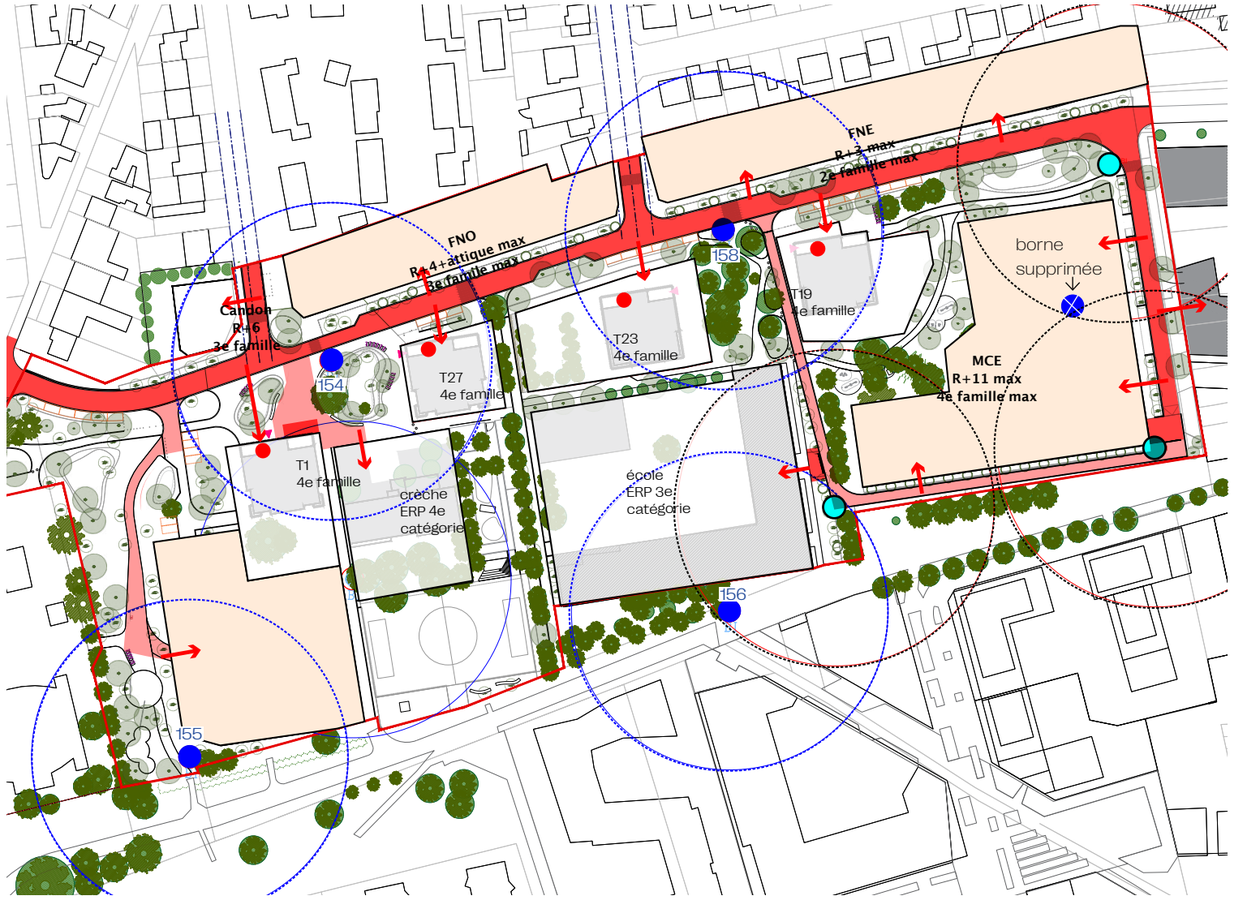

Aujourd'hui, le quartier est composé **de tours et de barres qui règnent entre le R+9 et le R+13**. Les barres sont en cours de démolition et/ou en cours de relogement. Par ailleurs, le projet vise à respecter les tours et leur environnement direct : **les futures constructions ne dépasseront pas le R+11.**

Pour les futures constructions, il est proposé de décliner 2 types de mode d'habiter :

1 – par des **collectifs hauts en gradins** dans les macrolots est et ouest (R+11), tout en laissant les tours régner

2 – par de **l'intermédiaire au nord**, avec une échelle plus basse en évitant les vis-à-vis en proposant une forme de politesse au regard des constructions voisines (maisons au nord notamment).

Voie engin

Voie échelle

Colonnes sèches

Borne incendie existante conservée + rayon 50m

Nouvelle borne incendie + rayon 50m

Les colonnes sèches des futurs bâtiments devront s'implanter à une distance maximum de 60m d'une borne incendie.

1 borne existante supprimée à l'est (dans l'emprise du MCE)
3 bornes créées à l'est

1/Les bâtiments de logements sont majoritairement classés en Habitation – 4ème famille. Les bâtiments seront accessibles par la voie engins. La distance entre les cages d'escalier et l'engin pompier sera inférieur à 50m.
2/Les franges sont classées en 2e ou 3e famille. Leur défense incendie se fera par la rue Lamartine.
Les bornes incendies sont localisées à moins de 50m d'une entrée / hall d'accès

Fonctionnement à terme

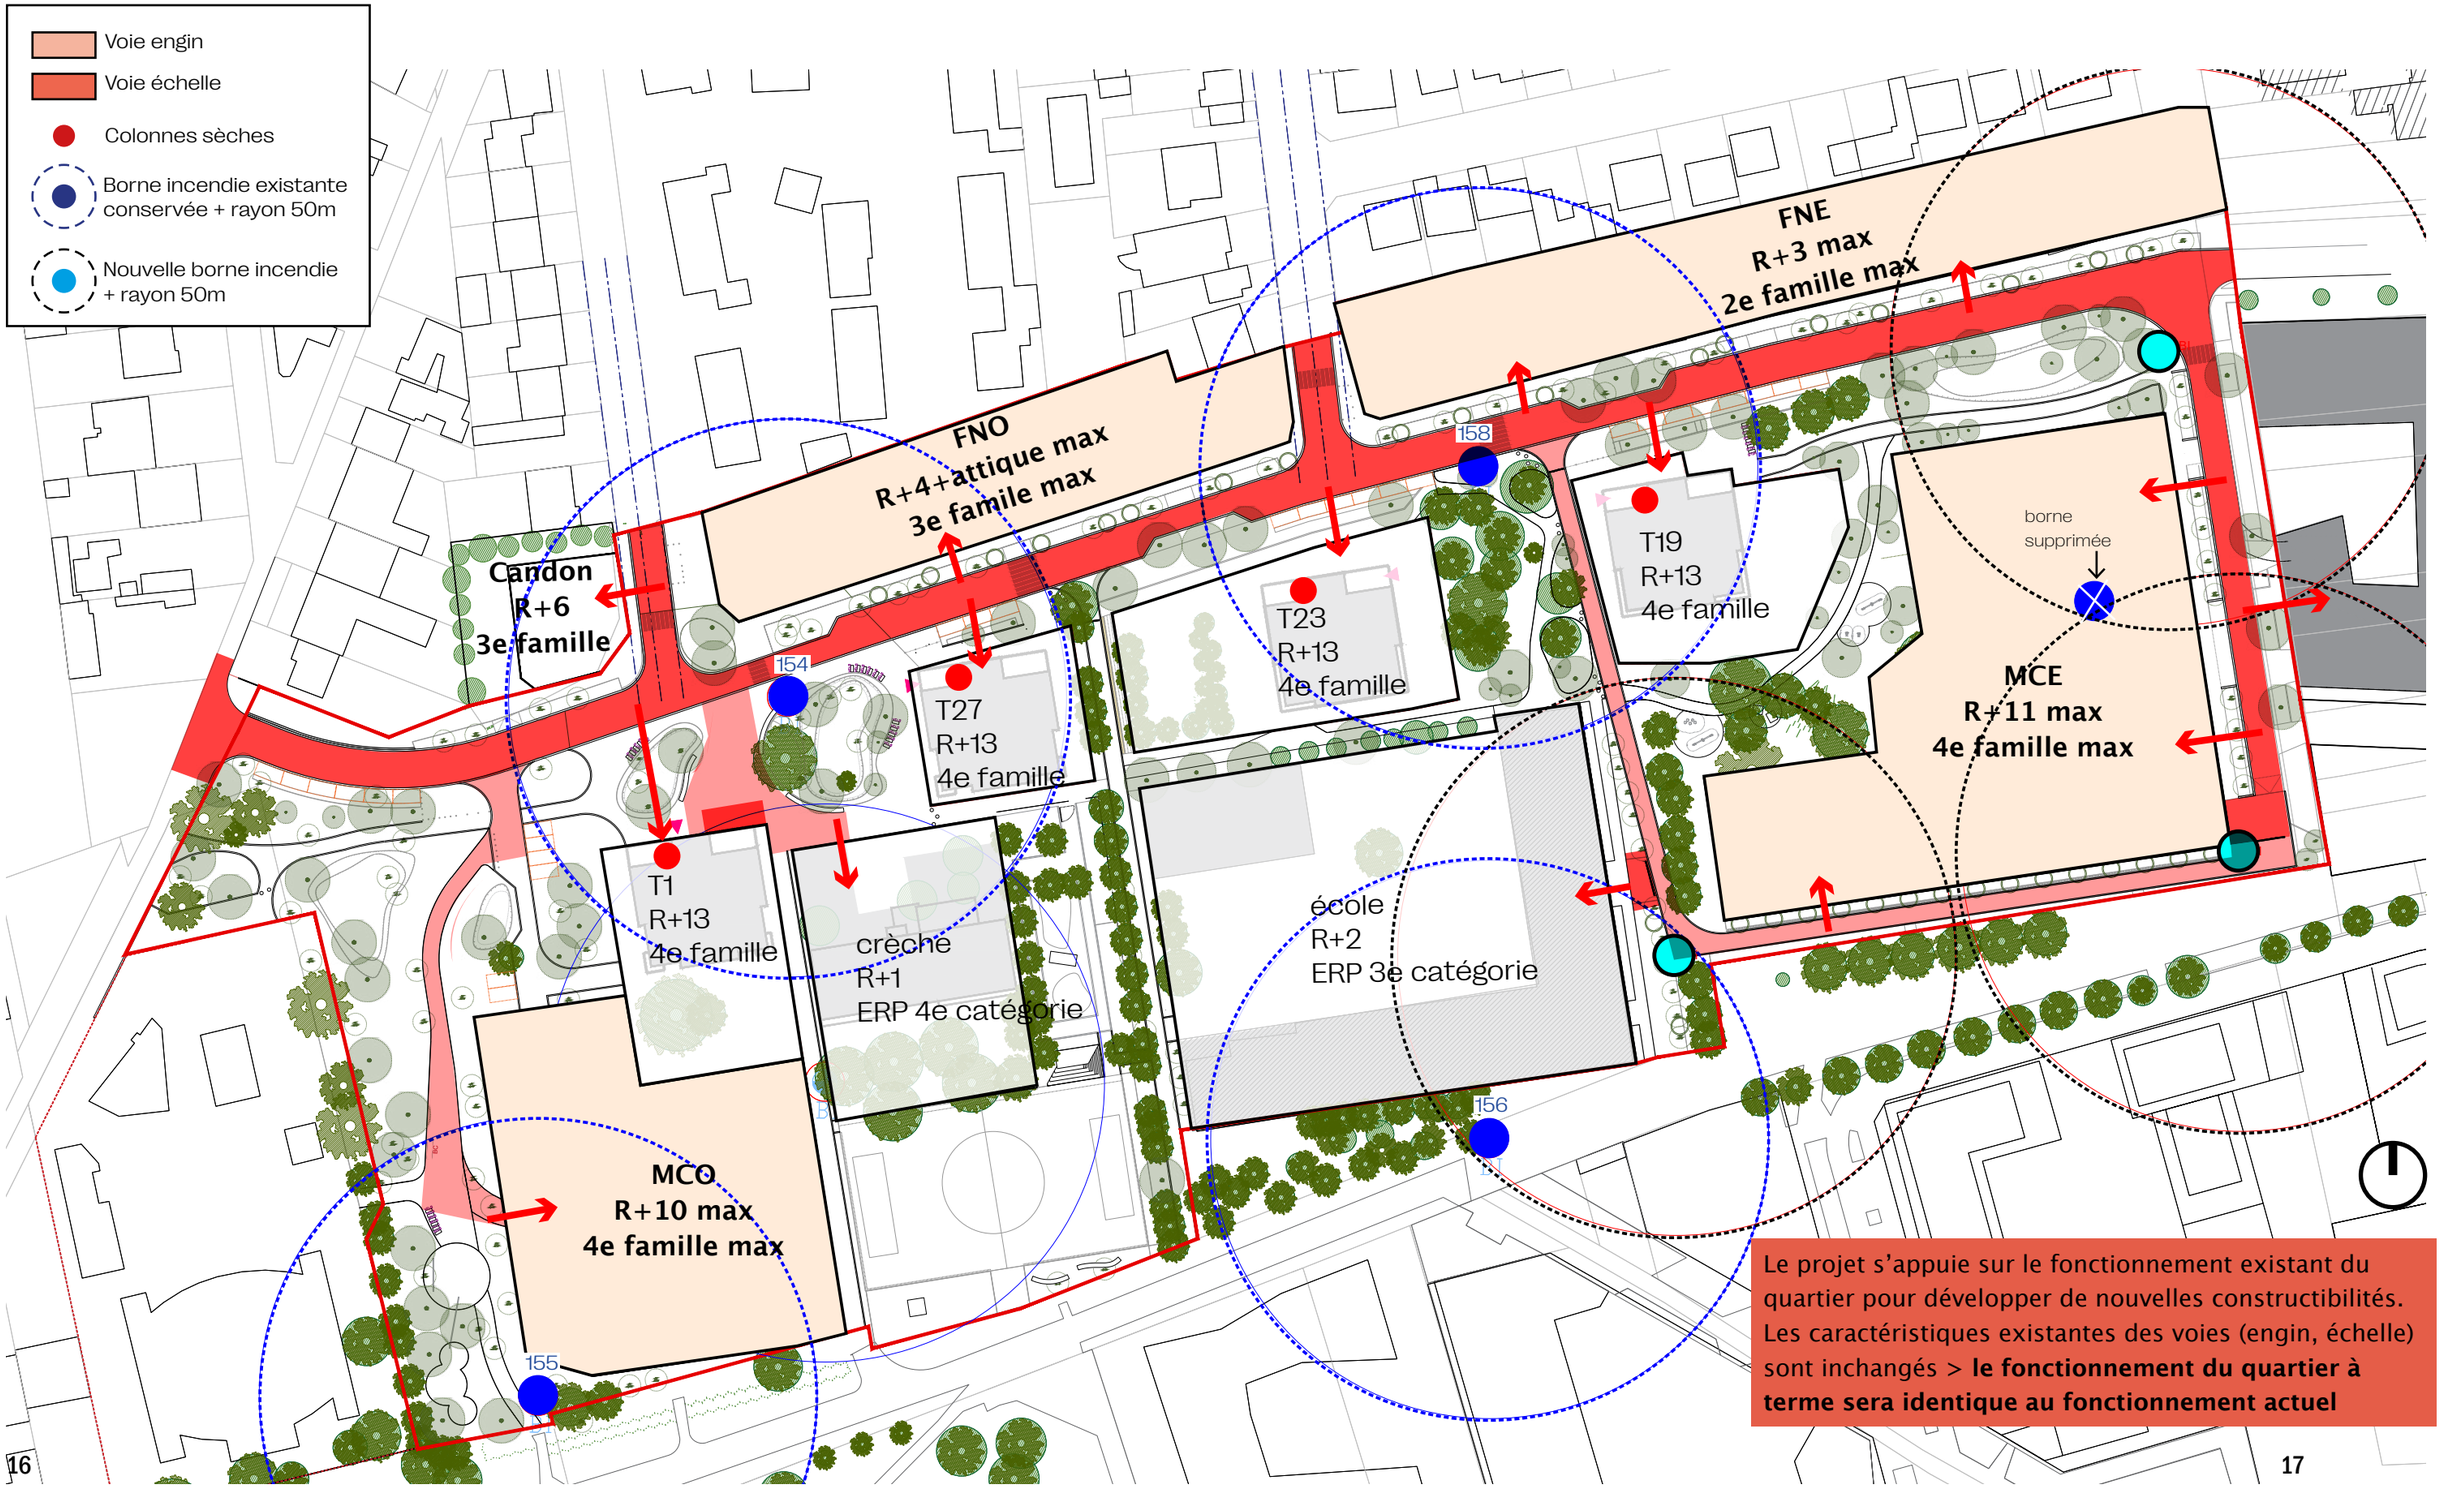

Le projet s'appuie sur le fonctionnement existant du quartier pour développer de nouvelles constructibilités. Les caractéristiques existantes des voies (engin, échelle) sont inchangés > **le fonctionnement du quartier à terme sera identique au fonctionnement actuel**

Détails bâtiments existants conservés

Tour 1 : 4e famille R+13
desserte assurée par la rue Lamartine (voie échelle) + assurée par le parvis qui sera circulable pour les engins de secours. Borne incendie localisée à -50m des escaliers + des colonnes sèches de la tour

Tour 27 : 4e famille R+13
desserte assurée par la rue Lamartine (voie échelle).
Borne incendie localisée à -50m des escaliers + des colonnes sèches de la tour

Crèche : ERP 4e catégorie R+2
desserte assurée par le parvis, (depuis la rue Lamartine) qui sera circulable pour les engins de secours. Borne incendie localisée à -50m des escaliers

Tour 23 : 4e famille R+13
desserte assurée par la rue Lamartine (voie échelle)
Borne incendie localisée à -50m des escaliers + des colonnes sèches de la tour

Tour 19 : 4e famille R+13
desserte assurée par la rue Lamartine (voie échelle)
Borne incendie localisée à -50m des escaliers + des colonnes sèches de la tour

Ecole: ERP 3e catégorie R+2
desserte assurée par la voie de l'école (voie engin).
Une portion de 4mx10m est aménagé devant l'école (voie échelle).
Borne incendie localisée à -50m.

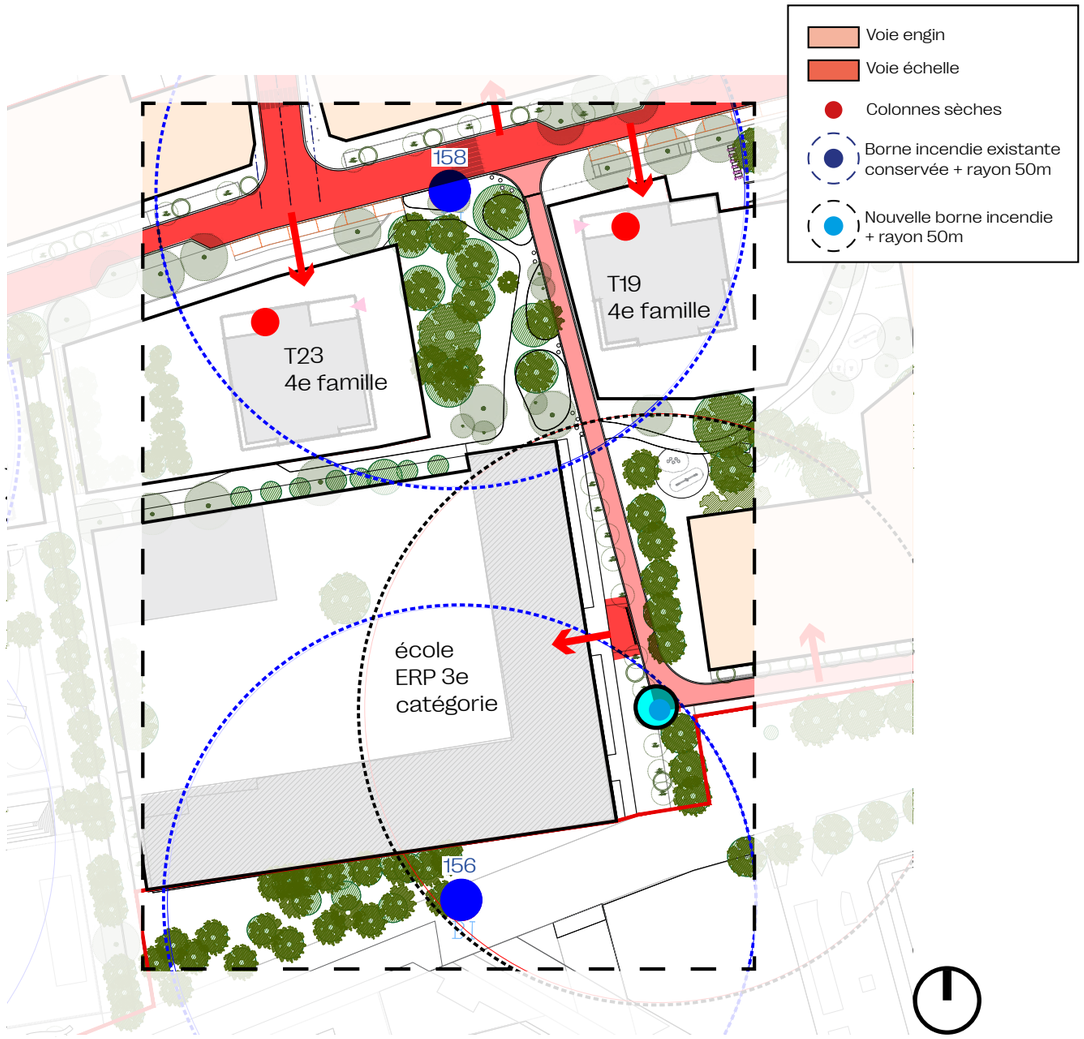

Détails desserte ilots constructibles

MCO : 4e famille R+10
desserte assurée depuis la rue Lamartine sur une voie engin dans la jardin ouest.
Borne incendie localisée à -50m des escaliers + les colonnes sèches des futures bâtiments seront localisées à -50m des bornes

FNO : 3e famille R+4+A
desserte assurée par la rue Lamartine (nécessité voie engin, dimensionnée voie échelle).
Borne incendie localisée à -50m des escaliers

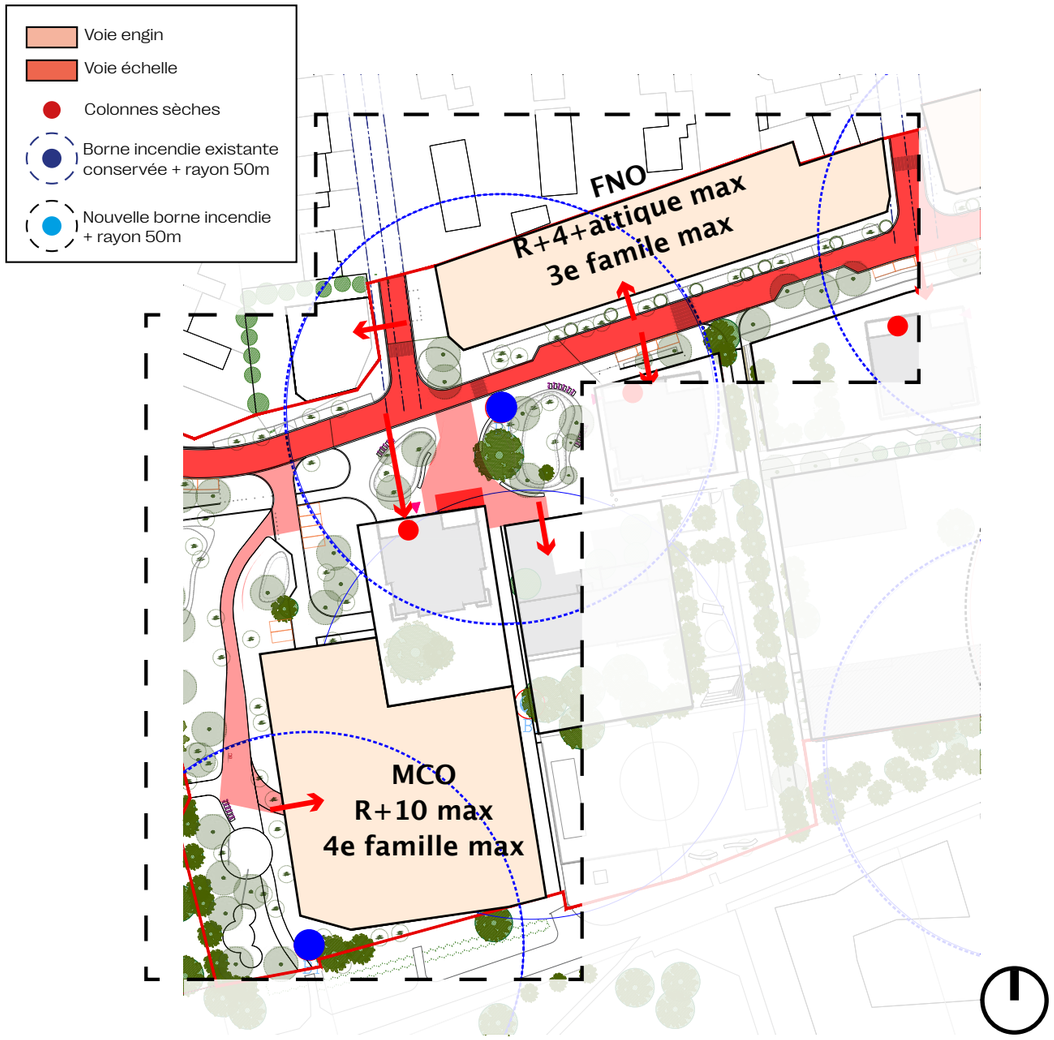

MCE : 4e famille R+11
desserte assurée depuis la rue Lamartine sur une voie engin dans la jardin ouest.
Borne incendie localisée à -50m des escaliers + les colonnes sèches des futures bâtiments seront localisées à -50m des bornes

FNE : 3e famille R+3
desserte assurée par la rue Lamartine (nécessité voie engin, dimensionnée voie échelle).
Borne incendie localisée à -50m des escaliers

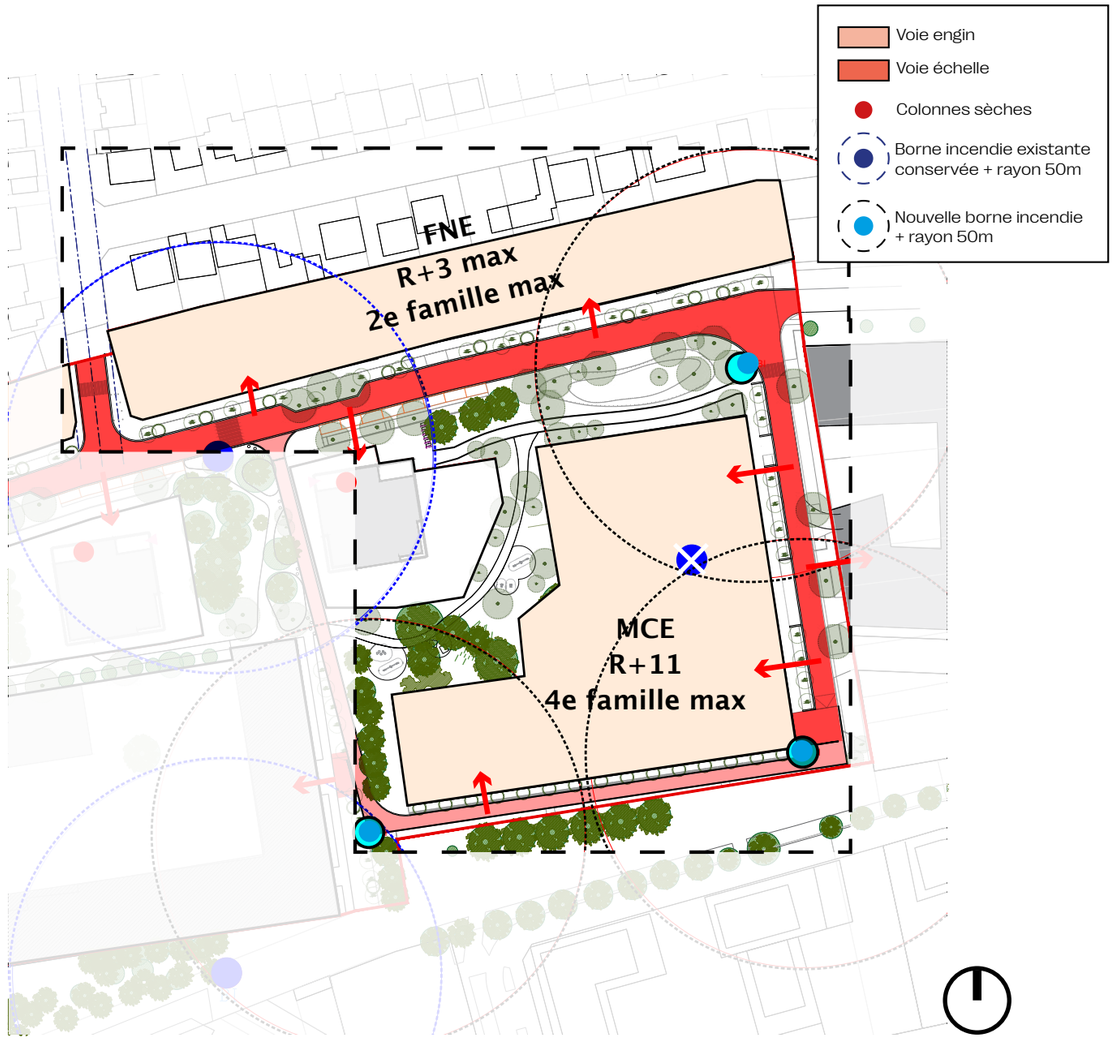

Vision globale

Un quartier renouvelé et animé

Un quartier ouvert sur la ville, diversifié et mixte.

300 logements sociaux réhabilités

460 nouveaux logements neufs et diversifiés

Des équipements rénovés

le groupe scolaire Robert Lebon,
la crèche Robert Lebon,
le terrain de foot

Des services en coeur de quartier

3 des locaux d'Economie Sociale et Solidaire en rez de chaussée

4 la maison des projets / tiers lieux jeunesse

5 local commun résidentiel

Un quartier paysager et piéton

Un total de 8000 m² d'espaces verts publics et 35% de pleine terre sur le quartier.

Nouvelle rue Lamartine, apaisée et paysagée

Des venelles piétonnes vers l'école et la coulée verte

Des espaces de rassemblement

La coulée verte

3 jardins publics en coeur de quartier, reliés à la coulée verte par des chemins piétons

1 Le jardin Est

2 Le jardin Ouest

3 Le jardin de jeux

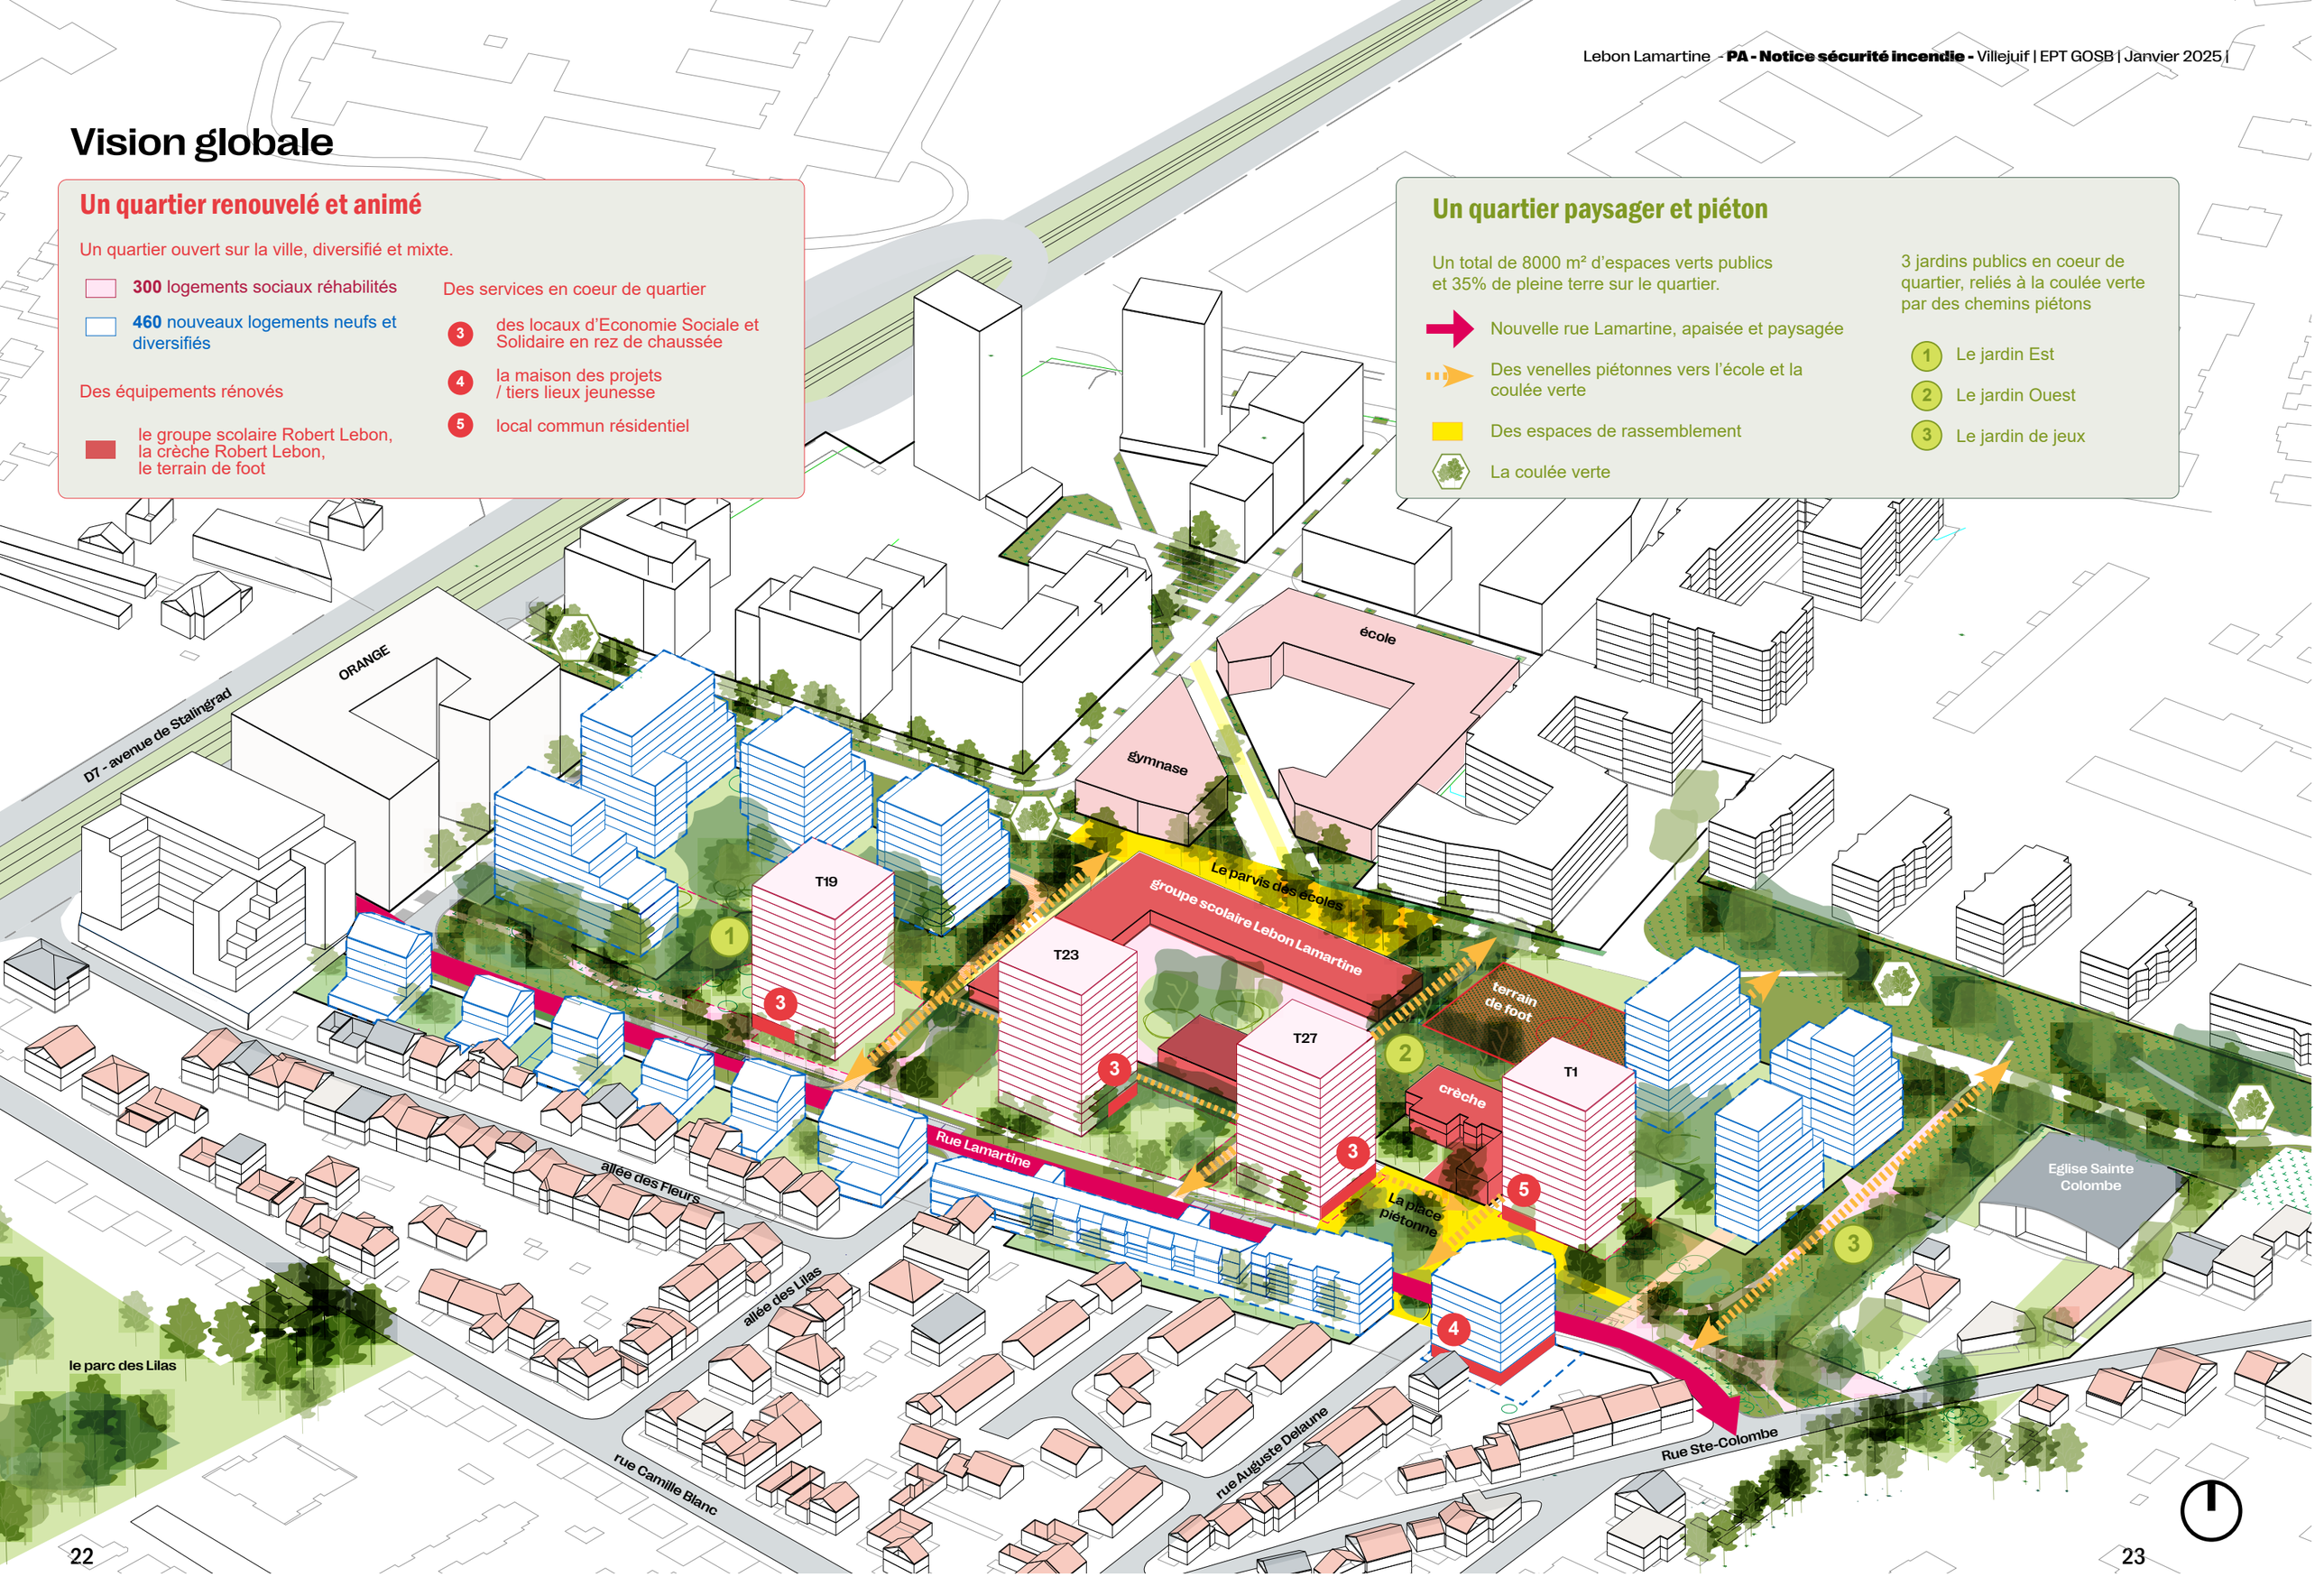

Les modes d'habiter

Aujourd'hui, le quartier est composé de tours et de barres qui règnent entre le R+9 et le R+13. Les barres sont en cours de démolition et/ou en cours de relogement.
De manière générale, le quartier est un lieu où l'on habite le ciel : par des vues spectaculaires sur le terrtitoire, par l'élancement des tours et par la réhabilitation de ces dernières qui comprendront des balcons pour mieux profiter du contexte.

Pour les futures constructions, il est proposé de décliner 2 types de mode d'habiter :

1 - par des **collectifs hauts en gradins** dans les macrolots est et ouest (R+11), tout en laissant les tours régner
2 - par de **l'intermédiaire**, avec une échelle plus basse en évitant les vis-à-vis en proposant une forme de politesse au regard des constructions voisines (maisons au nord notamment).

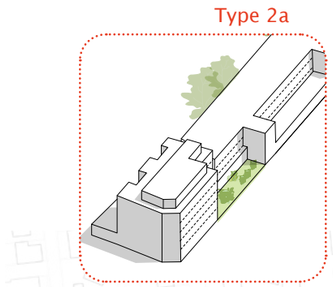

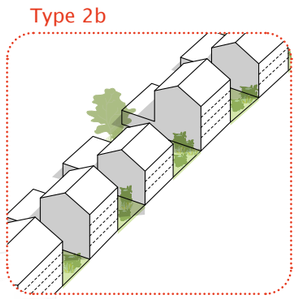

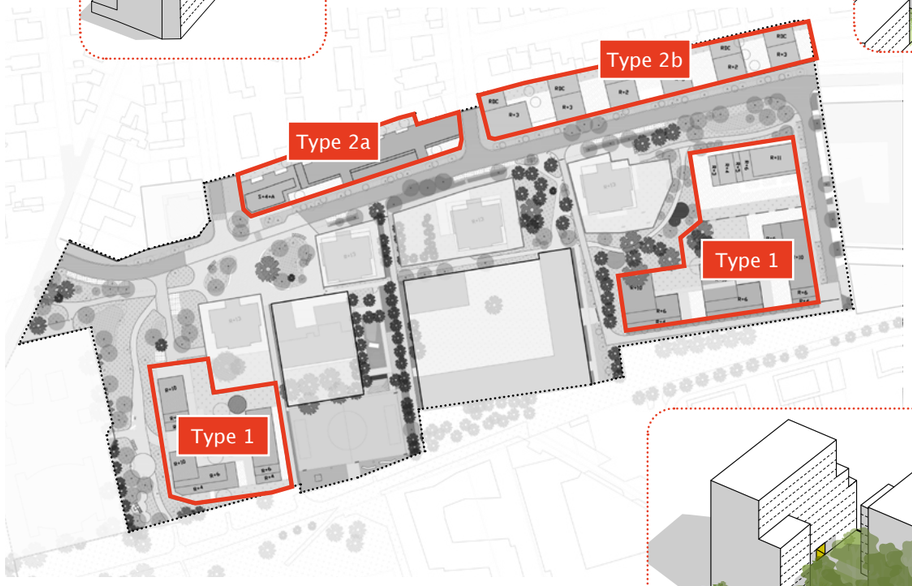

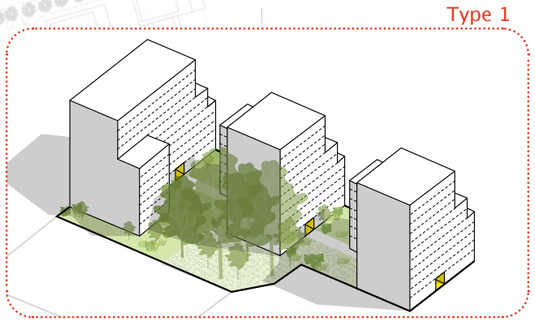

Répartition des lots constructibles

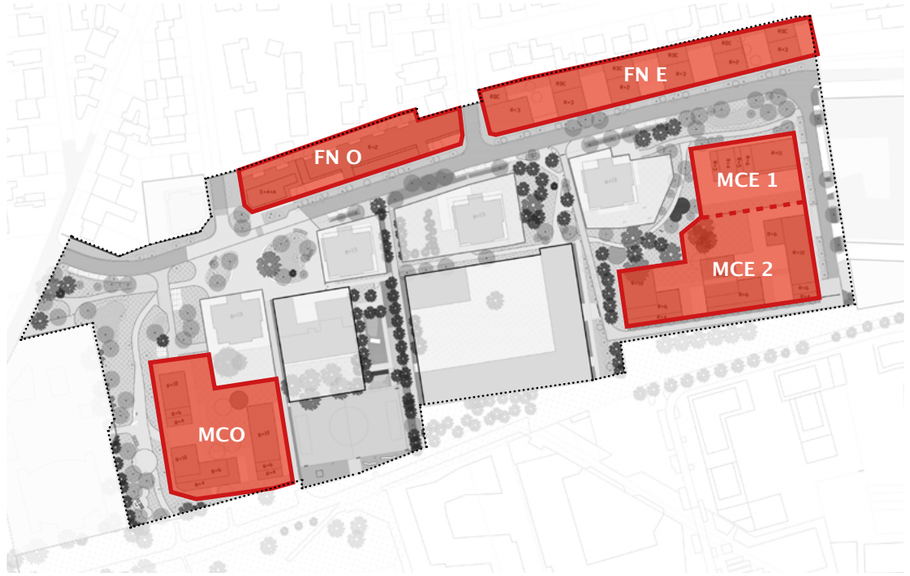

L'aménagement du quartier prévoit :
- la démolition de 263 logements (barres)
- la réhabilitation de 300 logements (tours)
- la construction de 466 logements

ILOT	EMPRISE	NOMBRE DE LOGEMENT
FNO	2226 m²	~ 40 logements
FNE	3236 m²	~ 53 logements
MCE 1	1600 m²	~ 53 logements
MCE 2	3531 m²	~ 169 logements
MCO	3298 m²	~ 117 logements

FN Est
R+3max
2e famile max

FN Ouest
R+4+attique max
3e famile max

Candon
R+6
3e famille

MLE 1

MLE 2
R+11
4e famille max

ML Ouest
R 10+max
4e famille max

Tour 1
R+13
4e famille

Tour 19
R+13
4e famille

Tour 23
R+13
4e famille

Tour 27
R+13
4e famille

Ecole exi
R+2
ERP 3 cat

Creche exi
R+1
ERP 4 cat

borne supprimée

BI

Secteur Lebon-Lamartine
MAITRISE D'OEUVRE URBAINE

Permis d'aménager

Plan schématique classement pompier

LEGENDE - FAMILLES

Habitations existantes (tours)
4e

ERP existants conservés
3e 4e

BI bornes incendies existantes conservées

BI bornes incendies créées

rayon 50m

stationnement

voie échelle

voie engin

REMARQUES

Les colonnes sèches des futurs bâtiments devront s'implanter obligatoirement à une distance maximum de 60m d'une borne incendie.

MAÎTRISE D'OUVRAGE :

EPT GOBS
11 Avenue Henri Farman
BP 748
94398 Orly Aérogare Cedex

MAÎTRISE D'OEUVRE :

Marniquet Aubouin
21 rue Pierrecourt - 75020 Paris
tel : 01 48 05 53 25 - fax : 01 48 05 55 14
@ : atelier@marniquetaubouin.com

Echelle : 1/500

Date: Janvier 2025

Planche N°
Indice : A05