
20 mars 2026, équinoxe de printemps : l'ombre du projet atteint 11 façades à fenêtres de 5 maisons des Castors

Projet A26 BLM, permis PC 094 076 26 01015, rue Lamartine à Villejuif. Copropriété des Castors de Sainte Colombe, allée du Sapin Bleu et rue Auguste Delaune.

Moments de la journée où l'ombre du projet atteint chaque façade à fenêtres (pas de 5 min)

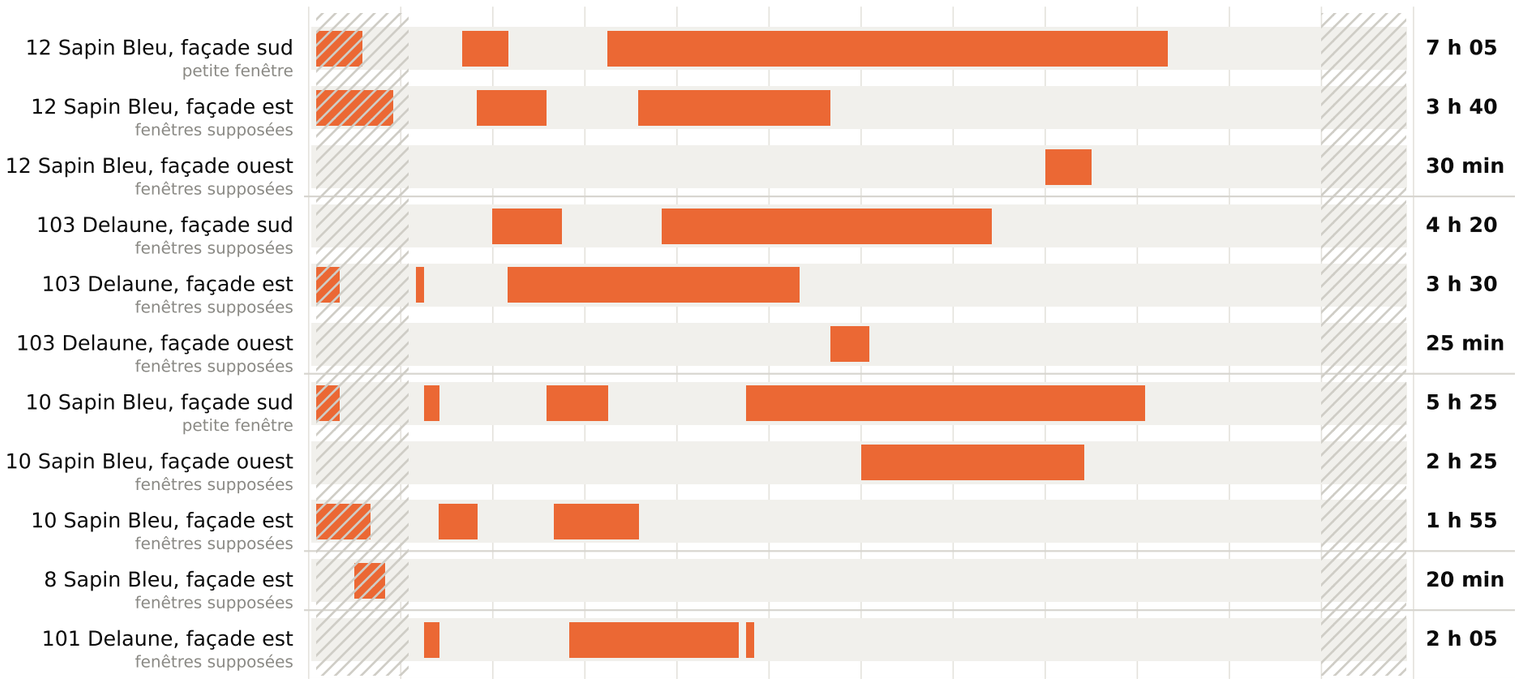

Fond gris clair : jour (lever du soleil 7 h 02, coucher 18 h 56). Hachures : soleil à moins de 10°. Durée totale à droite.

La règle (fiche de lot, citée par la note Trans-Faire)

« A l'équinoxe de printemps, l'ombre portée ne devra pas affecter les façades avec des ouvertures. »

À vérifier : la citation figure sur la page du lot voisin Frange Nord-Est ; il faut la fiche du lot Frange Nord-Ouest.

Ce que conclut la note Trans-Faire (mars 2025)

« A l'équinoxe de printemps et d'automne, le projet n'a que très peu d'incidence sur le tissu pavillonnaire au nord. »
Projet « en phase pré-AVP » ; aucune vérification fenêtre par fenêtre.

Ce que montre notre maquette (plans du permis)

L'ombre du projet atteint 11 façades à fenêtres de 5 maisons.
3 d'entre elles pendant plus de 4 heures :

- 12 Sapin Bleu, façade sud : 7 h 05
- 103 Delaune, façade sud : 4 h 20
- 10 Sapin Bleu, façade sud : 5 h 25

Heure par heure : en orange, l'ombre ajoutée par le projet au sol ; points orange, fenêtres (supposées) que cette ombre atteint

Gris clair : ombre qui existe déjà sans le projet (bâtiments actuels, mur existant de 2 m). Gris foncé : le projet. Maisons étudiées en blanc.



Méthode et limites : soleil calculé pour Villejuif le 20 mars 2026, en heure légale, toutes les 5 minutes, par ciel dégagé. Une façade est « atteinte » quand au moins un de ses points (à 0,5, 1,5 ou 2,5 m du sol) passe à l'ombre du projet.
Fenêtres des maisons supposées (2 par façade), sauf la petite fenêtre sud des 10 et 12 Sapin Bleu, indiquée par les habitants. Projet reconstitué d'après les plans du permis (plan du rez-de-chaussée et plan des toitures calés sur le cadastre, environ 0,5 m près).
Mur existant de 2 m compté, avant comme après ; arbres prévus non comptés. Estimation indépendante, à titre indicatif : seule une étude professionnelle fait foi. Maquette interactive : canongauss.github.io/SapinBleu-Lamartine · planche établie le 23 octobre 2026.