Docusign Envelope ID: 768CA9BC-72CD-4AB4-BAB7-6AD7892DDC2C

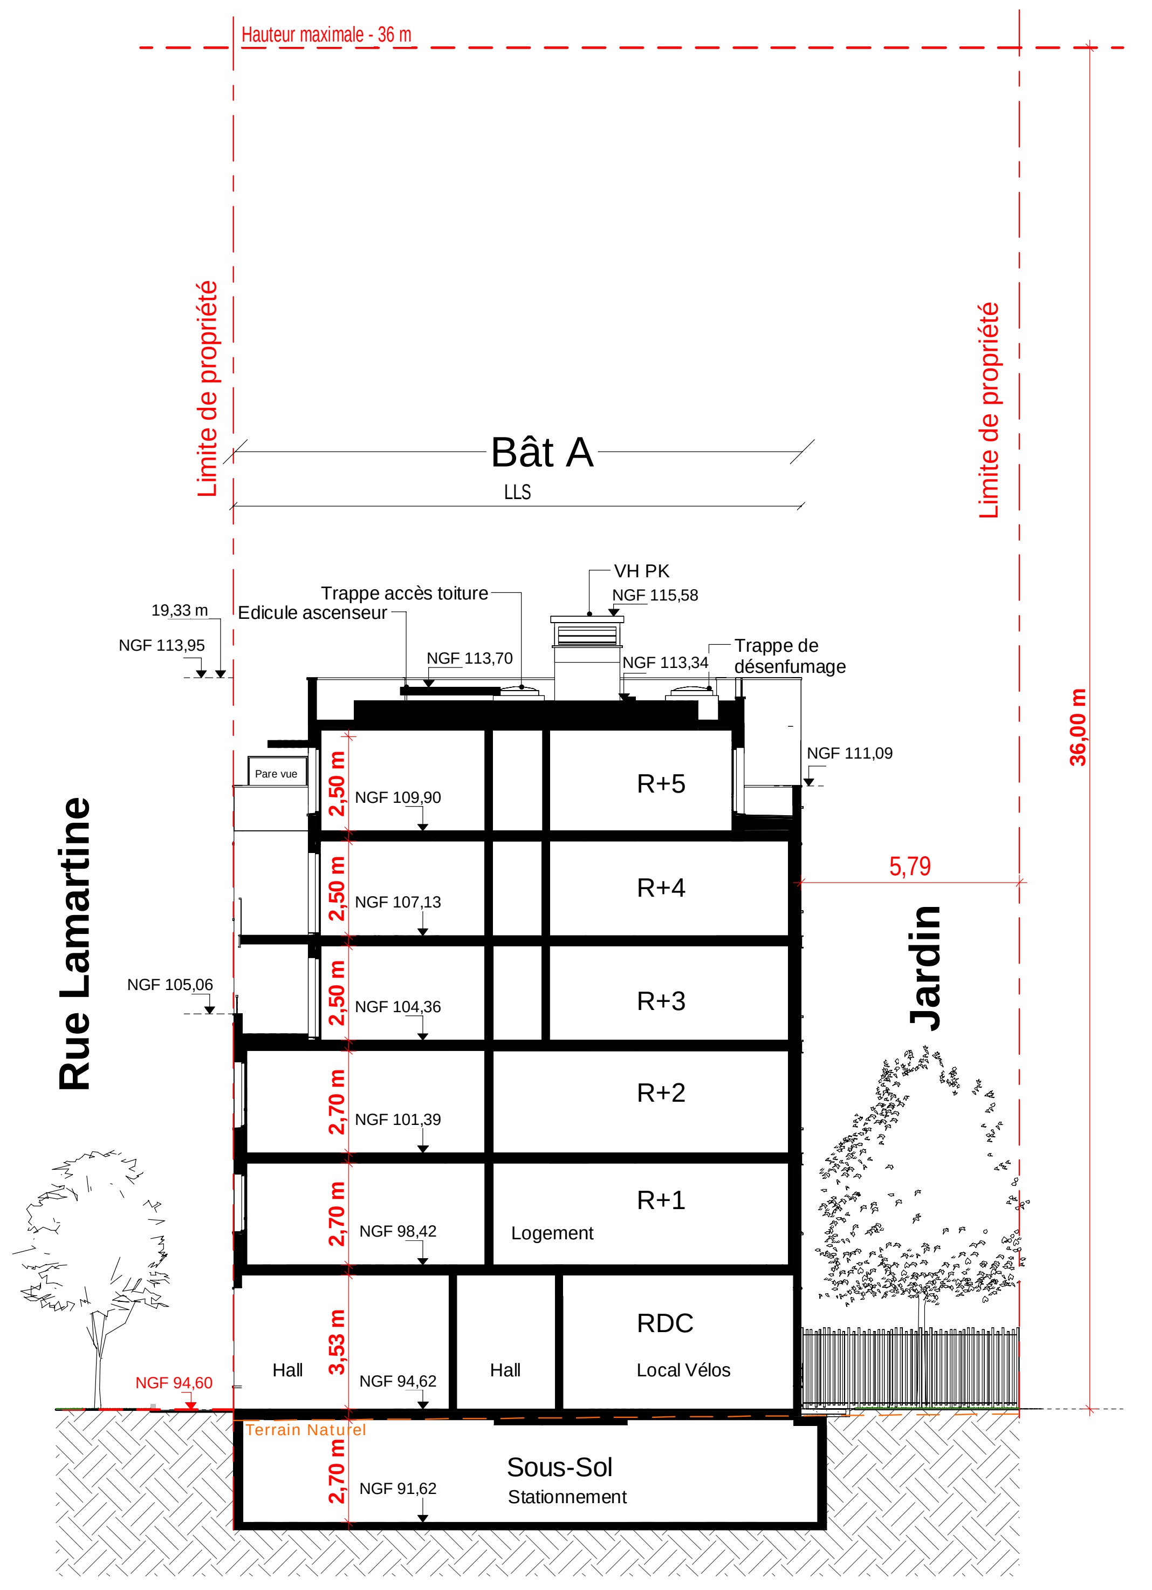

A. Coupe AA
Echelle : 1 : 200ème

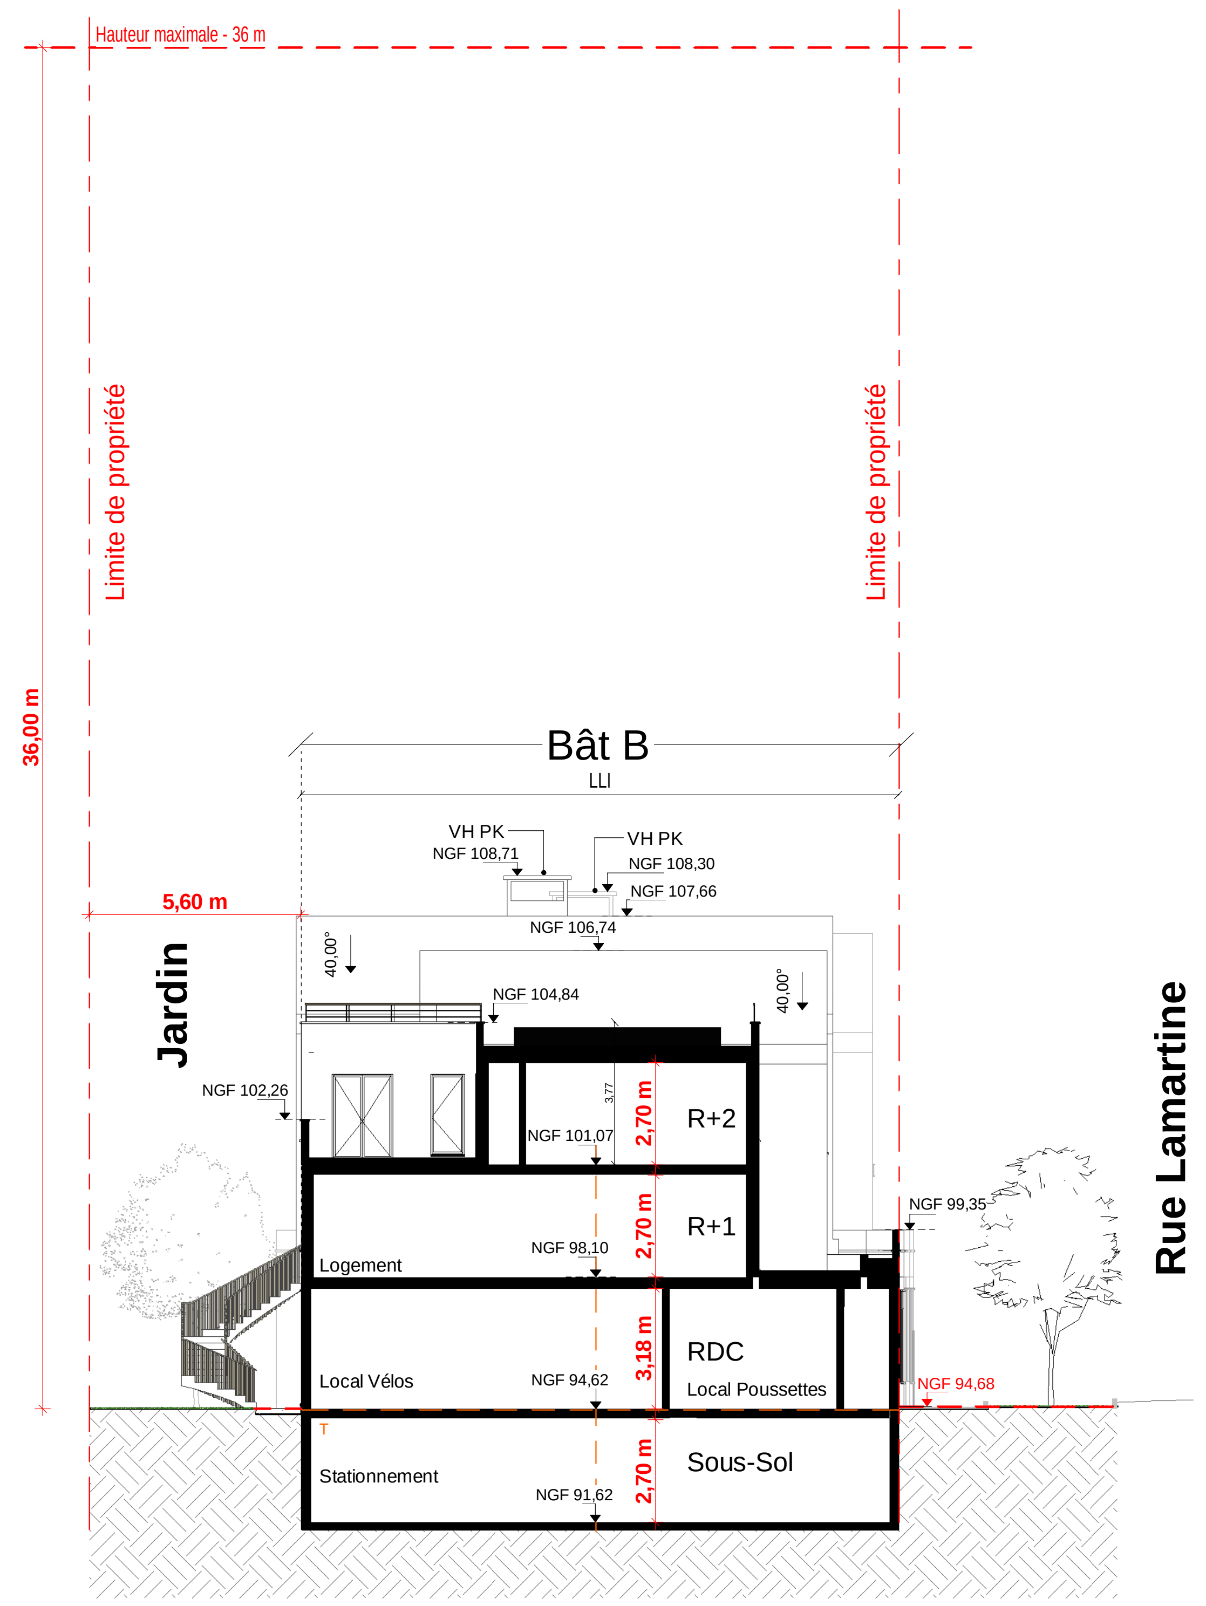

B. Coupe BB
Echelle : 1 : 200ème

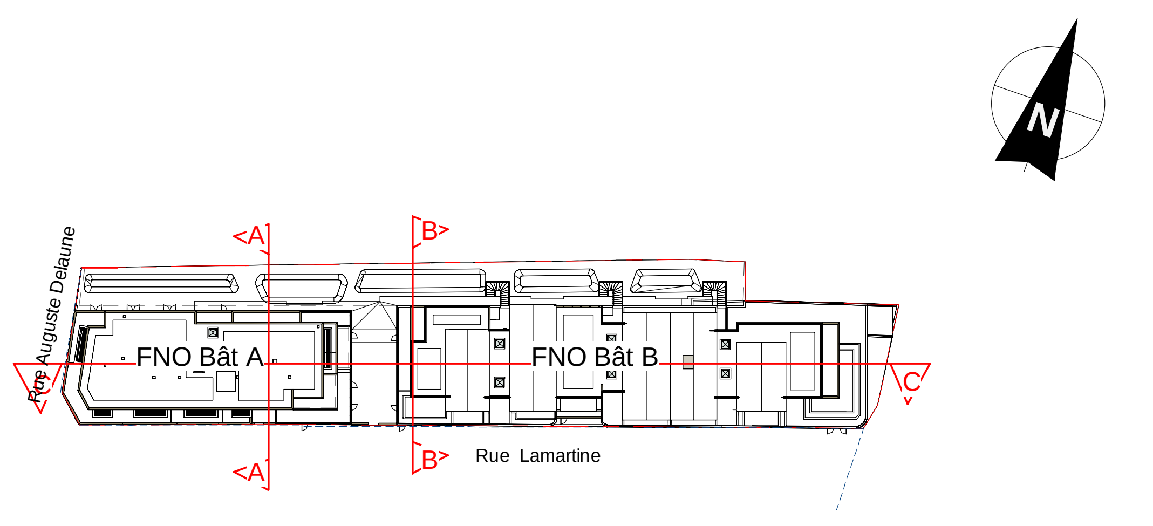

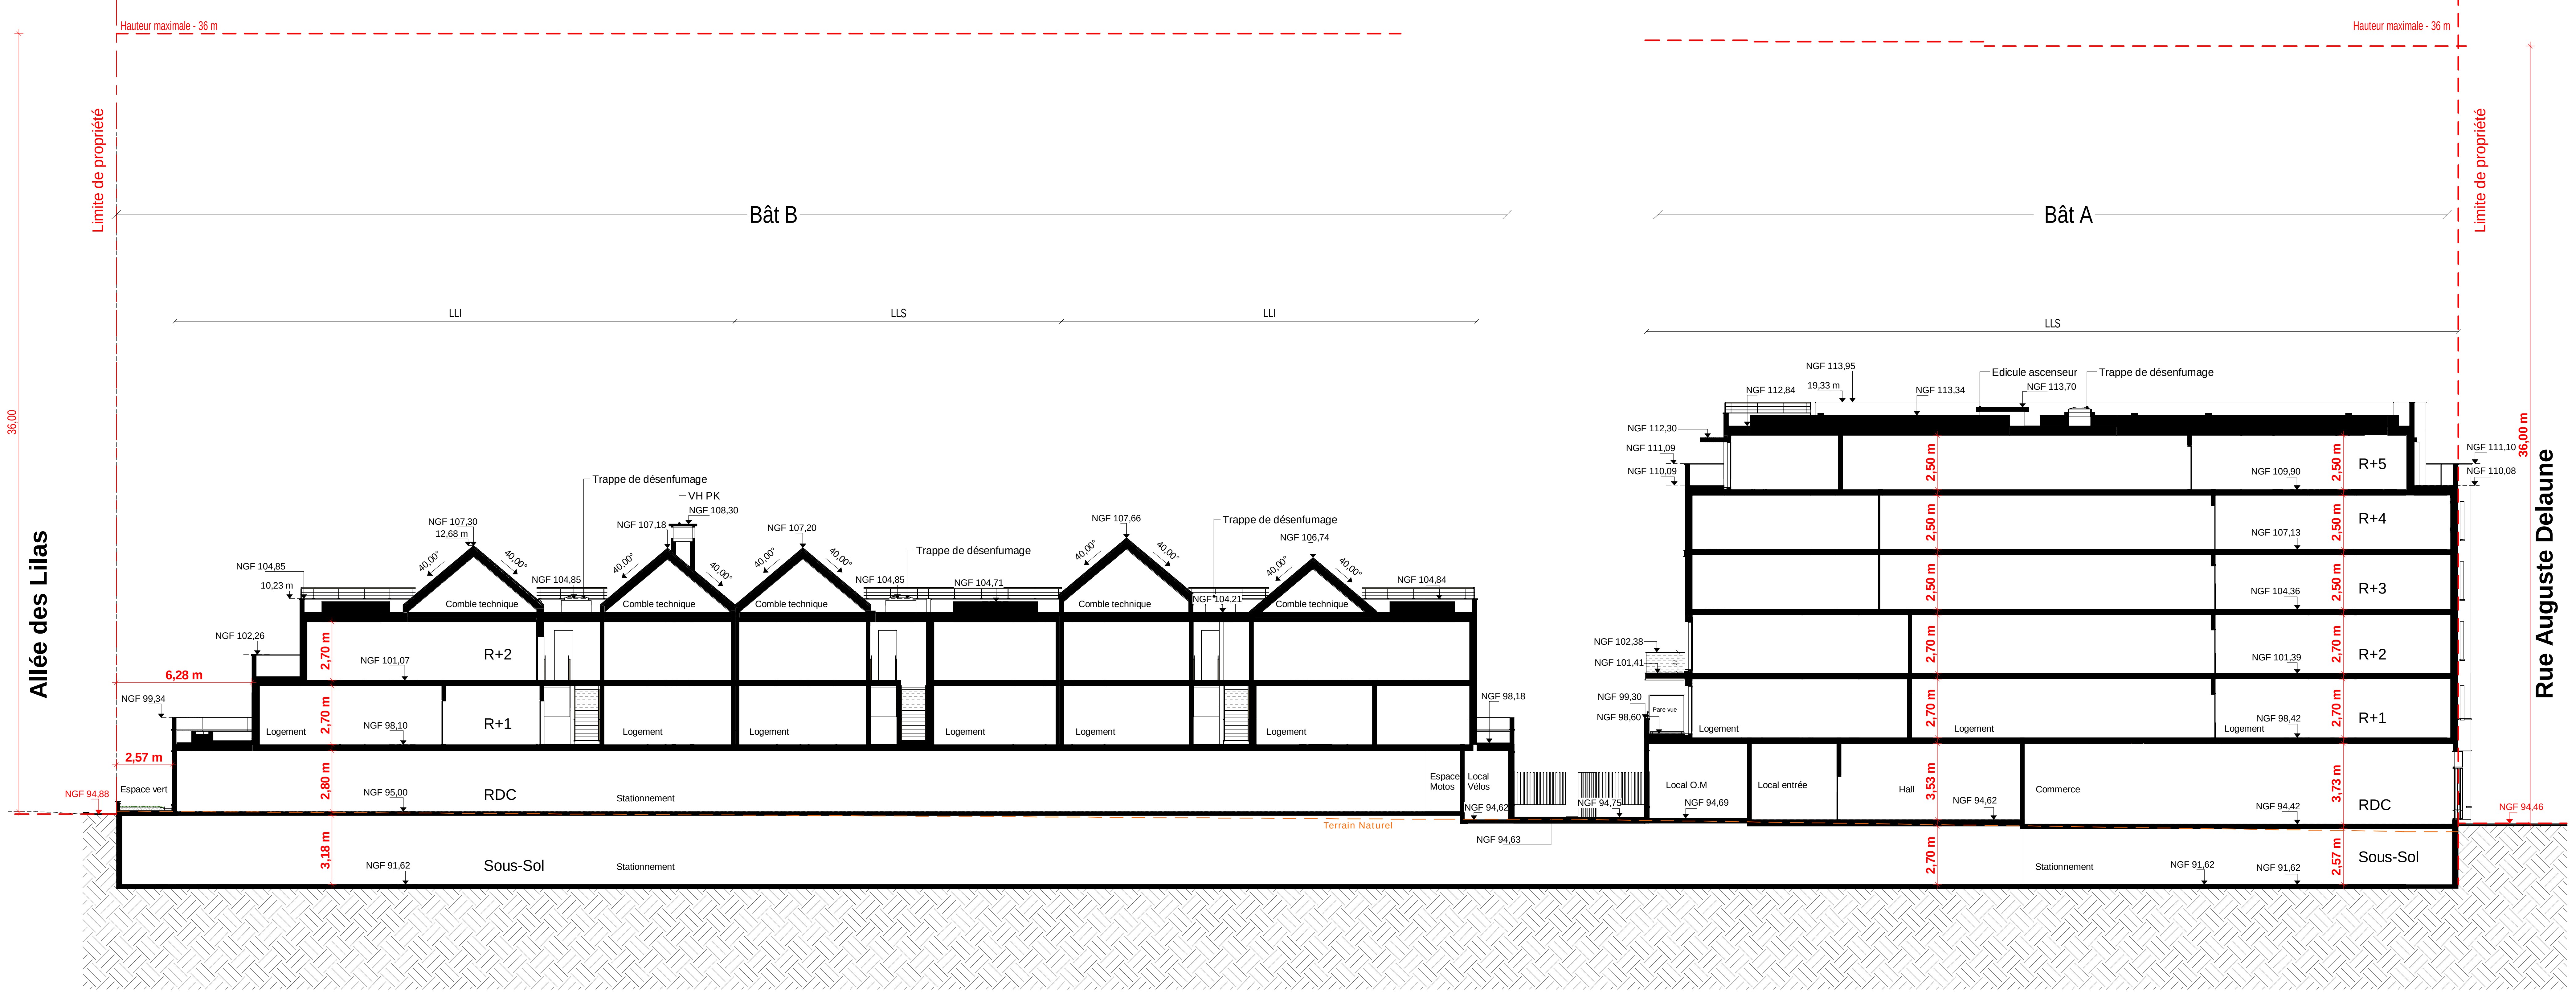

C. Coupe CC
Echelle : 1 : 200ème

Les côtes NGF mentionnées sont données à titre indicatif et restent soumises à ultérieure synthèse avec le plan d'aménagement

0 4m 8m

Maîtrise d'Ouvrage

SCCV VILLEJUIF
LEBON LAMARTINE
FNE-FNO

121 Avenue de Malakoff 75116 Paris

Signed by:
François Daguet
B6701235FCC444D...

Rue LAMARTINE

PROJET A26 BLM

PROJET QUARTIER LEBON LAMARTINE

PC- FRANGE NORD OUEST- LEBON LAMARTINE

Titre
Plan en coupe du terrain et de la construction - Art. R.431.10b

N°
PC3

Date
Mars 2026

Réf
3881

Echelle
1/200

Indice	Date	Modifications
2	Date 2	Révision 2

Maîtrise d'Oeuvre

- A26 BLM -
167 rue de Vaugirard-75015 PARIS
www.a26blm.eu - 01.45.67.09.02
SAS au capital de 33 100 €
NAF 7111Z-SIRET 410 007 249 00015
Ordre N°National S03534
TVA FR 67 410 007 249

Architectes-Urbanistes
Agence certifiée ISO 9001 - ISO 14001

167, rue de VAUGIRARD - 75015 PARIS
Tél: 01.45.67.09.02 - email : contact-blm@a26.eu

Architectes-Paysagistes
11 rue Beauregard -75002 Paris
Tél: 01.53.26.77.32 - email : agence@compagniedupaysage.fr

Infrastructures et Construction France
10 place Fulgence Bienvenue- 77600 Bussy Saint-Georges
Tél: 01.60.37.55.37 - email : marnevallee@apave.com

B.E.T
23 rue Raspail - 94200 Ivry-sur-Seine
Tél: 01.49.87.04.90 - email : contact@epdc.fr

C:\Users\dcoco\Documents\0-REVIT-LOCALS\3881_VIL_EME_FNO_CENTRAL_dcocoAP3D2.rvt 05/03/2026 09:07:52