Docusign Envelope ID: 768CA9BC-72CD-4AB4-BAB7-6AD7892DDC2C

Maîtrise d'Ouvrage

SCCV VILLEJUIF
LEBON LAMARTINE
FNE-FNO

121 Avenue de Malakoff 75116 Paris

Signed by:
François Daguet
B6701235FCC444D...

Rue LAMARTINE

PROJET A26 BLM

PROJET QUARTIER LEBON LAMARTINE

PC- FRANGE NORD OUEST- LEBON LAMARTINE

Titre		N°
Imprimé du dossier spécifique		**PC39-40**
Date: Mars 2026	Réf: **3881**	Echelle: ECH :

Indice	Date	Modifications

- A26 BLM -
167 rue de Vaugirard-75015 PARIS
www.a26blm.eu - 01.45.67.09.02
SAS au capital de 33 100 €
NAF 7111Z-SIRET 410 007 249 00015
Ordre N°National S03534
TVA FR 67 410 007 249

Maîtrise d'Oeuvre

Architectes-Urbanistes
Agence certifiée ISO 9001 - ISO 14001

167, rue de VAUGIRARD - 75015 PARIS
Tél: 01.45.67.09.02 - email : contact-blm@a26.eu

Architectes-Paysagistes
11 rue Beauregard -75002 Paris
Tél: 01.53.26.77.32 - email : agence@compagniedupaysage.fr

Infrastructures et Construction France
10 place Fulgence Bienvenue- 77600 Bussy Saint-Georges
Tél: 01.60.37.55.37 - email : marnevallee@apave.com

B.E.T
23 rue Raspail - 94200 Ivry-sur-Seine
Tél: 01.49.87.04.90 - email : contact@epdc.fr

Docusign Envelope ID: 768CA9BC-72CD-4AB4-BAB7-6AD7892DDC2C

Liberté • Égalité • Fraternité
RÉPUBLIQUE FRANÇAISE

MINISTÈRE CHARGÉ DE LA CONSTRUCTION

Dossier spécifique permettant de vérifier la conformité des établissements recevant du public aux règles d'accessibilité et de sécurité contre l'incendie et la panique

Cette demande fait suite à un agenda d'accessibilité programmée (Ad'AP) approuvé : Oui ❑ Non ❑

(pièce PC39 et PC40 ou PA50 et PA51)

Article L. 111-8 et D.111-19-34 du code de la construction et de l'habitation

Cadres 1 à 3 informations nécessaires à l'instruction du dossier spécifique
Cadre 4 informations nécessaires à la vérification de la conformité aux règles de sécurité et d'accessibilité en application des articles R. 111-19-17 et R. 123-22 du code de la construction
Cadre 5 informations nécessaires à l'instruction des dérogations ou modalités particulières d'application des règles de sécurité ou d'accessibilité

Vous pouvez utiliser ce formulaire si :

- vous souhaitez construire, aménager ou modifier un établissement recevant de public
- vous souhaitez réaliser les travaux de mise en accessibilité d'un établissement recevant du public dans le cadre d'un agenda d'accessibilité programmée
- les travaux projetés sont soumis à un permis de construire ou un permis d'aménager

Ce dossier qui sera joint à la demande de permis (PC 39/PC 40 ou PA 50/PA 51) vous permet d'accomplir les formalités nécessaires

CADRE RÉSERVÉ À L'ADMINISTRATION

N° de l'autorisation

AT ⌊_⌋⌊_⌋⌊_⌋ ⌊_⌋⌊_⌋⌊_⌋ ⌊_⌋⌊_⌋ ⌊_⌋⌊_⌋⌊_⌋⌊_⌋⌊_⌋

Le cas échéant, n° de permis de construire ou d'aménager :

⌊_⌋⌊_⌋⌊_⌋ ⌊_⌋⌊_⌋⌊_⌋ ⌊_⌋⌊_⌋ ⌊_⌋⌊_⌋⌊_⌋⌊_⌋⌊_⌋ ⌊_⌋⌊_⌋

Date de dépôt en mairie : ⌊_⌋⌊_⌋ ⌊_⌋⌊_⌋ ⌊_⌋⌊_⌋⌊_⌋⌊_⌋

1- Identité du ou des demandeur(s)

Le demandeur indiqué dans le cadre ci-dessous sera le titulaire de la future autorisation
Si la demande est présentée par plusieurs personnes, indiquez leurs identités sur papier libre[1]

Vous êtes un particulier **Madame** ❑ **Monsieur** ❑

Nom : ..... Prénom : ..... Date de naissance : ⌊_⌋⌊_⌋ ⌊_⌋⌊_⌋ ⌊_⌋⌊_⌋⌊_⌋⌊_⌋

Vous êtes une personne morale

Raison sociale et dénomination : SCCV VILLEJUIF LEBON LAMARTINE FNO

N° Siret : ⌊_⌋⌊_⌋⌊_⌋ ⌊_⌋⌊_⌋⌊_⌋ ⌊_⌋⌊_⌋⌊_⌋ ⌊_⌋⌊_⌋⌊_⌋⌊_⌋⌊_⌋

Représentant de la personne morale : Madame ❑ **Monsieur** ☒

Nom : DAGUET Prénom : François Date de naissance à défaut de N° SIRET : ⌊_⌋⌊_⌋ ⌊_⌋⌊_⌋ ⌊_⌋⌊_⌋⌊_⌋⌊_⌋

2- Coordonnées du ou des demandeur(s) : Si la demande est présentée par plusieurs personnes, indiquez leurs coordonnées sur papier libre

Adresse Numéro : 121 Voie : avenue de Malakoff

Lieu-dit : ..... Localité : Paris

Code postal 75116⌊_⌋ BP ⌊_⌋⌊_⌋⌊_⌋ cedex ⌊_⌋⌊_⌋

Si le demandeur habite à l'étranger : Pays : ..... Division territoriale : .....

Téléphone fixe : ⌊_⌋⌊_⌋ ⌊_⌋⌊_⌋ ⌊_⌋⌊_⌋ ⌊_⌋⌊_⌋ ⌊_⌋⌊_⌋ **Portable :** ⌊_⌋⌊_⌋ ⌊_⌋⌊_⌋ ⌊_⌋⌊_⌋ ⌊_⌋⌊_⌋ ⌊_⌋⌊_⌋

Indicatif si pays étranger : ⌊_⌋⌊_⌋ ⌊_⌋⌊_⌋ Courriel : mleduc et agohard @ emerige.com

[1] Les décisions prises par l'administration seront notifiées au demandeur indiqué ci-dessus. Une copie des décisions concernant le dossier spécifique sera adressée aux autres demandeurs, lesquels seront co-titulaires de l'autorisation.

Docusign Envelope ID: 768CA9BC-72CD-4AB4-BAB7-6AD7892DDC2C

3 - Auteur du projet ou maître d'œuvre

Madame ❑ Monsieur ❑ Personne morale ❑

Nom : ..... Prénom : .....

Et/ou :

Raison sociale et dénomination de la personne morale, le cas échéant : A26

N° Siret : 79003164500035

Adresse Numéro : 165 Voie : rue de vaugirard

Lieu-dit : ..... Localité : PARIS

Code postal 75015 BP ... cedex ...

Si le maître d'œuvre habite à l'étranger/ Pays : Pays : ..... Division territoriale : .....

Téléphone fixe : 0970755280 **Téléphone portable :** ...

Indicatif si pays étranger : ... Courriel : ..... @ .....

❑ Je souhaite que les courriers de l'administration concernant le dossier spécifique (autres que les décisions) lui soient adressés

4 - Le projet

4.1 – Adresse du terrain

Nom de l'établissement : .....

Numéro : ..... Voie : RUE LAMARTINE

Lieu-dit : ..... Localité : VILLEJUIF

Code postal 94800 BP ... cedex ...

N° de section(s) cadastrale(s) : AV N° de parcelle (s) : 372

4.2 – Activité

AVANT TRAVAUX, le cas échéant :

Activité principale exercée dans l'établissement *(par étage(s))* :

.....

Activité(s) annexe(s) ou secondaire(s) *(par étage(s))* :

.....

Classement sécurité incendie de l'ERP :
(Catégorie et type d'exploitation en application de l'article R. 123-19 du code de la construction et de l'habitation)

.....

Identité de l'exploitant *(s'il est connu au moment du projet)* **:**

.....

APRÈS TRAVAUX :

Activité principale *(par étage(s))* **:**

1 ERP 5ème catégorie de type M et N

Activité(s) annexe(s) *(par étage(s))* :

.....

Proposition de classement sécurité incendie de l'ERP :
(Catégorie et type d'exploitation en application de l'article R. 123-19 du code de la construction et de l'habitation)

ERP de 5eme catégorie livré en coque brute faisant l'objet d'une demande d'aménagement ultérieur

Identité de l'exploitant *(s'il est connu au moment du projet)***:**

.....

Veuillez compléter sur papier libre, si nécessaire.

4.3 – Nature des travaux *(plusieurs cases possibles)*

☒ Construction neuve

☐ Travaux de mise en conformité totale aux règles d'accessibilité

☐ Extension

☐ Réhabilitation

☐ Travaux d'aménagement (remplacement de revêtements, rénovation électrique, création d'une rampe, par exemple)

☐ Création de volumes nouveaux dans des volumes existants (modification du cloisonnement, par exemple)

Surface de plancher avant travaux : ..... Surface de plancher après travaux : .....

☐ Modification des accès en façades

Le cas échéant,préciser si ces travaux mettent en œuvre des engagements d'un Ad 'AP déposé antérieurement.

☐ Oui : Ad'AP n° ☐☐☐ ☐☐☐ ☐☐☐☐ validé le : ☐☐ ☐☐ ☐☐☐☐

☐ Non

Cette demande fait l'objet d'une déclaration ou autorisation au titre du code de l'environnement (produits dangereux stockés ou utilisés) : Oui ☐ Non ☒

4.4 – Effectif

Maximum susceptible d'être admis même temporairement par niveau (suivant le calcul réglementaire défini par les règlements incendie) en indiquant les principaux locaux accessibles au public

	Types de locaux (activité/prestation)	Public	Personnel	TOTAL
Sous-sol				
Rez-de-chaussée	Type M et N	180	20	200
1er étage				
2e étage				
3e étage				
Effectif cumulé		180	20	200

Veuillez joindre une note annexe si le projet le nécessite (nombre d'étages supérieur à 3, présence d'une mezzanines, etc)

4.5 - Stationnement

Stationnement couvert ☒ Parcs de stationnement intégrés ☐ ou isolés ☐

	Avant réalisation du projet	Après réalisation du projet
Nombre de places de stationnement	0	0
Dont nombre de places réservées aux personnes handicapées	0	0

5 - Dérogations et/ou adaptations

5.1 – Dérogations

Ce projet comporte une demande de dérogation :

☐ Au titre de la sécurité incendie (Article R.123-13 du CCH) : Nombre de dérogations demandées : _____

Chaque demande doit faire l'objet d'une fiche détaillée rédigée sur papier libre indiquant notamment les règles auxquelles il est demandé de déroger (référence article et libellé), les éléments du projet auxquels elles s'appliquent (localisation sur les plans) et leur justification (motivation et mesures compensatoires proposées)

☐ Au titre de l'accessibilité (Article R. 111-19-10 du CCH) : Nombre de dérogations demandées : _____

Chaque demande doit faire l'objet d'une fiche détaillée rédigée sur papier libre indiquant notamment les règles auxquelles il est demandé de déroger (référence article et libellé), les éléments du projet auxquels elles s'appliquent (localisation sur les plans) et leur justification (motivation et mesures de substitution proposées pour les ERP exerçant une mission de service public)

5.2 – Modalités particulières d'application

☐ Le projet présente des contraintes liées à la structure du bâtiment qui justifient des modalités d'application particulières telles que définies par l'arrêté prévu à l'article R. 111-19-7 IV du Code de la construction et de l'habitation

(veuillez expliciter les adaptations prévues et les contraintes structurelles dont elles découlent)

Veuillez joindre une note annexe si le projet le nécessite

.....

.....

.....

.....

Docusign Envelope ID: 768CA9BC-72CD-4AB4-BAB7-6AD7892DDC2C

Si vous souhaitez vous opposer à ce que les informations nominatives comprises dans ce formulaire soient utilisées à des fins commerciales, cochez la case ci-contre : ❑

Si vous êtes un particulier : La loi n° 78 -17 du 6 janvier 1978 relative à l'informatique, aux fichiers et aux libertés, s'applique aux réponses contenues dans ce formulaire pour les personnes physiques. Elle garantit un droit d'accès aux données nominatives les concernant lorsqu'ils ne portent pas atteinte à la recherche d'infractions fiscales et la possibilité de rectification sous réserve des procédures prévues au code général des impôts et au Livre des procédures fiscales. Ces droits peuvent être exercés à la mairie. Les données recueillies seront transmises aux services compétents pour l'instruction de votre demande.

Délais et voies de recours : le délai de recours devant le tribunal administratif compétent est de deux mois à compter de la décision autorisant ou refusant l'autorisation ou, en cas de décision tacite, à compter de la date à laquelle la décision aurait dû être notifiée (dès lors que le dossier avait été complété). Le tribunal administratif peut être saisi par l'application informatique « Télérecours citoyens » accessible par le site internet https://www.telerecours.fr/

Docusign Envelope ID: 768CA9BC-72CD-4AB4-BAB7-6AD7892DDC2C

Liberté • Égalité • Fraternité
RÉPUBLIQUE FRANÇAISE

MINISTÈRE CHARGÉ
DE LA CONSTRUCTION

Bordereau de dépôt des pièces constituant le dossier spécifique

Veuillez cocher les cases correspondant aux pièces jointes à votre demande et reporter le numéro correspondant sur la pièce jointe.

L'attention du pétitionnaire est attirée sur le fait que la commission de sécurité et d'accessibilité pourra lui demander des pièces complémentaires si la compréhension du projet le nécessite.

Pièces	Numéro de la pièce	Nombre d'exemplaires à fournir
☒ Imprimé du dossier spécifique permettant de vérifier la conformité des établissements recevant du public aux règles d'accessibilité et de sécurité contre l'incendie et la panique	1	4
☒ Plan de situation	2	3

1 - Dossier destiné à la vérification de la conformité aux règles de sécurité incendie

(Art. R. 123-22 du code de la construction et de l'habitation (PC 40 ou PA 51))

Pièces	Numéro de la pièce	Nombre d'exemplaires à fournir
☒ Une notice récapitulant les dispositions prises pour satisfaire aux mesures prévues par le règlement de sécurité et notamment : • les matériaux utilisés pour le gros œuvre, la décoration et les aménagements intérieurs • la ou les solutions retenues pour l'évacuation des personnes de chaque niveau de la construction en tenant compte des différentes situations de handicap	3	3
☒ Un plan de situation, des plans de masse et de façades des constructions projetées faisant ressortir : • les conditions d'accessibilité des engins de secours • les largeurs des voies et les emplacements des baies d'intervention pompiers • la présence de tout bâtiment ou local occupé par des tiers	4	3
☒ Des plans de coupe et des plans de niveaux, ainsi qu'éventuellement ceux des planchers intermédiaires aménagées dans la hauteur comprise entre deux niveaux ou entre le dernier plancher et la toiture du bâtiment, faisant apparaître notamment : • les largeurs des passages affectés à la circulation du public tels que les dégagements, escaliers, sorties • la ou les solutions retenues pour l'évacuation des personnes de chaque niveau de la construction en tenant compte des différentes situations de handicap • les caractéristiques des éventuels espaces d'attente sécurisés	5	3
☐ La ou les demande(s) de dérogation(s) éventuelle(s), la ou les fiche(s) explicative(s) et tous les documents utiles à leur justification	6	3

N. B : *les documents de détail intéressant les installations techniques doivent pouvoir être fournis par le constructeur ou l'exploitant avant le début des travaux portant sur ces installations ; ils sont alors communiqués à la commission de sécurité*

2 - Dossier destiné à la vérification de la conformité aux règles d'accessibilité

(Arrêté du 11 septembre 2007 DEVU0763039A) (PC39 ou PA50)

Pièces	Numéro de la pièce	Nombre d'exemplaires à fournir
☒ Plans cotés dans les trois dimensions (longueur, largeur, hauteur) à une échelle adaptée précisant : • Les cheminements extérieurs (fonctions, largeurs, pentes, dévers, éclairage, solutions techniques pour assurer le guidage, le repérage, …) • Les raccordements (voirie / parties extérieures de l'établissement ; parties extérieures / parties intérieures du ou des bâtiments constituant l'établissement) • Les circuits destinés aux piétons et aux véhicules (liaison accès au terrain/voie interne/places de stationnement adaptées et réservées/circulations piétonnes/ entrée de l'établissement) • Les espaces de manœuvre, de retournement et de repos extérieurs • Les pentes des plans inclinés et les dévers de cheminement	7	3

Docusign Envelope ID: 768CA9BC-72CD-4AB4-BAB7-6AD7892DDC2C

☒	Plans cotés dans les trois dimensions (longueur, largeur, hauteur) à une échelle adaptée pour chaque niveau et pour chaque bâtiment précisant : • Les circulations intérieures horizontales et verticailes (fonctions, largeurs, pentes, dévers …) • Les aires de stationnement • Les locaux sanitaires destinés au public • Le sens d'ouverture des portes et leur espace de débattement • Les espaces d'usage, de manœuvre, de retournement et de repos intérieurs • L'emplacement des appareils sanitaires et leurs accessoires obligatoires • Les places de stationnement adaptées et réservées aux personnes handicapées et la mention du taux de ces places • Cas particuliers des ERP de 5e catégorie situés dans un cadre bâti existant et des IOP existantes : Délimitation de la partie de bâtiment accessible aux personnes handicapées et indications permettant de s'assurer que les prestations sont accessibles dans cette partie	8	3
☐	Plans avant travaux s'il s'agit d'un bâtiment existant	9	3
☒	Notice descriptive présentant les points suivants pour expliquer comment le projet prend en compte l'accessibilité (Art. R. 111-19-19 CCH) : • Dimensions des locaux ouverts aux usagers de l'établissement • Caractéristiques fonctionnelles et dimensionnelles des équipements techniques et des dispositifs de commande utilisables par le public • Nature et couleur des matériaux et revêtements de sols, murs et plafonds • Traitement acoustique des espaces • Dispositif d'éclairage des parties communes et, le cas échéant, niveaux d'éclairement et moyens éventuels d'extinction progressive des luminaires S'il s'agit d'un établissement ou d'une installation recevant du public assis : • Emplacements accessibles aux personnes handicapées en fauteuil roulant : nombre, taux par rapport au nombre total de places assises, localisation, cheminements permettant d'y accéder depuis l'entrée de l'établissement • Dans le cas d'un établissement recevant du public assis de plus de 1000 places, l'arrêté municipal fixant le nombre d'emplacements accessibles S'il s'agit d'un établissement disposant de locaux d'hébergement destinés au public • Nombre et caractéristiques des chambres, salles d'eau et cabinets d'aisance accessibles aux personnes handicapées : taux de ces chambres et locaux par rapport au nombre total de chambres, localisation, répartition par catégorie, le cas échéant S'il s'agit d'un établissement ou d'une installation comportant des cabines d'essayage, d'habillage ou de déshabillage ou des douches : • Nombre et caractéristiques des cabines et douches accessibles aux personnes handicapées S'il s'agit d'un établissement ou d'une installation comportant des caisses de paiement disposées en batterie • Nombre de caisses aménagées pour être accessibles aux personnes handicapées et leur localisation	10	3
☐	Dans le cas d'un parking de plus de 500 places, couvert ou non, dépendant d'un établissement recevant du public ou d'une installation ouverte au public : Arrêté municipal prévu à l'article 3 de l'arrêté du 1er août 2006 (NOR : SOCU0611478A) fixant le nombre de places de stationnement automobile adaptées et réservées	11	3
☐	La ou les demande(s) de dérogation(s) éventuelle(s), la ou les fiche(s) explicative(s) et tous les documents utiles à sa justification	12	3

Docusign Envelope ID: 768CA9BC-72CD-4AB4-BAB7-6AD7892DDC2C

VILLE DE VILLEJUIF - 94800

QUARTIER LEBON LAMARTINE

LOT FNO - FRANGE NORD OUEST

CONSTRUCTION DE 41 LOGEMENTS LLI-LLS ET 1 ERP DE 5ème CATEGORIE TYPE M ET N EN COQUE VIDE

PC39-10 : Notice accessibilité Commerce

Maîtrise d'ouvrage

EMERIGE RESIDENTIEL
121 94800 – 75116 PARIS

GRAND PARIS AMENAGEMENT
2 avenue Jean-Jaurès - 94600 Choisy-le-Roi

Maîtrise d'œuvre
A26BLM Architecture et Urbanisme
167, rue de Vaugirard
75015 Paris

- A26 BLM -
167 rue de Vaugirard-75015 PARIS
www.a26blm.eu - 01.45.67.09.02
SAS au capital de 33 100 €
NAF 7111Z-SIRET 410 007 249 00015
Ordre N°National S03534
TVA FR 67 410 007 249

Docusign Envelope ID: 768CA9BC-72CD-4AB4-BAB7-6AD7892DDC2C

1. Presentation

1.1. Objet du projet

La présente notice d'accessibilité – niveau PC- concerne la création d'un ERP de 5ème catégorie, type M et N implanté dans le LOT FNO - FRANGE NORD OUEST au rez-de-chaussée du Bâtiment A situé le long de la rue LAMARTINE.

1.2. Caracteristiques de l'etablissement

La surface commerciale utile est 264 m²

La surface dispose des accès au niveau de la rue Lamartine et de la rue Auguste Delaume
La surface commerciale objet de la présente notice sera implantée au rez-de-chaussée d'un immeuble à usage d'habitations.

La surface commerciale fera l'objet d'un dossier d'aménagement par le(s) preneur(s) pour avis de la commission de sécurité avant toute exploitation.

1.3. Classement

Le commerce est classé en 5ème catégorie, type M et N.

2. Réglementations applicables

- Code de la construction et de l'habitation, article R162-8 à R162-13
- Code de l'urbanisme ;
- Arrêté du 23 juin 1978 relatif aux installations de chauffage ;
- Arrêté du 20 avril 2017 relatif à l'accessibilité aux personnes handicapées des ERP lors de leur construction

3. Descriptif sommaire des travaux

Le local « commerce », sera livré étanche, brut de gros œuvre en béton et fluides en attentes,

Les vitrines et les menuiseries extérieures seront à la charge du preneur et devront respecter la façade du présent permis.

Le reste des aménagements seront à la charge du preneur.

Il appartiendra au futur preneur de déposer auprès des autorités compétentes le dossier des aménagements interieur à réaliser. La présente notice vise simplement à rappeler les principales dispositions réglementaires applicables à l'établissement de par son classement.

Docusign Envelope ID: 768CA9BC-72CD-4AB4-BAB7-6AD7892DDC2C

4. Dispositions prévues

Dans le cadre des travaux d'aménagement, les dispositions suivantes en matière d'accessibilité pour les personnes en situation de handicap devront être appliquées. Le ou les futurs preneurs devront, lors du dossier d'aménagement du commerce, confirmer ou infirmer certaines dispositions décrites ci-dessous.

Dispositions relatives à l'accès de l'établissement

Caracteristiques

- Le cheminement extérieur sera horizontal et sans ressaut. Les plans inclinés pour rejoindre le bâtiment depuis la voie publique, lorsqu'ils ne peuvent pas être évités, auront une pente inférieure à 5% et comporteront des paliers de repos en haut et en bas. La distance entre les paliers de repos, pour une pente inférieure à 5%, sera au maximum de 10m ;
- Un ressaut inférieur à bord arrondi ou muni d'un chanfrein inférieur à 2 cm sera toléré pour franchir une des portes d'éntrée ;
- La largeur minimale du cheminement permettant d'accéder à l'établissement sera au moins égale à 1,40 mètre libre de tout obstacle ;
- Un espace de manœuvre avec possibilité de demi-tour (gabarit rond de 1m50) sera réalisé en chaque point du cheminement où un choix d'itinéraire est donné à l'usager, ainsi que devant les portes d'entrée de l'établissement desservies par un cheminement accessible (longueur de l'espace de manœuvre : supérieure à 1m70 lorsque porte poussée ; supérieure à 2m20 lorsque porte tirée);
- La nature du sol devra être non meuble, non glissante et non réfléchissante et sans obstacle à la roue.
- Lorsque le cheminement accessible croise un itinéraire emprunté par des véhicules, il comportera un élément permettant l'éveil de la vigilance des piétons au droit de ce croisement. Un marquage au sol et une signalisation indiqueront aux conducteurs des véhicules qu'ils croisent un cheminement pour piétons ;
- Le cheminement sera éclairé (valeur d'éclairement mesurée au sol supérieure ou égale à 20 lux).

Pour ce projet, l'ensemble des dispositions précitées sera réalisé.
L'accès à ce commerce se fait depuis rue Lamartine et de la rue Auguste Delaume
Les altimètries des planchers des commerces seront adaptées.

Dispositions relatives au stationnement automobile (article 3)

Aucune place de stationnement PMR sera attribuée au commerce.
aucune places de stationnement seront aménagées au RDC et Sous-sol de l'immeuble pour l'ensemble des commerces.
99 places de stationnement seront aménagées sur deux niveaux.
Parmi elles, 78 places seront dédiées aux tours 1 et 27 du quartier Lebon Lamartine, et 21 places au lot FNO, réparties comme suit :

Docusign Envelope ID: 768CA9BC-72CD-4AB4-BAB7-6AD7892DDC2C

– RDC : 33 places pour les tours dont 5 places PMR ;
– Sous-sol -1 : 45 places pour les tours et 21 places pour le lot FNO dont 2 places PMR.

Dispositions relatives aux accès à l'établissement (article 4)

L'accès à l'établissement est libre et en continuité avec le cheminement extérieur.

- Les entrées de l'établissement seront facilement repérables par des éléments architecturaux ou par un traitement utilisant des matériaux différents ou visuellement contrastés ;
  - un fléchage et/ou une indication sera mise en place à partir de la voie publique pour diriger les PMR vers ces accès ;
  - un système de contrôle d'accès ou de communication adapté et répondant aux dispositions réglementaires pourra être mis en place ponctuellement ;
  - le système d'ouverture des portes sera utilisable en position debout comme en position assise.

Disposition relatives à l'accueil du public (article 5)

A la charge du preneur dans sa demande d'autorisation d'aménagement.

Dispositions relatives aux circulations intérieures horizontales (article 6)

(Ces dispositions seront détaillées dans le dossier d'aménagement déposé par l'exploitant).

Dispositions relatives aux circulations intérieures verticales (article 7)

Sans objet

Dispositions relatives aux revetements des sols, murs et plafonds (article 9)

(Ces dispositions seront détaillées dans le dossier d'aménagement déposé par l'exploitant).

Dispositions relatives aux portes et SAS (article 10)

Concernant les portes extérieures (enveloppe de la coque):

Toutes les portes permettront le passage des personnes handicapées et devront pouvoir être manoeuvrées par des personnes ayant des capacités physiques réduites ;

Les portes situées sur le cheminement emprunté par le public auront une largeur minimale de vantail de 0m90 (avec passage libre de plus de 0m83 lorsque la porte est ouverte à 90 degrés). Des espaces de manœuvre de porte seront aménagés au droit des portes éventuelles desservant des locaux accessibles au public (longueur de l'espace de manœuvre : supérieure à 1m70 lorsque porte poussée ; supérieure à 2m20 lorsque porte tirée).

L'effort nécessaire pour ouvrir une porte sera inférieur ou égale à 50 N ;

Docusign Envelope ID: 768CA9BC-72CD-4AB4-BAB7-6AD7892DDC2C

Les portes comportant une partie vitrée importante seront repérables - ouvertes comme fermées - à l'aide d'éléments visuels contrastés par rapport à l'environnement immédiat.

Concernant les portes intérieures :

Ces dispositions seront détaillées dans le dossier d'aménagement déposé par l'exploitant.

Dispositions relatives aux sanitaires (article 12)

S'agissant des aménagements intérieurs, une demande préalable ou un permis de construire sera déposée ultérieurement par des futurs exploitants.

Dispositions relatives aux sorties (article 13)

Les sorties devront pouvoir être aisement repérées, atteintes et utilisées par les personnes handicapées.

L'évacuation des Personnes en Situation de Handicap se fera directement sur l'extérieur au rez-de-chaussée.

Alarme : Le signal sonore doit être complété par un dispositif destiné à rendre l'alarme perceptible en tenant compte de la spécificité des locaux et des différentes situations de handicap des personnes amenées à fréquenter l'établissement.

(Ces dispositions seront détaillées dans le dossier d'aménagement déposé par l'exploitant).

Dispositions relatives à l'éclairage (article 14)

La qualité de l'éclairage, artificiel ou naturel, des circulations intérieures sera telle que l'ensemble du cheminement sera traité sans créer de gêne visuelle. A cette fin, le dispositif d'éclairage artificiel mis en œuvre répondra aux dispositions suivantes :

- Il permet d'assurer des valeurs minimales d'éclairement mesurées au sol d'au moins : 200 lux au droit des postes d'accueil, 100 lux en tout point des circulations intérieures horizontales ; (Ces dispositions seront détaillées dans le dossier d'aménagement déposé par l'exploitant).
- La mise en œuvre des points lumineux permettra d'éviter tout effet d'éblouissement direct des usagers en position « debout » comme « assis » ou de reflet sur la signalétique.

(Ces dispositions seront détaillées dans le dossier d'aménagement déposé par l'exploitant).

Docusign Envelope ID: 768CA9BC-72CD-4AB4-BAB7-6AD7892DDC2C

Maîtrise d'Ouvrage

SCCV VILLEJUIF
LEBON LAMARTINE
FNE-FNO

121 Avenue de Malakoff 75116 Paris

Signed by:
François Daguet
B6701235FCC444D...

Rue LAMARTINE

PROJET A26 BLM

PROJET QUARTIER LEBON LAMARTINE

PC- FRANGE NORD OUEST- LEBON LAMARTINE

Titre

Dossier spécifique - règles d'accessibilité aux personnes handicapées.

N°

PC39

Date	Réf	Echelle
Mars 2026	**3881**	ECH :

Indice	Date	Modifications

- A26 BLM -
167 rue de Vaugirard-75015 PARIS
www.a26blm.eu - 01.45.67.09.02
SAS au capital de 33 100 €
NAF 7111Z-SIRET 410 007 249 00015
Ordre N°National S03534
TVA FR 67 410 007 249

Maîtrise d'Oeuvre

Architectes-Urbanistes
Agence certifiée ISO 9001 - ISO 14001

167, rue de VAUGIRARD - 75015 PARIS
Tél: 01.45.67.09.02 - email : contact-blm@a26.eu

Architectes-Paysagistes
11 rue Beauregard -75002 Paris
Tél: 01.53.26.77.32 - email : agence@compagniedupaysage.fr

Infrastructures et Construction France
10 place Fulgence Bienvenue- 77600 Bussy Saint-Georges
Tél: 01.60.37.55.37 - email : marnevallee@apave.com


B.E.T
23 rue Raspail - 94200 Ivry-sur-Seine
Tél: 01.49.87.04.90 - email : contact@epdc.fr

Docusign Envelope ID: 768CA9BC-72CD-4AB4-BAB7-6AD7892DDC2C




Maitre d'oeuvre : A26 BUILDING HARMONY	Maitre d'ouvrage :	PROJET A26 BLM	Accessibilité PMR - Plans de situation		**PC39.2**
		PC- FRANGE NORD OUEST- LEBON LAMARTINE	Date : Mars 2026	1/2000	**3881**

Docusign Envelope ID: 768CA9BC-72CD-4AB4-BAB7-6AD7892DDC2C

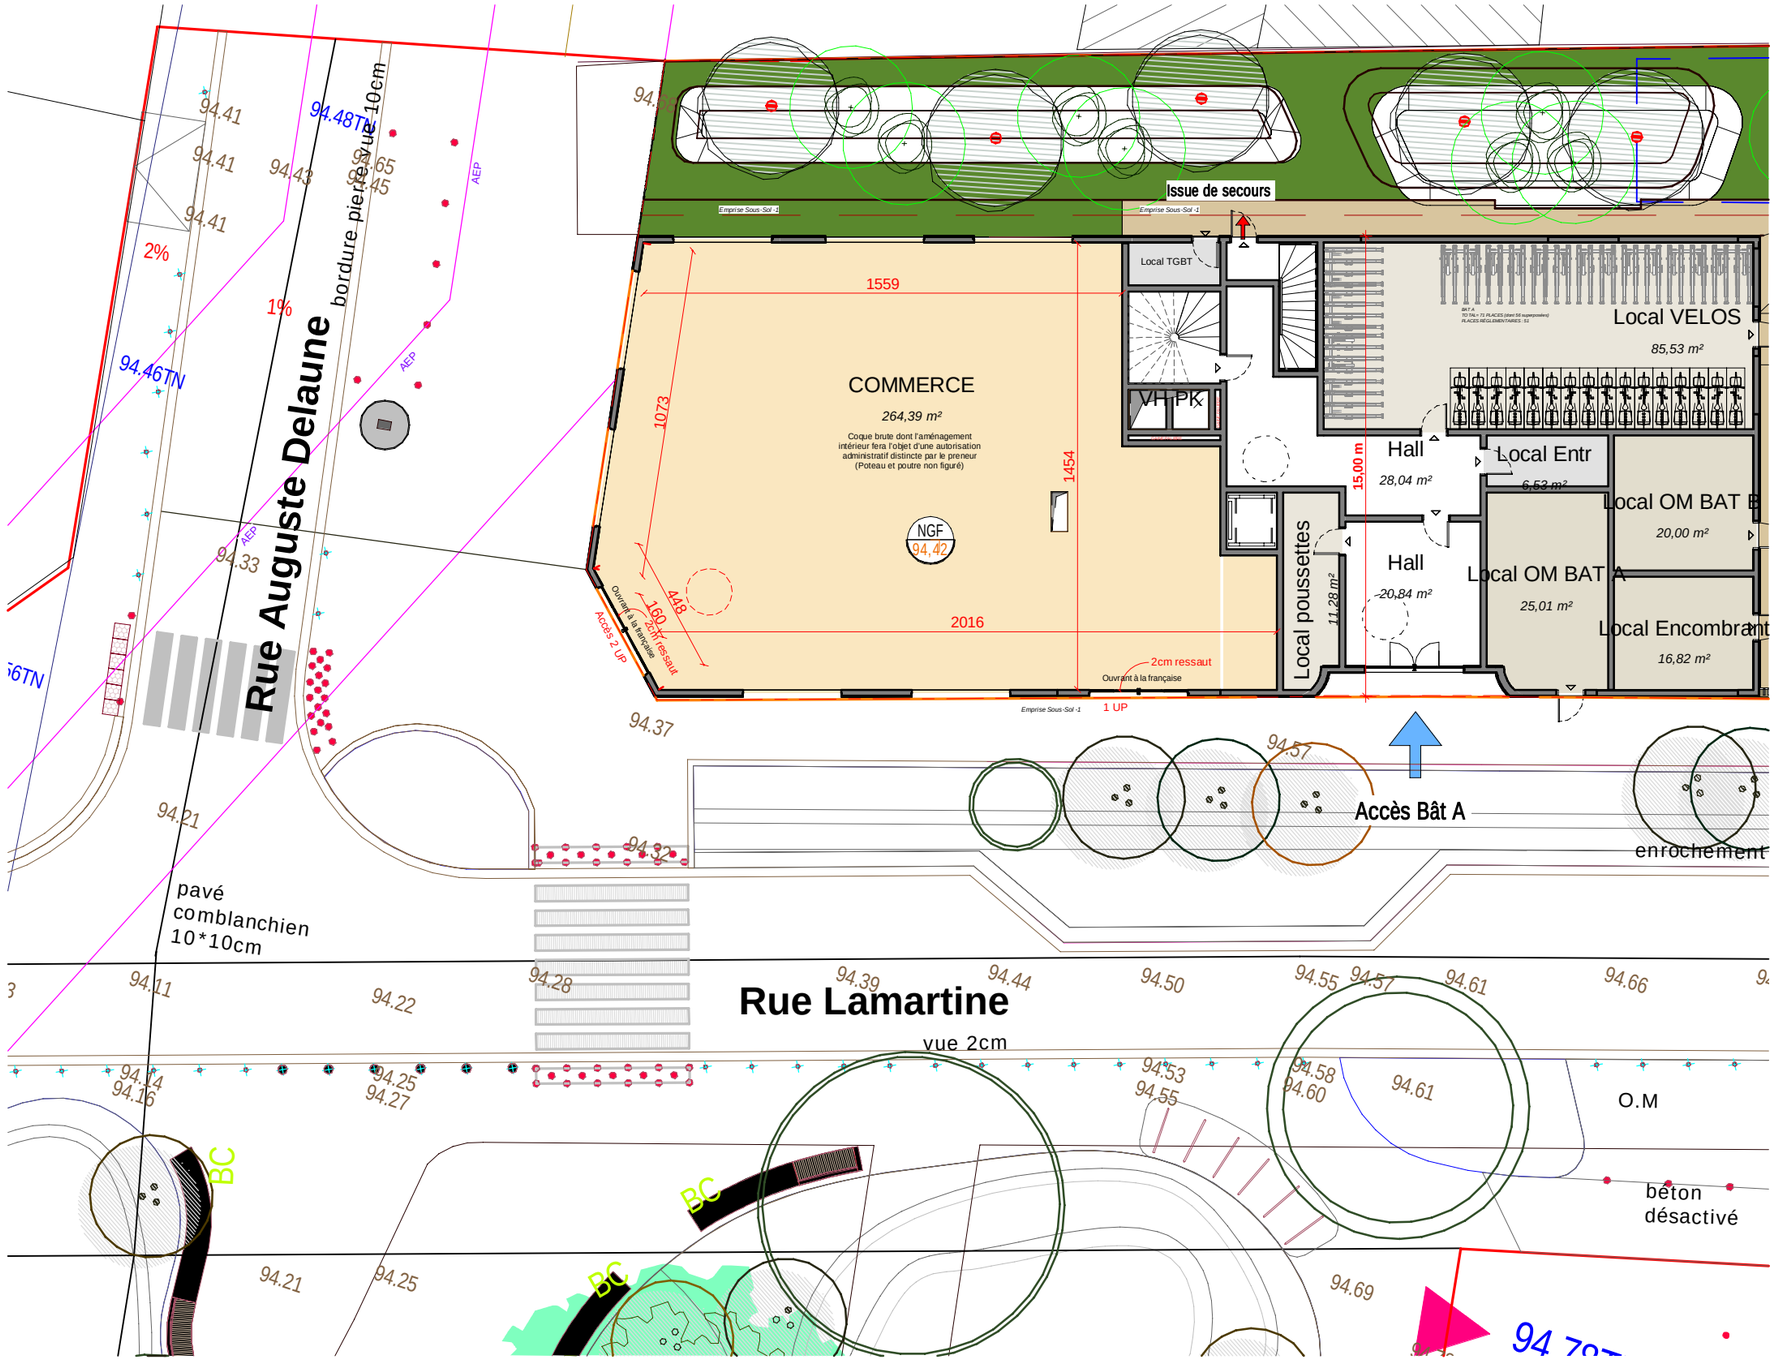

Maitre d'oeuvre : A26 BUILDING HARMONY	Maitre d'ouvrage :	PROJET A26 BLM	Accessibilité PMR - Plan du RDC coté dans les trois dimmensions - EXTERIEUR		**PC39.7**
		PC- FRANGE NORD OUEST- LEBON LAMARTINE	Date : Mars 2026	Ech : 1 : 200	**3881**

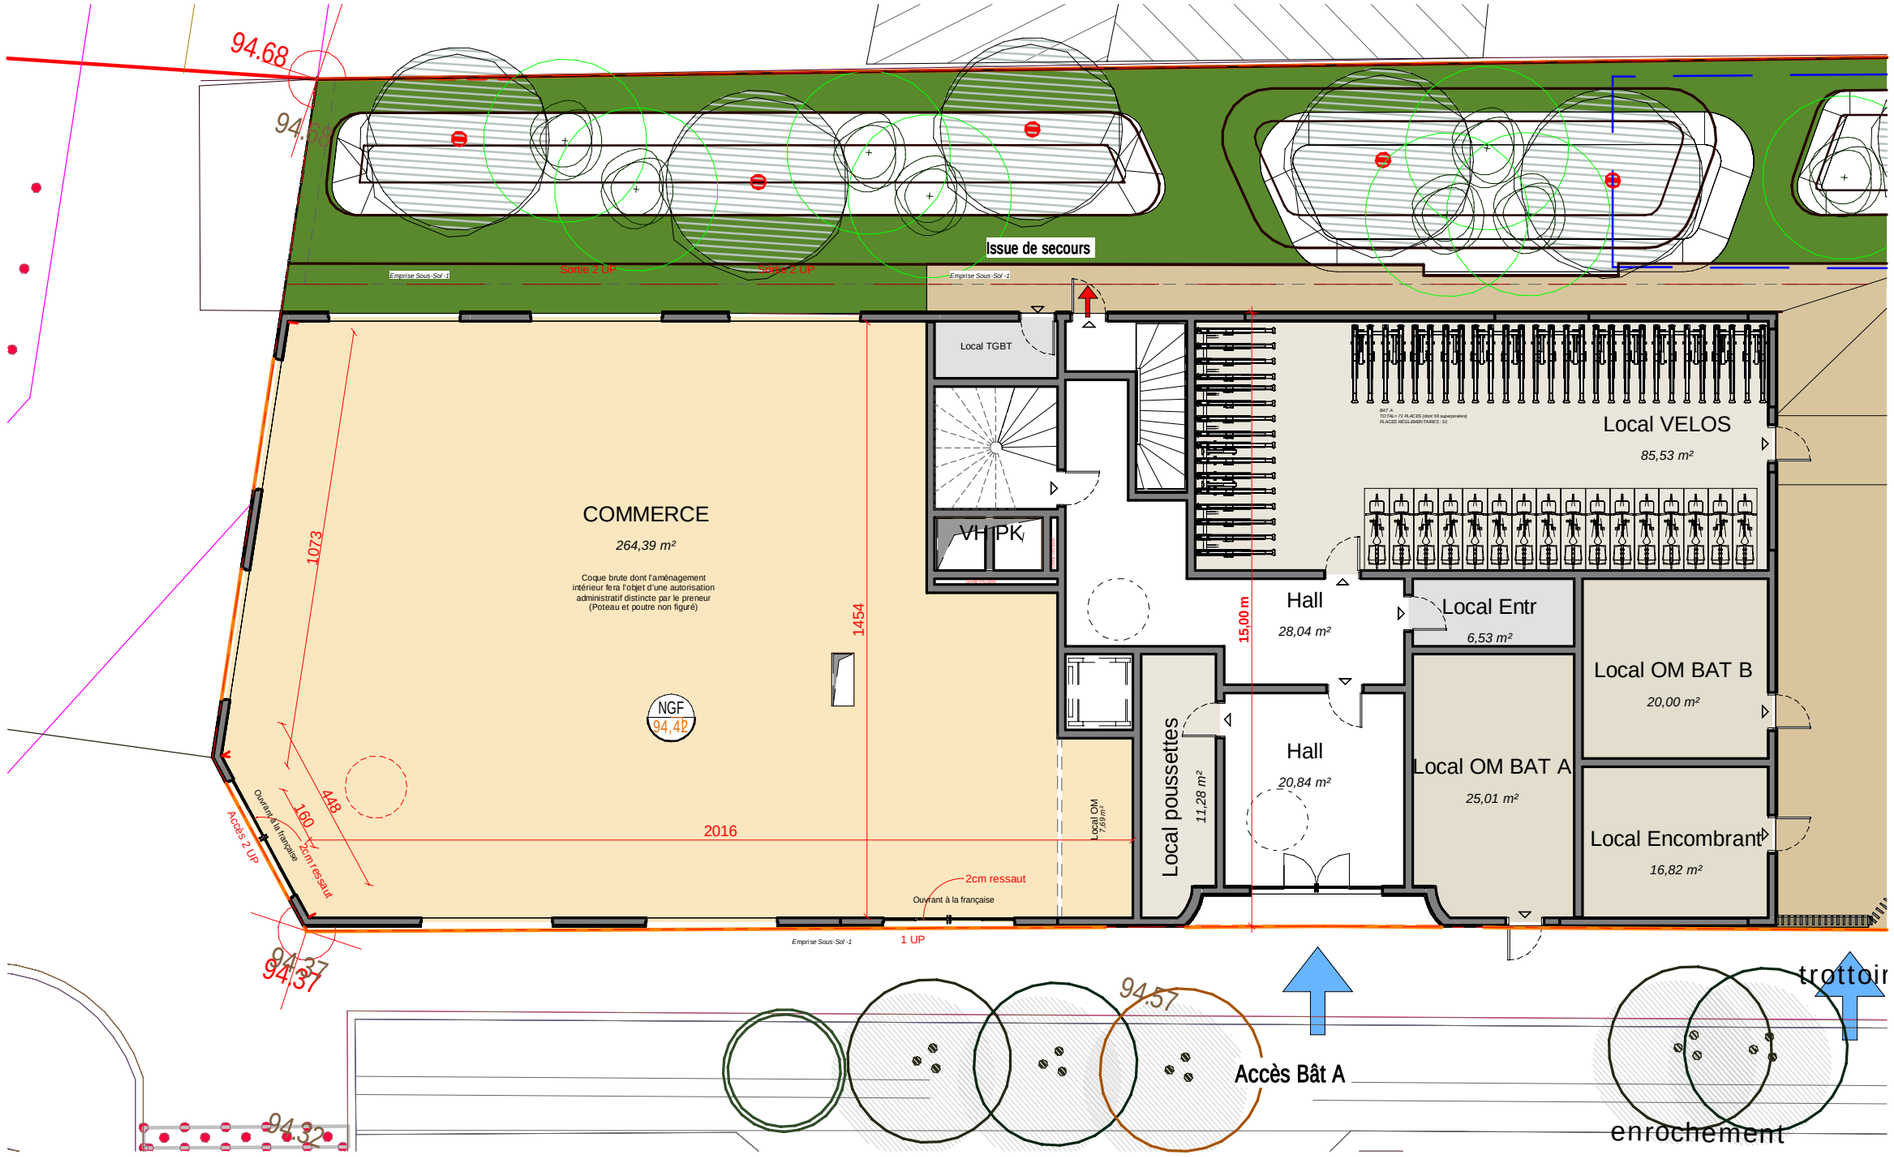

Maitre d'oeuvre : A26 BUILDING HARMONY	Maitre d'ouvrage :	PROJET A26 BLM	Accessibilité PMR - Plan du RDC coté dans les trois dimmensions - INTERIEUR		**PC39.8**
		PC- FRANGE NORD OUEST- LEBON LAMARTINE	Date : Mars 2026	Ech : 1 : 150	**3881**

Docusign Envelope ID: 768CA9BC-72CD-4AB4-BAB7-6AD7892DDC2C

VILLE DE VILLEJUIF - 94800

QUARTIER LEBON LAMARTINE

LOT FNO - FRANGE NORD OUEST

CONSTRUCTION DE 41 LOGEMENTS LLI-LLS ET 1 ERP DE 5ème CATEGORIE TYPE M ET N EN COQUE VIDE

PC40.3 : Notice de sécurité incendie Commerce

Maîtrise d'ouvrage

EMERIGE RESIDENTIEL
121 avenue de Malakoff – 75116 PARIS

GRAND PARIS AMENAGEMENT
2 avenue Jean-Jaurès - 94600 Choisy-le-Roi

Maîtrise d'œuvre
A26BLM Architecture et Urbanisme
167, rue de Vaugirard
75015 Paris

- A26 BLM -
167 rue de Vaugirard-75015 PARIS
www.a26blm.eu - 01.45.67.09.02
SAS au capital de 33 100 €
NAF 7111Z-SIRET 410 007 249 00015
Ordre N°National S03534
TVA FR 67 410 007 249

Docusign Envelope ID: 768CA9BC-72CD-4AB4-BAB7-6AD7892DDC2C

SOMMAIRE

1 GENERALITES....3

1.1 OBJET....3

1.2 TEXTES....3

2 ERP – LOCAL COMMERCIAL....4

2.1 BRANCHEMENT....5

2.2 ACCES DES SECOURS....5

2.3 ISOLEMENT PAR RAPPORT AUX TIERS....5

2.4 RESISTANCE AU FEU DES STRUCTURES ET PLANCHERS....6

2.5 FAÇADES....6

2.6 DÉGAGEMENTS....6

2.7 EVACUATION DES PERSONNES HANDICAPEES....7

2.8 AMÉNAGEMENTS INTERIEURS....7

2.9 DESENFUMAGE :....7

2.10 INSTALLATIONS ELECTRIQUES, ÉCLAIRAGE, CHAUFFAGE, PLOMBERIE, VENTILLATION, GRANDES CUISINES, ASCENSEURS, PROTECTION INCENDIE, SYSTÈME DE SÉCURITÉ INCENDIE :....7

Docusign Envelope ID: 768CA9BC-72CD-4AB4-BAB7-6AD7892DDC2C

1 GENERALITES

1.1 OBJET

La présente notice de sécurité incendie concerne la réalisation d'un ERP de 5ème catégorie, type M et N livré en coque vide.

Le commerce 1 est implanté au rez-de-chaussée d'un immeuble à usage d'habitation (bâtiment A du projet).

Ce commerce de 264 m² de surface au sol est destiné à être un ERP de 5e catégorie Type M et N. Il appartiendra à l'aménageur de la coque vide de prévoir une activité et une surface mise à disposition du public permettant de rester en 5e catégorie (futur dossier à déposer).

Le bâtiment A, en LLS, est classé en habitation collective de 3ème Famille A

Il fait partie du projet d'un ensemble immobilier de 2 bâtiments dont le bâtiment B est classé en intermédiaire de 2ème Famille. Le terrain se situe sur les parcelles cadastrales AV 265-372 le long de la rue Lamartine à Villejuif 94076

L'ensemble de l'opération comporte :

- Le bâtiment A avec des logements comprenant 1 cage :
  - Cage 1 comportant 26 logements d'habitation en R+4+A,
  - 1 ERP à rez-de-chaussée : commerce (objet de la présente notice.)

- Le bâtiment B avec des logements comprenant 3 escaliers extérieures :
  - comportant 15 logements d'habitation en R+2

- Un local sous-station en sous-sol -1 ;
  - 1 pour l'ensemble des logements des Bâtiments A et B

- Un niveau du RDC du Bâtiment B à usage de parc de stationnement destiné aux tours 1 et 27 du Quartier LEBON LAMARTINE, non accessible aux résidentes du projet, et comportant : 33 places pour les tours dont 5 places PMR ;
  au niveau du sous-sol -1 : 45 places pour les tours et 21 places pour le lot FNO dont 2 places PMR.

1.2 TEXTES

- Arrêté du 31 Janvier 1986, modifié par l'Arrêté du 19 Juin 2015 et l'Arrêté du 07 Août 2019,
- Règlement sanitaire départemental,
- Code de l'urbanisme (art. R111-2 et R111-4),

Docusign Envelope ID: 768CA9BC-72CD-4AB4-BAB7-6AD7892DDC2C

- Code de la construction et de l'habitation (art. R143-1 à R143-47),
- Arrêté du 25 juin 1980 modifié portant application des dispositions générales applicables aux établissements recevant du public,
- Arrêté du 22 Juin 1990 : dispositions complétant le règlement de sécurité ERP (5ème catégorie),
- Arrêté du 04 novembre 1975 et instruction du 1er décembre 1976 portant réglementation de l'utilisation de certains matériaux et produits dans les établissements recevant du public,
- Arrêté du 23 juin 1978 relatif aux installations fixes de chauffage,
- Décret n°2010-1016 du 30 août 2010 relatif aux obligations de l'employeur pour l'utilisation des installations électriques des lieux de travail.
- Décret n° 2010-1017 du 30 août 2010 relatif aux obligations des maîtres d'ouvrage entreprenant la construction ou l'aménagement de bâtiments destinés à recevoir des travailleurs en matière de conception et de réalisation des installations électriques
- Arrêté du 10 septembre 1970 relatif à la classification des façades vitrées par rapport au danger d'incendie,
- Arrêté du 10 septembre 1970 relatif à la classification des couvertures en matériaux combustibles par rapport au danger d'incendie résultant d'un feu extérieur,
- Arrêté du 30 juin 1983 portant classification des matériaux de construction et d'aménagement selon leur réaction au feu,
- Arrêté du 22 mars 2004 relatif à la résistance au feu des produits, éléments de construction et d'ouvrages.
- Arrêté du 23 février 2018 et des guides du CNPG applicables
- Arrêté du 13 juillet 2000 modifié portant règlement de sécurité de la distribution de gaz combustible par canalisations
- Instructions techniques n°246 relatives au désenfumage du 22 mars 2004.
- Instruction technique n°249 relatives aux façades.

2 ERP – LOCAL COMMERCIAL

Le commerce sera livré non-aménagé et il appartiendra au futur preneur de déposer auprès des autorités compétentes le dossier des aménagements projetés (en application de l'article R.425-15 du Code de l'Urbanisme reproduit ci-dessous).

Article R425-15

> *Lorsque le projet porte sur un établissement recevant du public, le permis de construire tient lieu de l'autorisation prévue par l'article L. 122-3 du code de la*

Docusign Envelope ID: 768CA9BC-72CD-4AB4-BAB7-6AD7892DDC2C

construction et de l'habitation dès lors que la décision a fait l'objet d'un accord de l'autorité compétente.

Le permis de construire indique, lorsque l'aménagement intérieur de l'établissement recevant du public ou d'une partie de celui-ci n'est pas connu lors du dépôt de la demande, qu'une autorisation complémentaire au seul titre de l'article L. 122-3 du code de la construction et de l'habitation devra être demandée et obtenue avant son ouverture au public en ce qui concerne l'aménagement intérieur du bâtiment ou de la partie de bâtiment concernée.

La coque sera livrée étanche (respect du coupe-feu et du clos et couvert), brute de gros œuvre en béton et les fluides seront en attente.

Les vitrines et les menuiseries extérieures seront à la charge du preneur et devront respecter la façade du présent permis.

Le reste des installations et aménagements ainsi que les notices de sécurité et accessibilité PMR seront à la charge du preneur.

2.1 BRANCHEMENT

- Les branchements concessionnaires ; eau, électricité, fibre… en attente dans le local. Pour l'électricité avec pose de coffret en façade ou directement raccordé sur le transfo de l'opération et comptage dans le commerce
- Les attentes eaux usées et eaux vannes bouchonnées
- Les gaines nécessaires au passage des futurs conduits de l'ERP (ventilation, désenfumage, hottes …) seront créées dans la traversée des logements des étages supérieurs et restitueront le coupe-feu exigible vis-à-vis des tiers (coupe-feu 1 heure).

  (Ces dispositions seront détaillées dans le dossier d'aménagement déposé par l'exploitant).

2.2 ISSUS DE SECOURS

- Le commerce est situé rez-de-chaussée et accessible de plain-pied.
- L'accès au commerce est possible directement à l'angle de la rue : Lamartine et Auguste Delaune
- Le commerce se trouve desservi par la voie publique (Lamartine) formant voie échelle. L'entrée du commerce est raccordée à la voie publique par un cheminement de plus de 1m80 de largeur (sans marches ni pente de plus de 10%).

Ces dispositions seront détaillées dans le dossier d'aménagement déposé par l'exploitant).

2.3 ISOLEMENT PAR RAPPORT AUX TIERS

Le commerce sera un ERP indépendant avec ses propres installations techniques.

Docusign Envelope ID: 768CA9BC-72CD-4AB4-BAB7-6AD7892DDC2C

Il sera isolé des tiers (logements) selon les dispositions de l'article PE6 du règlement de sécurité.

L'isolement vis-à-vis des logements adjacents sera établit par des murs et planchers coupe-feu 1 heure (REI 60).

Il n'y a pas de débord de couverture de l'ERP vis-à-vis de la façade du bâtiment d'habitation.

Les tiers en vis-à-vis sont distants de plus de 5 mètres.

Le parc de stationnement placé au R-1 sera isolé par un plancher CF 2 h. Aucune intercommunication n'existe entre le commerce et le parc de stationnement ;

Les conduits des logements traversant l'ERP seront traités coupe-feu 1h quel que soit leur diamètre.

Les conduits de l'ERP traversant le parking seront traités coupe-feu 2 heures quel que soit leur diamètre.

(Ces dispositions seront détaillées dans le dossier d'aménagement déposé par l'exploitant).

2.4 RESISTANCE AU FEU DES STRUCTURES ET PLANCHERS

La construction de l'ensemble du programme sera en béton armé, porteurs béton, voiles et planchers, assurant une stabilité et un coupe-feu 1 h au moins. Les commerces concernés occupent le RDC de ce programme et de ce fait leur enveloppe répondra à la Stabilité et à la tenue au feu de l'ensemble du programme.

(Ces dispositions seront détaillées dans le dossier d'aménagement déposé par l'exploitant).

2.5 FAÇADES

Pas de dispositions particulières en 5e catégorie.

2.6 DÉGAGEMENTS

Les sorties de secours du commerce sur l'extérieur sont réparties de la façon suivante :

- 1 porte coulissante automatique de 2 UP sur la rue Henri Lamartine
- 1 porte coulissante automatique de 1UP et distante de plus de 5 m.

Les sorties du commerce sur l'extérieur (2 issues totalisant 3 UP) sont dimensionnées pour un effectif de < 200 personnes.

(Ces dispositions seront détaillées dans le dossier d'aménagement déposé par l'exploitant).

La distribution intérieure au sein du commerce sera décrite dans le dossier d'aménagement du futur preneur selon l'article R.425-15 du Code de l'Urbanisme.

Docusign Envelope ID: 768CA9BC-72CD-4AB4-BAB7-6AD7892DDC2C

(Ces dispositions seront détaillées dans le dossier d'aménagement déposé par l'exploitant).

2.7 EVACUATION DES PERSONNES HANDICAPEES

A la charge du preneur à l'intérieur de l'établissement.

Au RDC les issues donnent de plain-pied sur l'extérieur.

Le cheminement extérieur respectera les dispositions réglementaires du point de vue de l'accessibilité des handicapés et permettra à ces derniers de quitter l'établissement en toute autonomie (pentes inférieures à 5%, ressauts inférieurs à 2cm, éclairage de 20 lux minimum …)

(Ces dispositions seront détaillées dans le dossier d'aménagement déposé par l'exploitant).

2.8 AMÉNAGEMENTS INTERIEURS

Les isolants thermiques intérieurs éventuels à mettre en œuvre respecteront les dispositions de l'article AM8 et du « Guide d'emploi des isolants combustibles dans les établissements recevant du public » (arrêté du 6 octobre 2004)

Les autres aménagements intérieurs mis en œuvre seront décrits dans le dossier d'aménagement du futur preneur selon l'article R.425-15 du Code de l'Urbanisme.

(Ces dispositions seront détaillées dans le dossier d'aménagement déposé par l'exploitant).

2.9 DESENFUMAGE :

Sans Objet (locaux non aveugles de moins de 300 m²)

2.10 INSTALLATIONS ELECTRIQUES, ÉCLAIRAGE, CHAUFFAGE, PLOMBERIE, VENTILLATION, GRANDES CUISINES, ASCENSEURS, PROTECTION INCENDIE, SYSTÈME DE SÉCURITÉ INCENDIE :

Les conduits non-aérauliques (évacuations diverses, conduites d'eau …) des logements traversant les ERP disposeront de manchon coupe-feu 1h ou seront encoffrés coupe-feu 1H quel que soit leur diamètre. Ce coupe-feu sera porté à 2 heures pour les réseaux transitant dans le parc de stationnement.

Les réseaux aérauliques tiers seront isolés coupe-feu 1 heures par encoffrement ou flocage dans la traversée de l'ERP. Ce coupe-feu sera porté à 2 heures pour les réseaux provenant du parc de stationnement.

(Ces dispositions seront détaillées dans le dossier d'aménagement déposé par l'exploitant).

Docusign Envelope ID: 768CA9BC-72CD-4AB4-BAB7-6AD7892DDC2C

Maîtrise d'Ouvrage

SCCV VILLEJUIF
LEBON LAMARTINE
FNE-FNO

121 Avenue de Malakoff 75116 Paris

Signed by:
François Daguet
B6701235FCC444D...

Rue LAMARTINE

PROJET A26 BLM

PROJET QUARTIER LEBON LAMARTINE

PC- FRANGE NORD OUEST- LEBON LAMARTINE

Titre		N°
Dossier spécifique - règles de sécurité		**PC40**
Date: Mars 2026	Réf: **3881**	Echelle: ECH :

Indice	Date	Modifications

- A26 BLM -
167 rue de Vaugirard-75015 PARIS
www.a26blm.eu - 01.45.67.09.02
SAS au capital de 33 100 €
NAF 7111Z-SIRET 410 007 249 00015
Ordre N°National S03534
TVA FR 67 410 007 249

Maîtrise d'Oeuvre

Architectes-Urbanistes
Agence certifiée ISO 9001 - ISO 14001


167, rue de VAUGIRARD - 75015 PARIS
Tél: 01.45.67.09.02 - email : contact-blm@a26.eu


Architectes-Paysagistes
11 rue Beauregard -75002 Paris
Tél: 01.53.26.77.32 - email : agence@compagniedupaysage.fr

Infrastructures et Construction France
10 place Fulgence Bienvenue- 77600 Bussy Saint-Georges
Tél: 01.60.37.55.37 - email : marnevallee@apave.com

B.E.T
23 rue Raspail - 94200 Ivry-sur-Seine
Tél: 01.49.87.04.90 - email : contact@epdc.fr

Docusign Envelope ID: 768CA9BC-72CD-4AB4-BAB7-6AD7892DDC2C

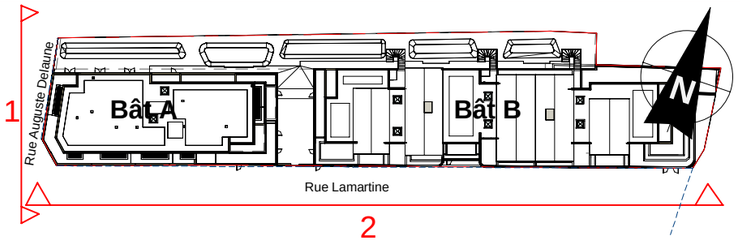

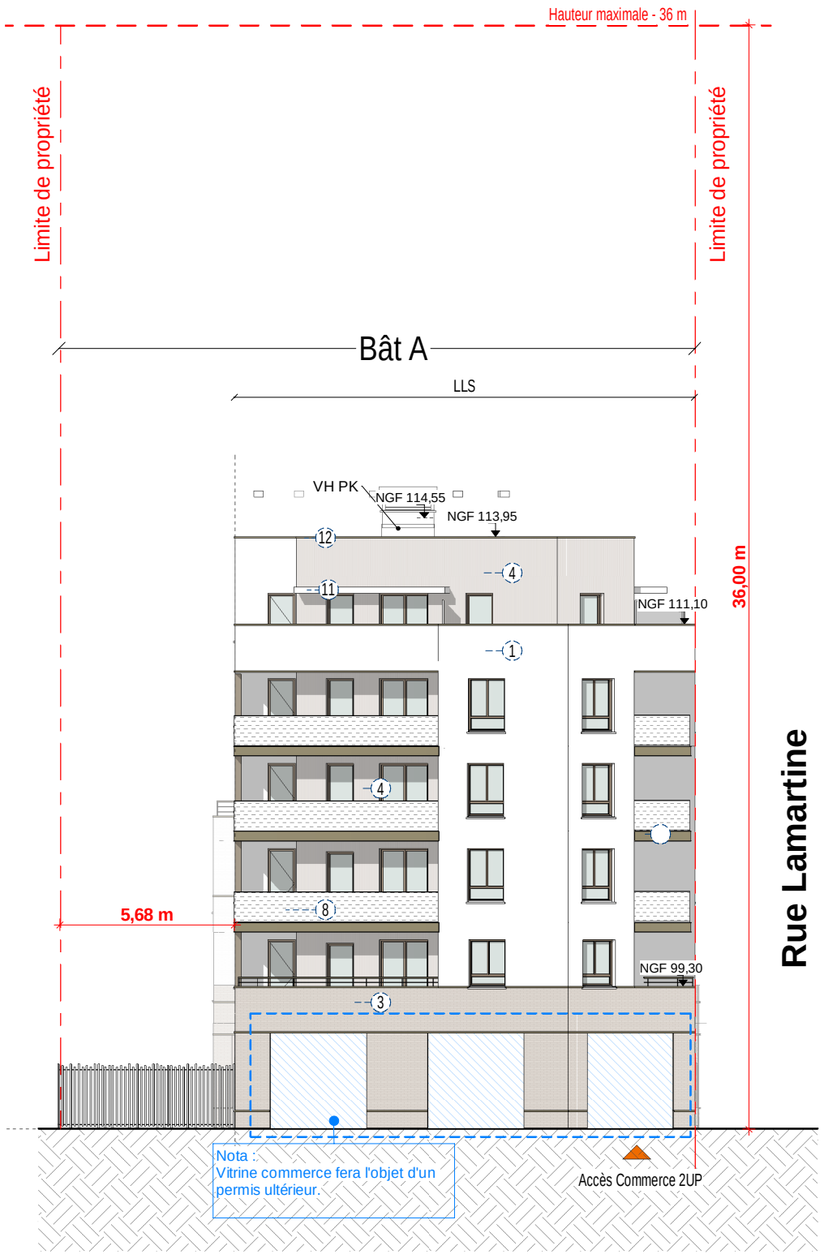


1. Façade Ouest-Rue Lamartine
Echelle : 1 : 200ème



2. PC40-4b - Bâtiment A - Façade SUD_Rue Lamartine
Echelle : 1 : 200ème

0 4m 8m

Maitre d'oeuvre :	Maitre d'ouvrage :	PROJET A26 BLM	Accessibilité PMR - Plan de façades		**PC40.4a-b**
		PC- FRANGE NORD OUEST- LEBON LAMARTINE	Date : Mars 2026	1/200	**3881**

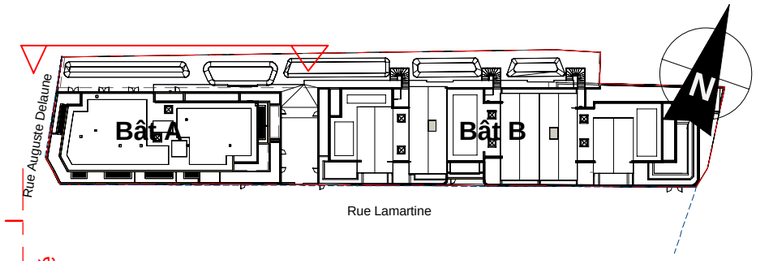




1. PC40-4c - Bâtiment A - Façade Nord sur jardin

Echelle : 1 : 200ème

0 4m 8m

Maitre d'oeuvre : A26 BUILDING HARMONY	Maitre d'ouvrage :	PROJET A26 BLM	Accessibilité PMR - Plan de façades		**PC40.4c**
		PC- FRANGE NORD OUEST- LEBON LAMARTINE	Date : Mars 2026	1/200	**3881**

Docusign Envelope ID: 768CA9BC-72CD-4AB4-BAB7-6AD7892DDC2C

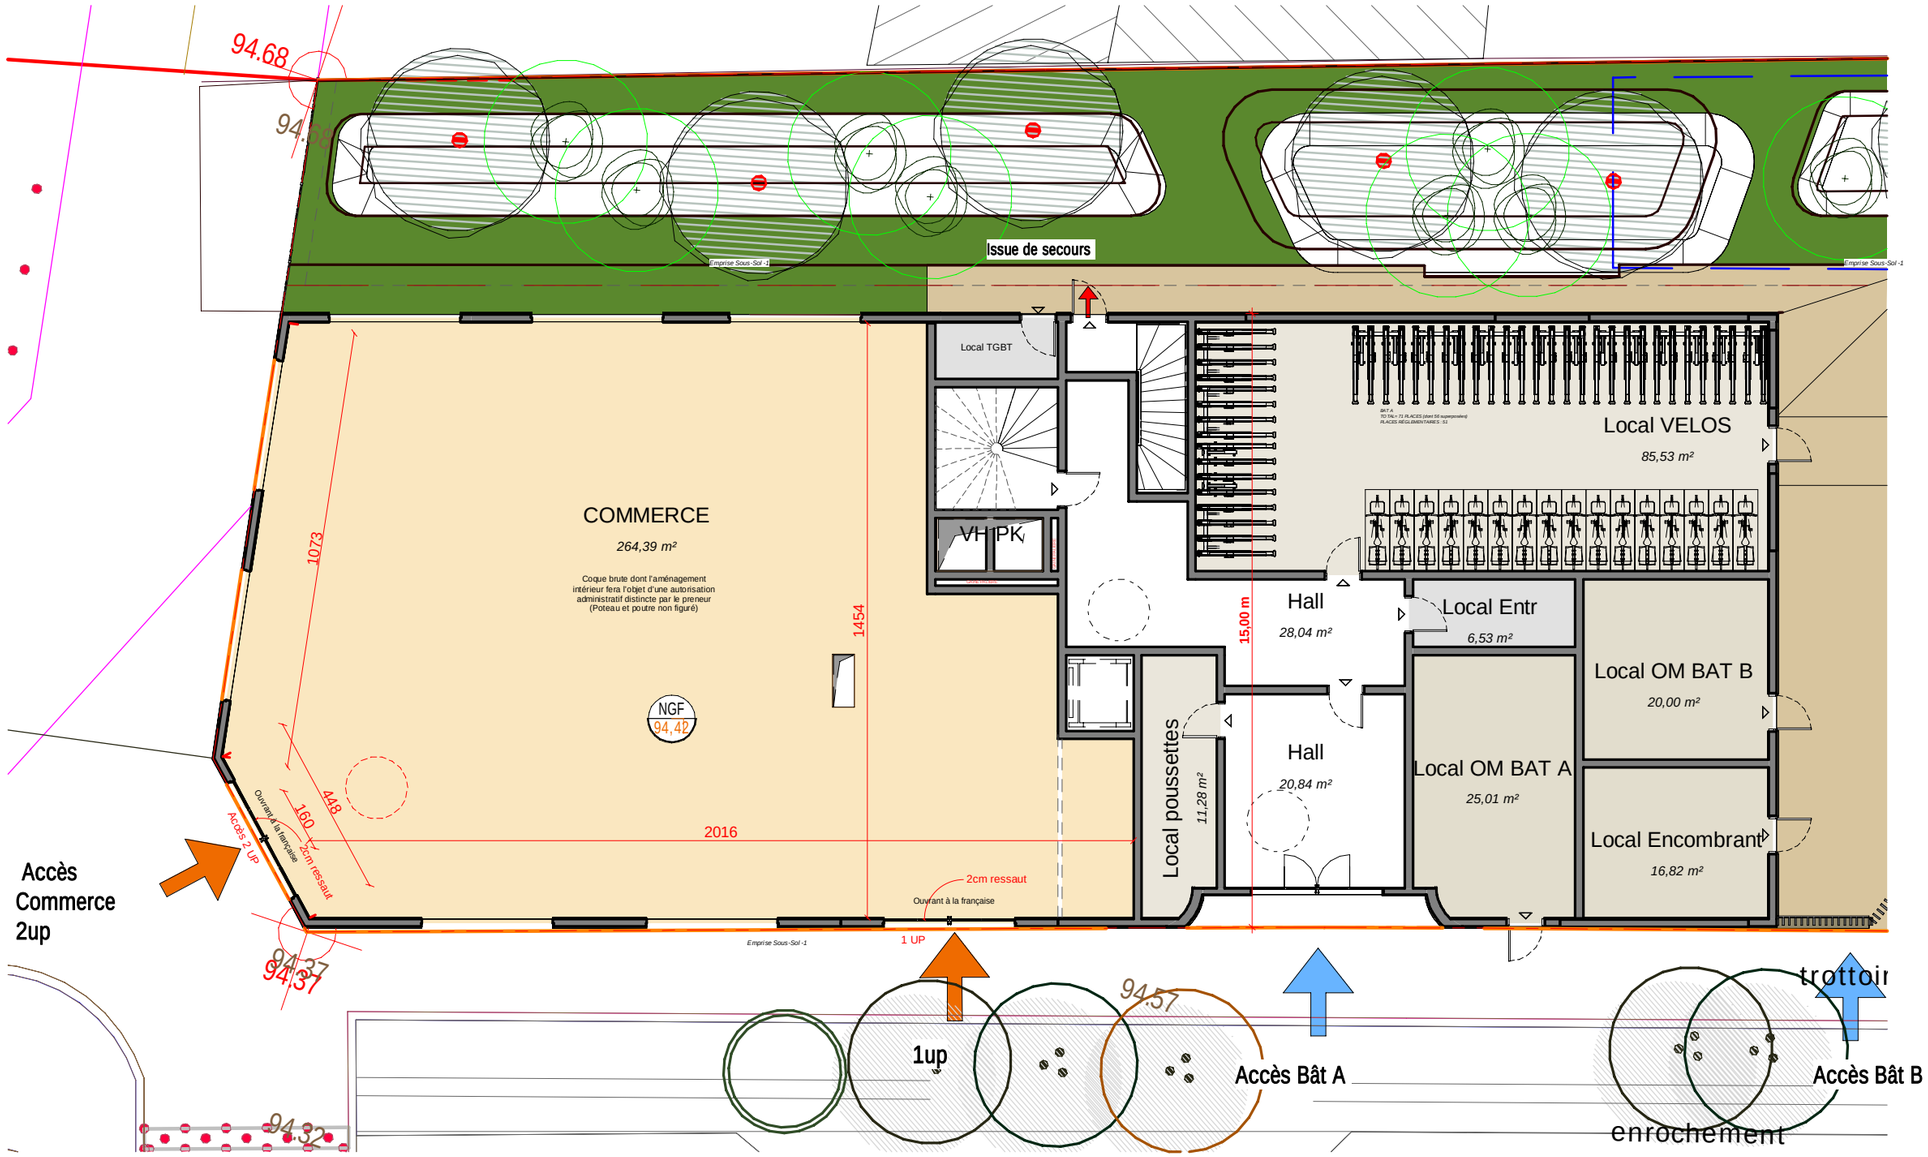

Maitre d'oeuvre : A26 BUILDING HARMONY	Maitre d'ouvrage :	PROJET A26 BLM	Sécurité Incendie - Plan de RDC - Bâtiment A		**PC40.5**
		PC- FRANGE NORD OUEST- LEBON LAMARTINE	Date : Mars 2026	Ech : 1 : 150	**3881**