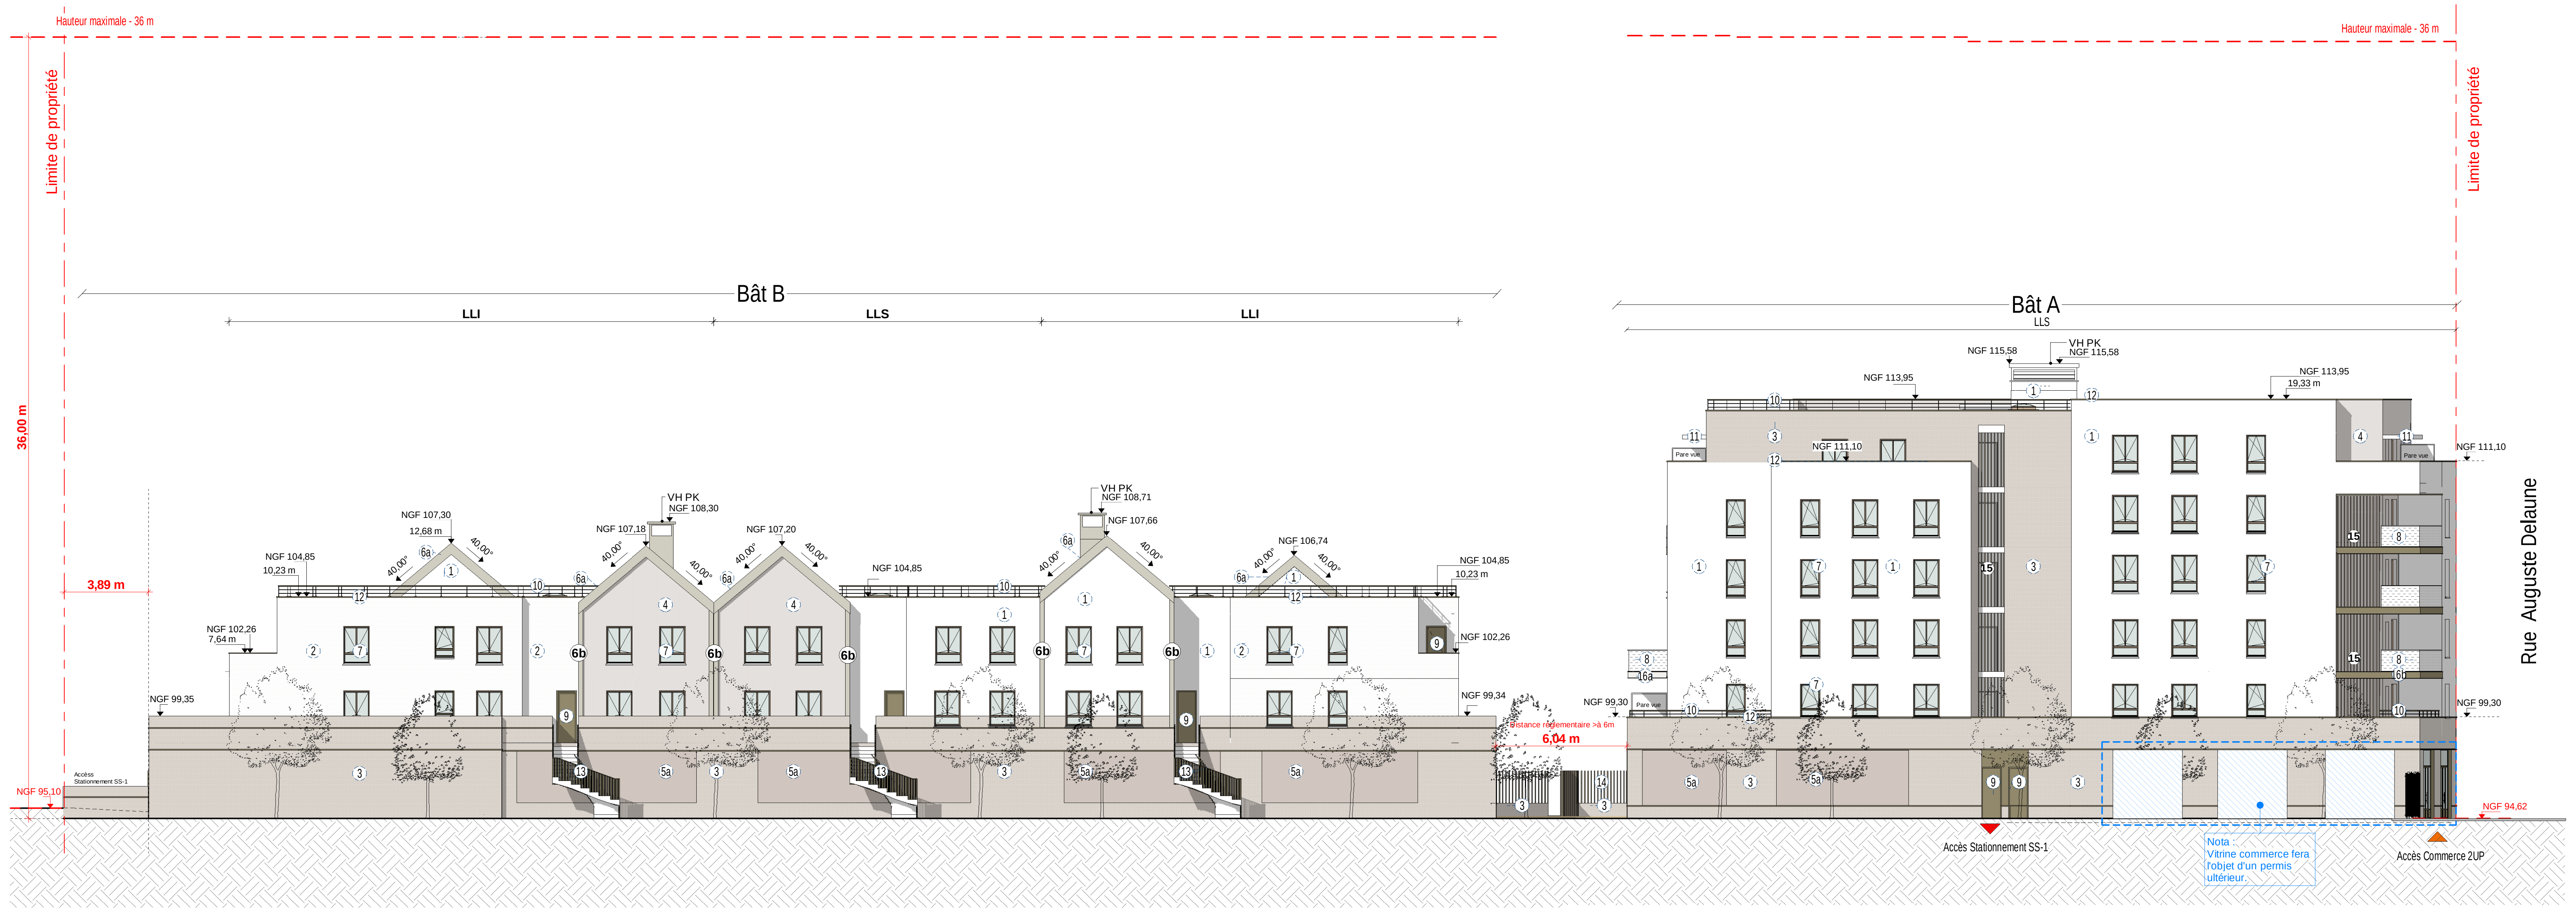

1. Façade Nord

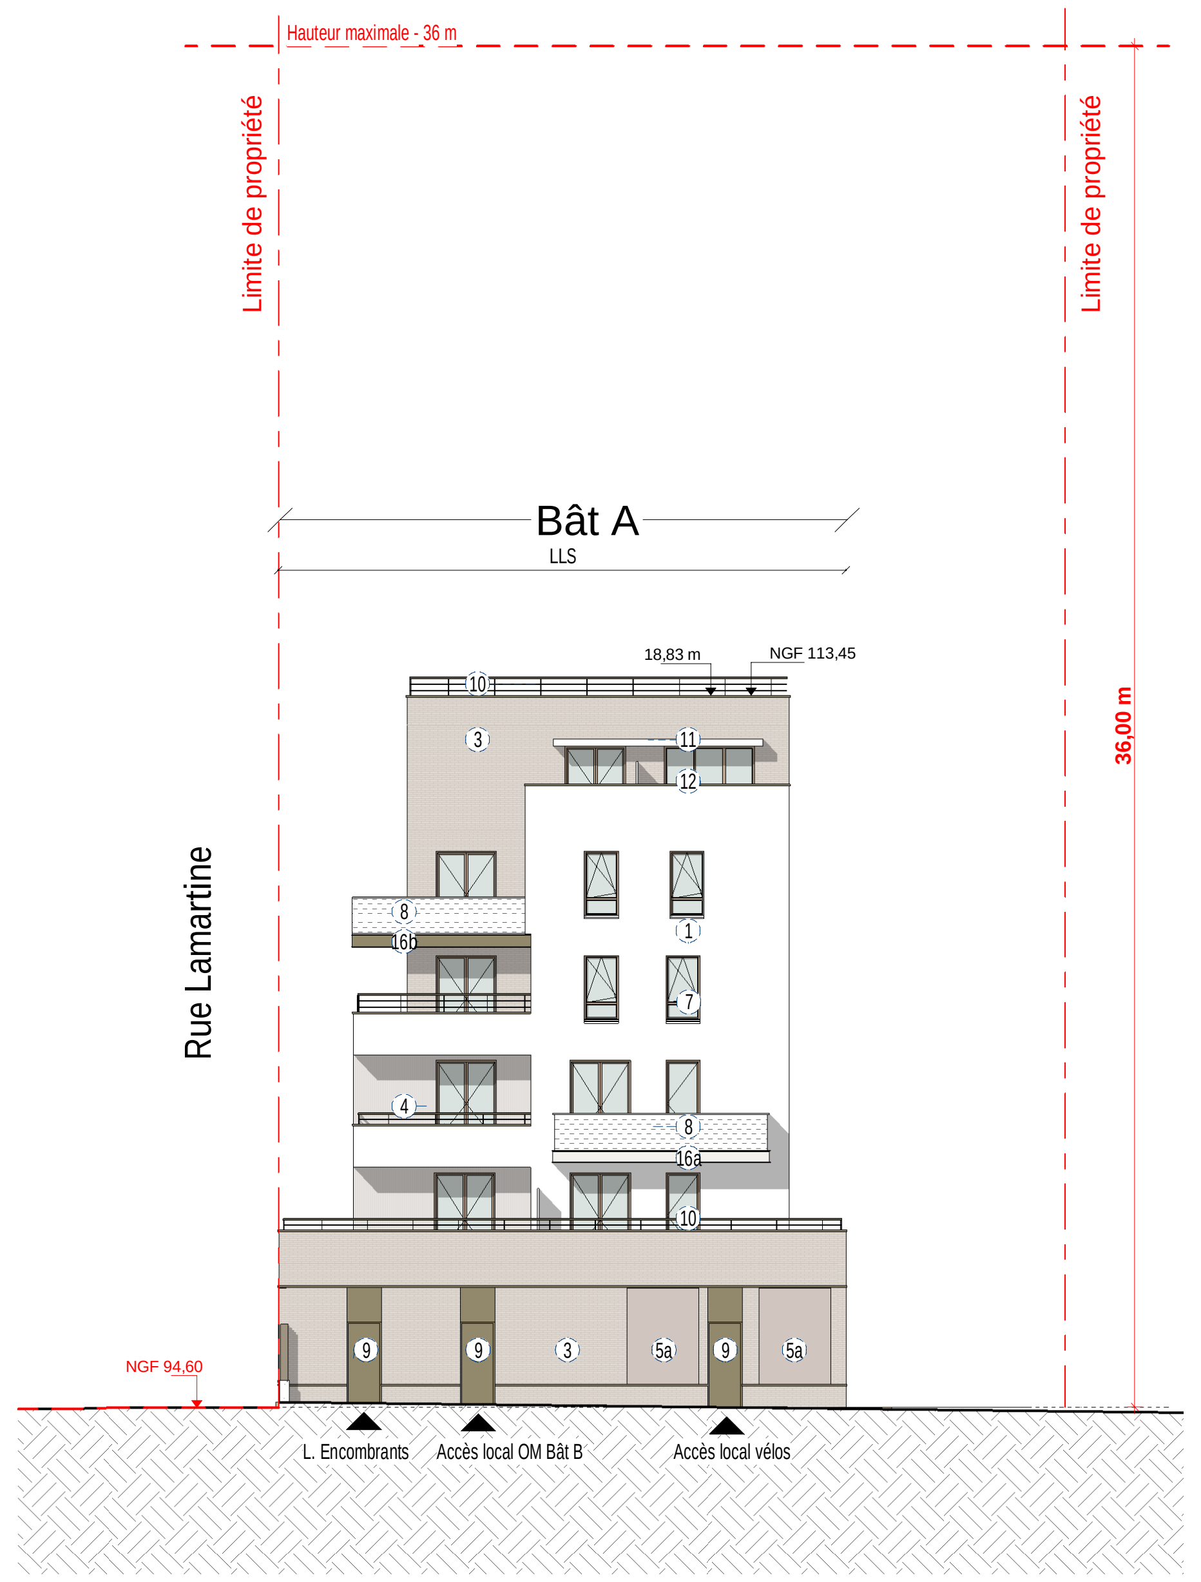

2. Façade Est Bât A
Echelle : 1 : 200ème

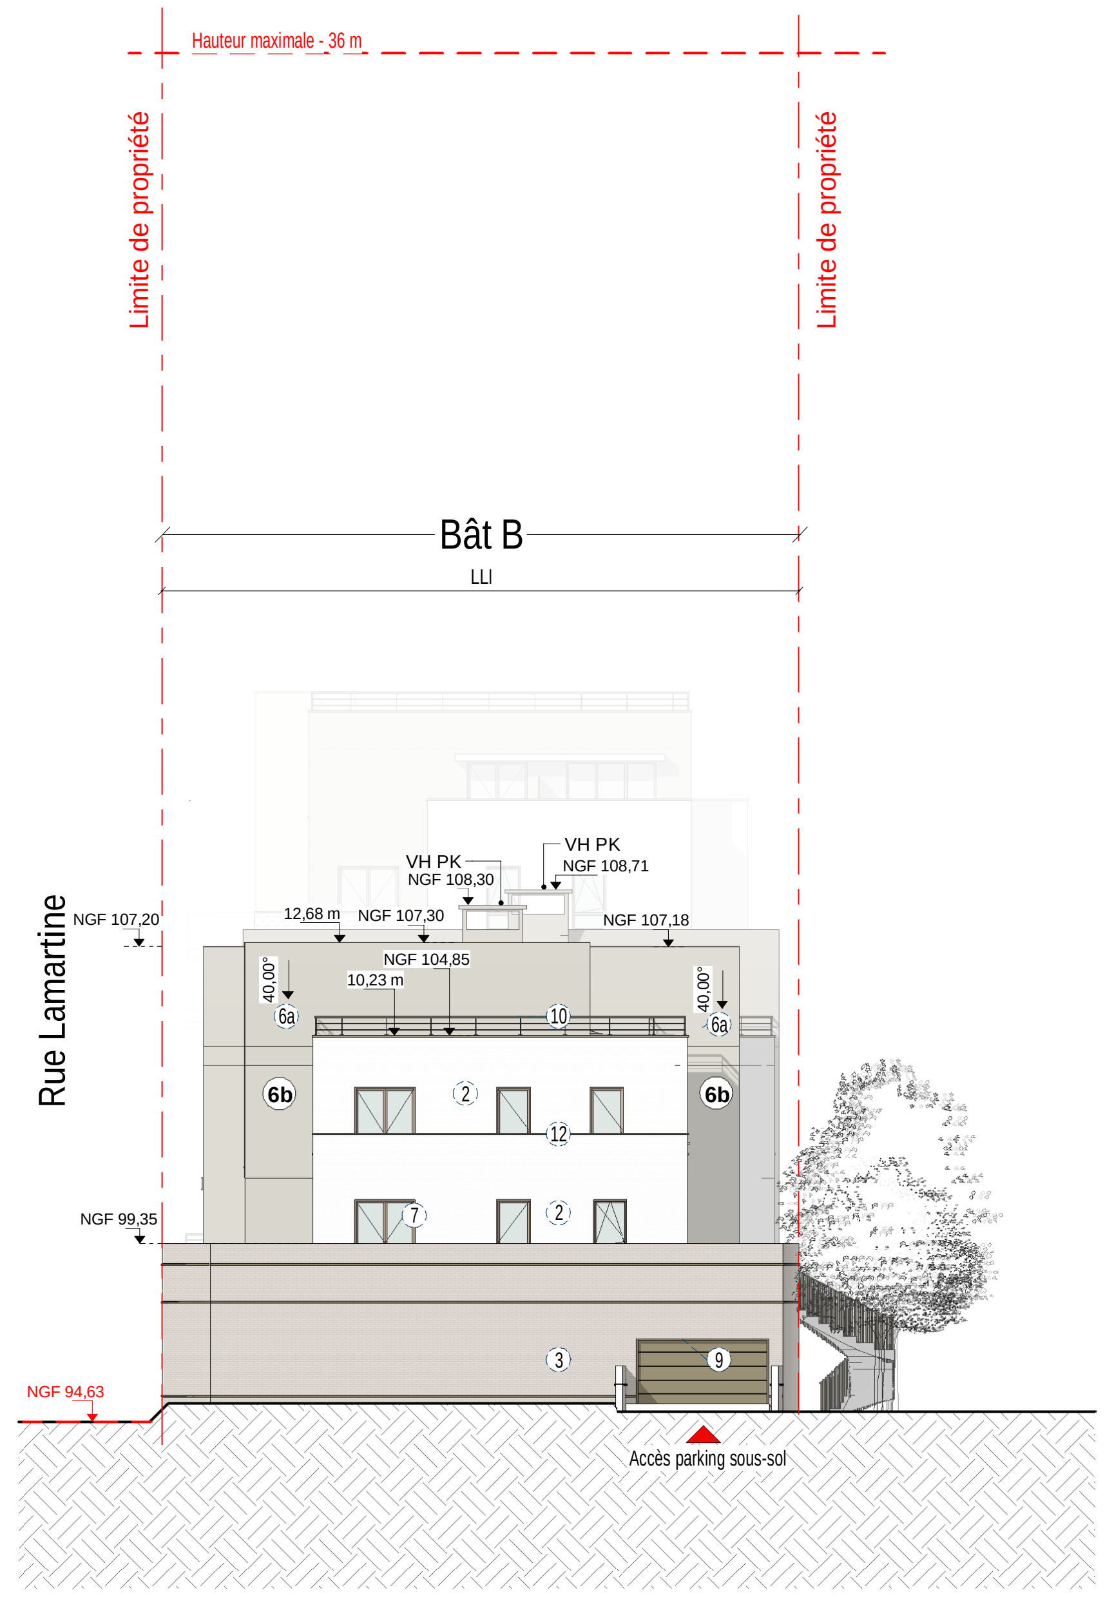

3. Façade Est Bât B
Echelle : 1 : 200ème

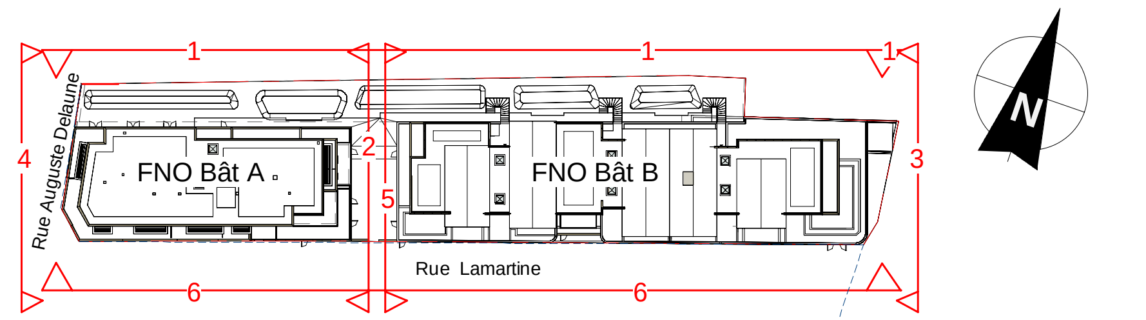

Légende matériaux :

- 1 Enduit blanc
- 2 Briquette de parement teinte blanche
- 3 Briquette de parement teinte beige clair
- 4 Enduit peigné teinte taupe foncé
- 5a Briquette de parement aspect Moucharabieh teinte beige clair
- 5b Briquette de parement aspect Moucharabieh teinte blanche
- 6a Toiture métallique PLX ou équivalent teinte beige foncé
- 6b Bardage vertical métallique PLX ou équivalent teinte beige foncé
- 6c Rive de toiture métallique PLX ou équivalent teinte blanche
- 7 Menuiseries bois
- 8 Garde corps teinte beige clair
- 9 Porte métallique teinte taupe foncé
- 10 Lisse de garde corps teinte taupe foncé
- 11 Casquette béton enduit teinte taupe foncé
- 12 Couvertine métallique teinte taupe clair
- 13 Main courante escalier métallique teinte beige clair
- 14 Clôture métallique teinte taupe foncé
- 15 Ventelles métalliques verticales teinte taupe foncé
- 16a Bord de dalles peint en teinte blanche
- 16b Bord de dalles peint en teinte taupe foncé

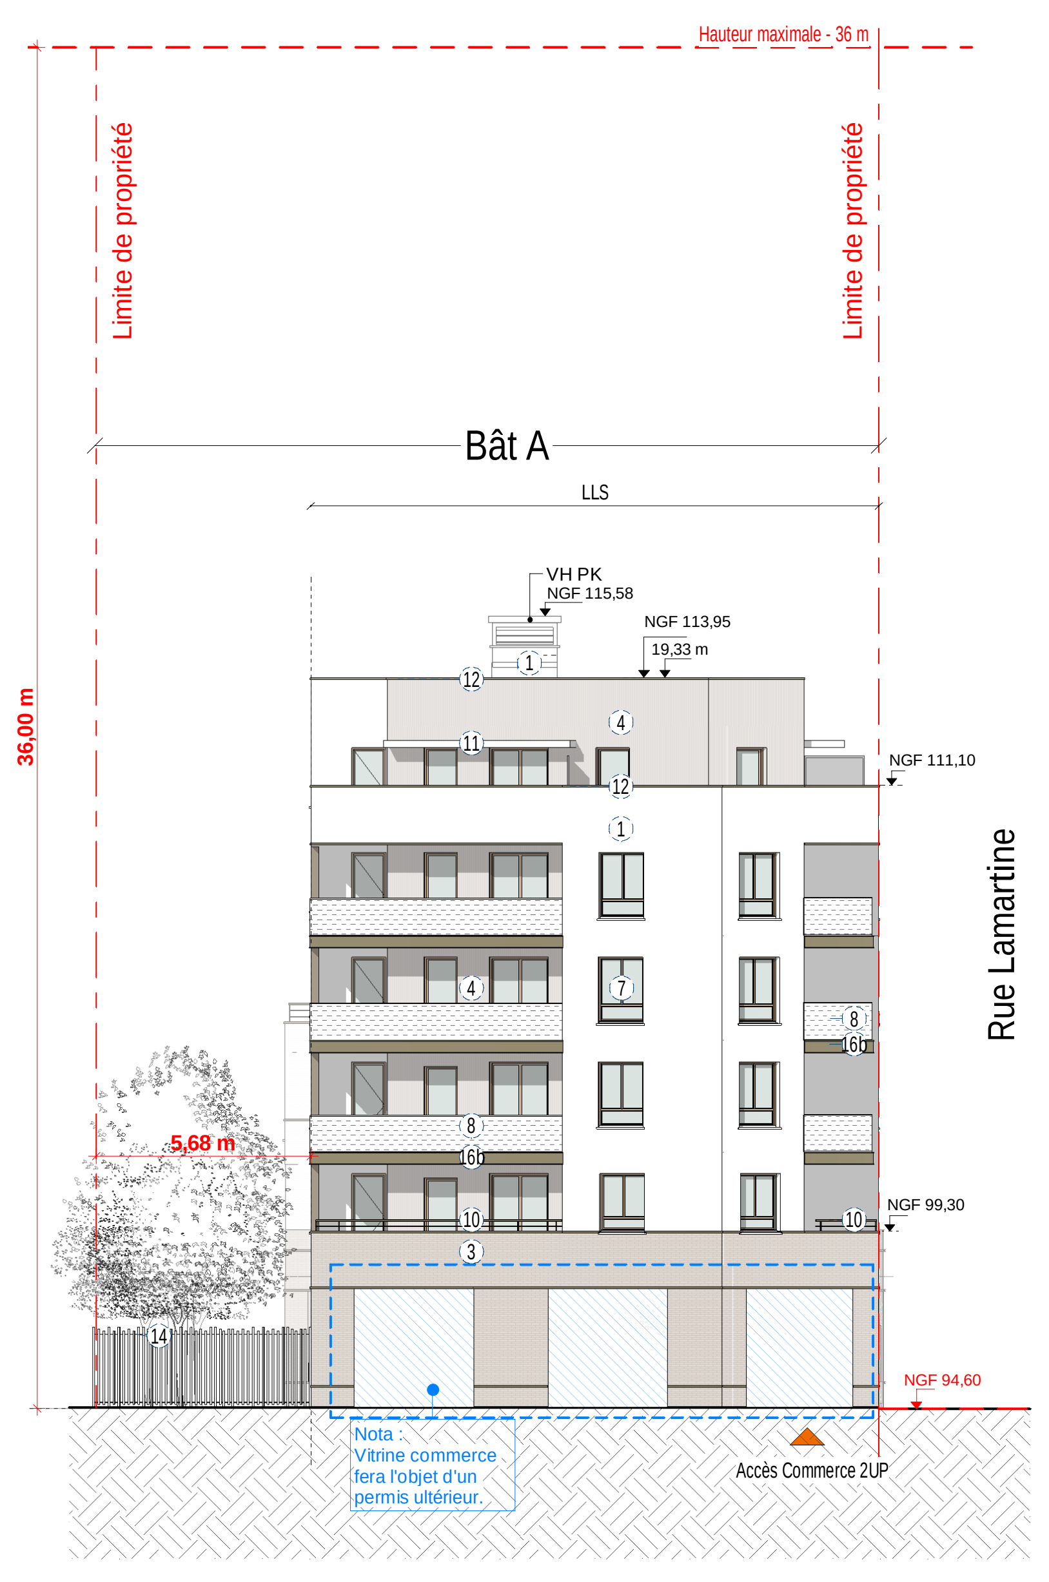

4. Façade Ouest Bât A
Echelle : 1 : 200ème

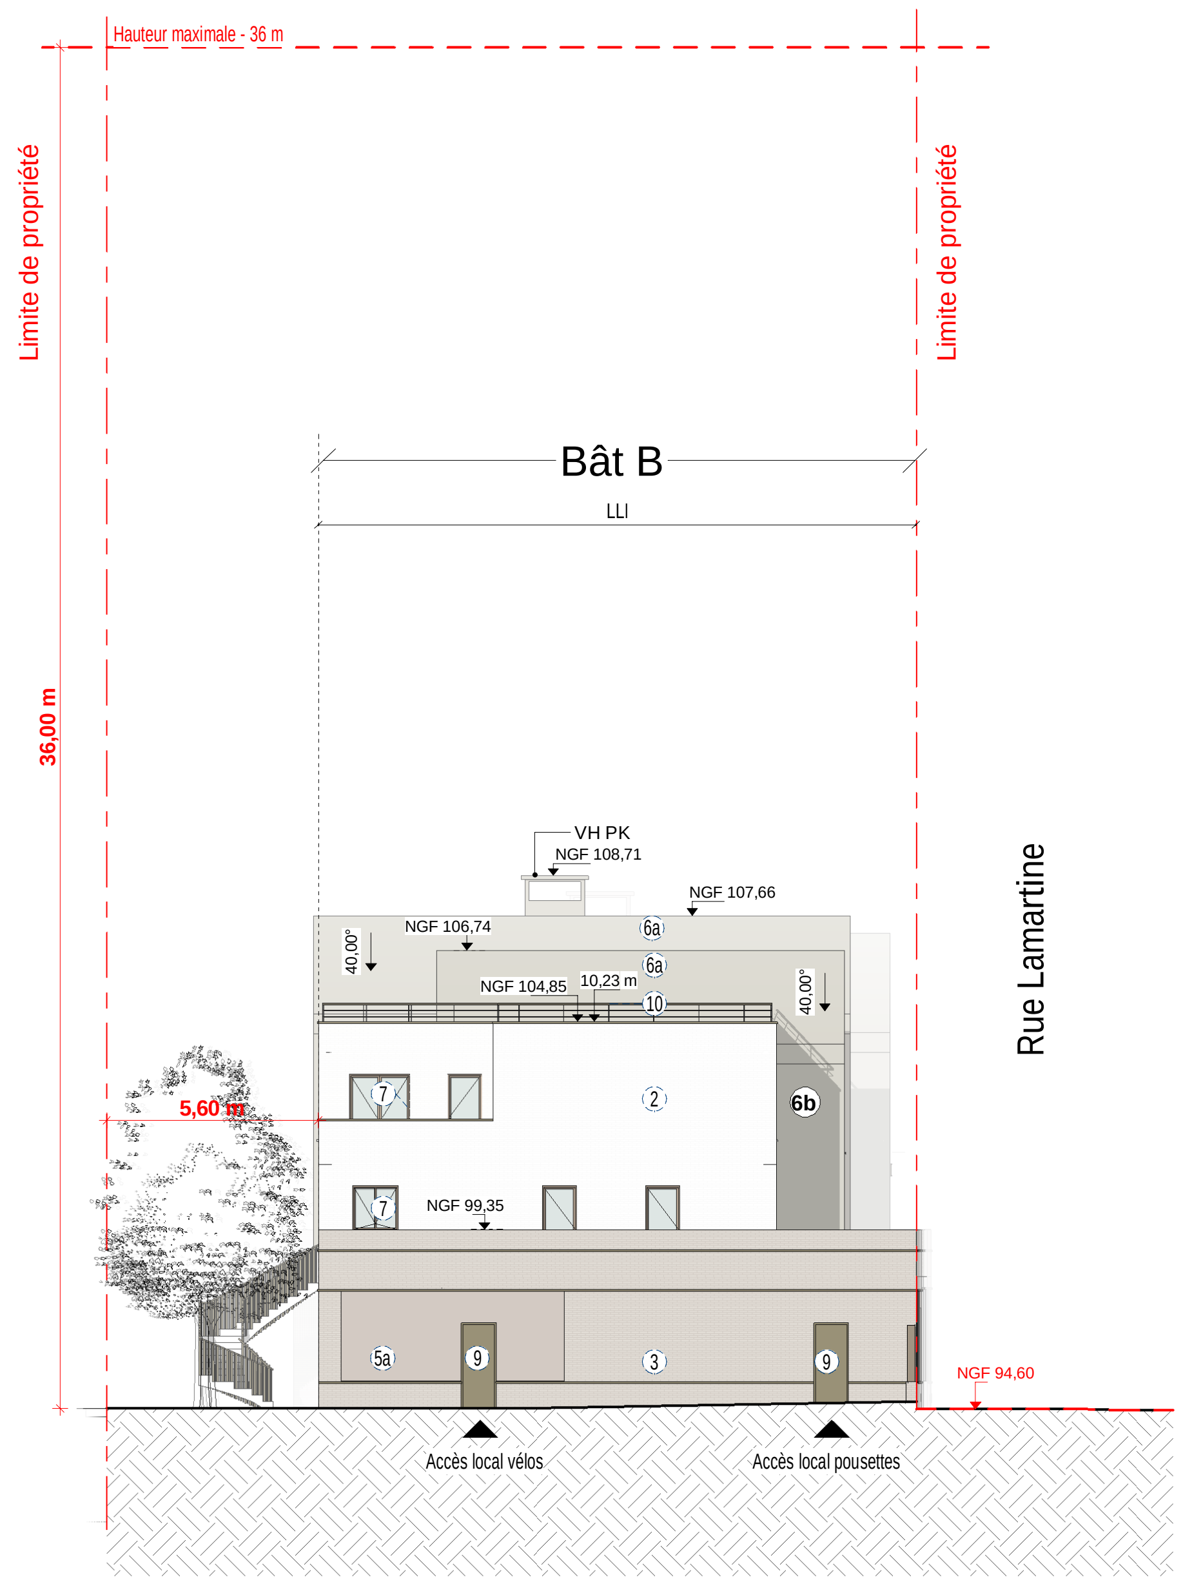

5. Façade Ouest Bât B
Echelle : 1 : 200ème

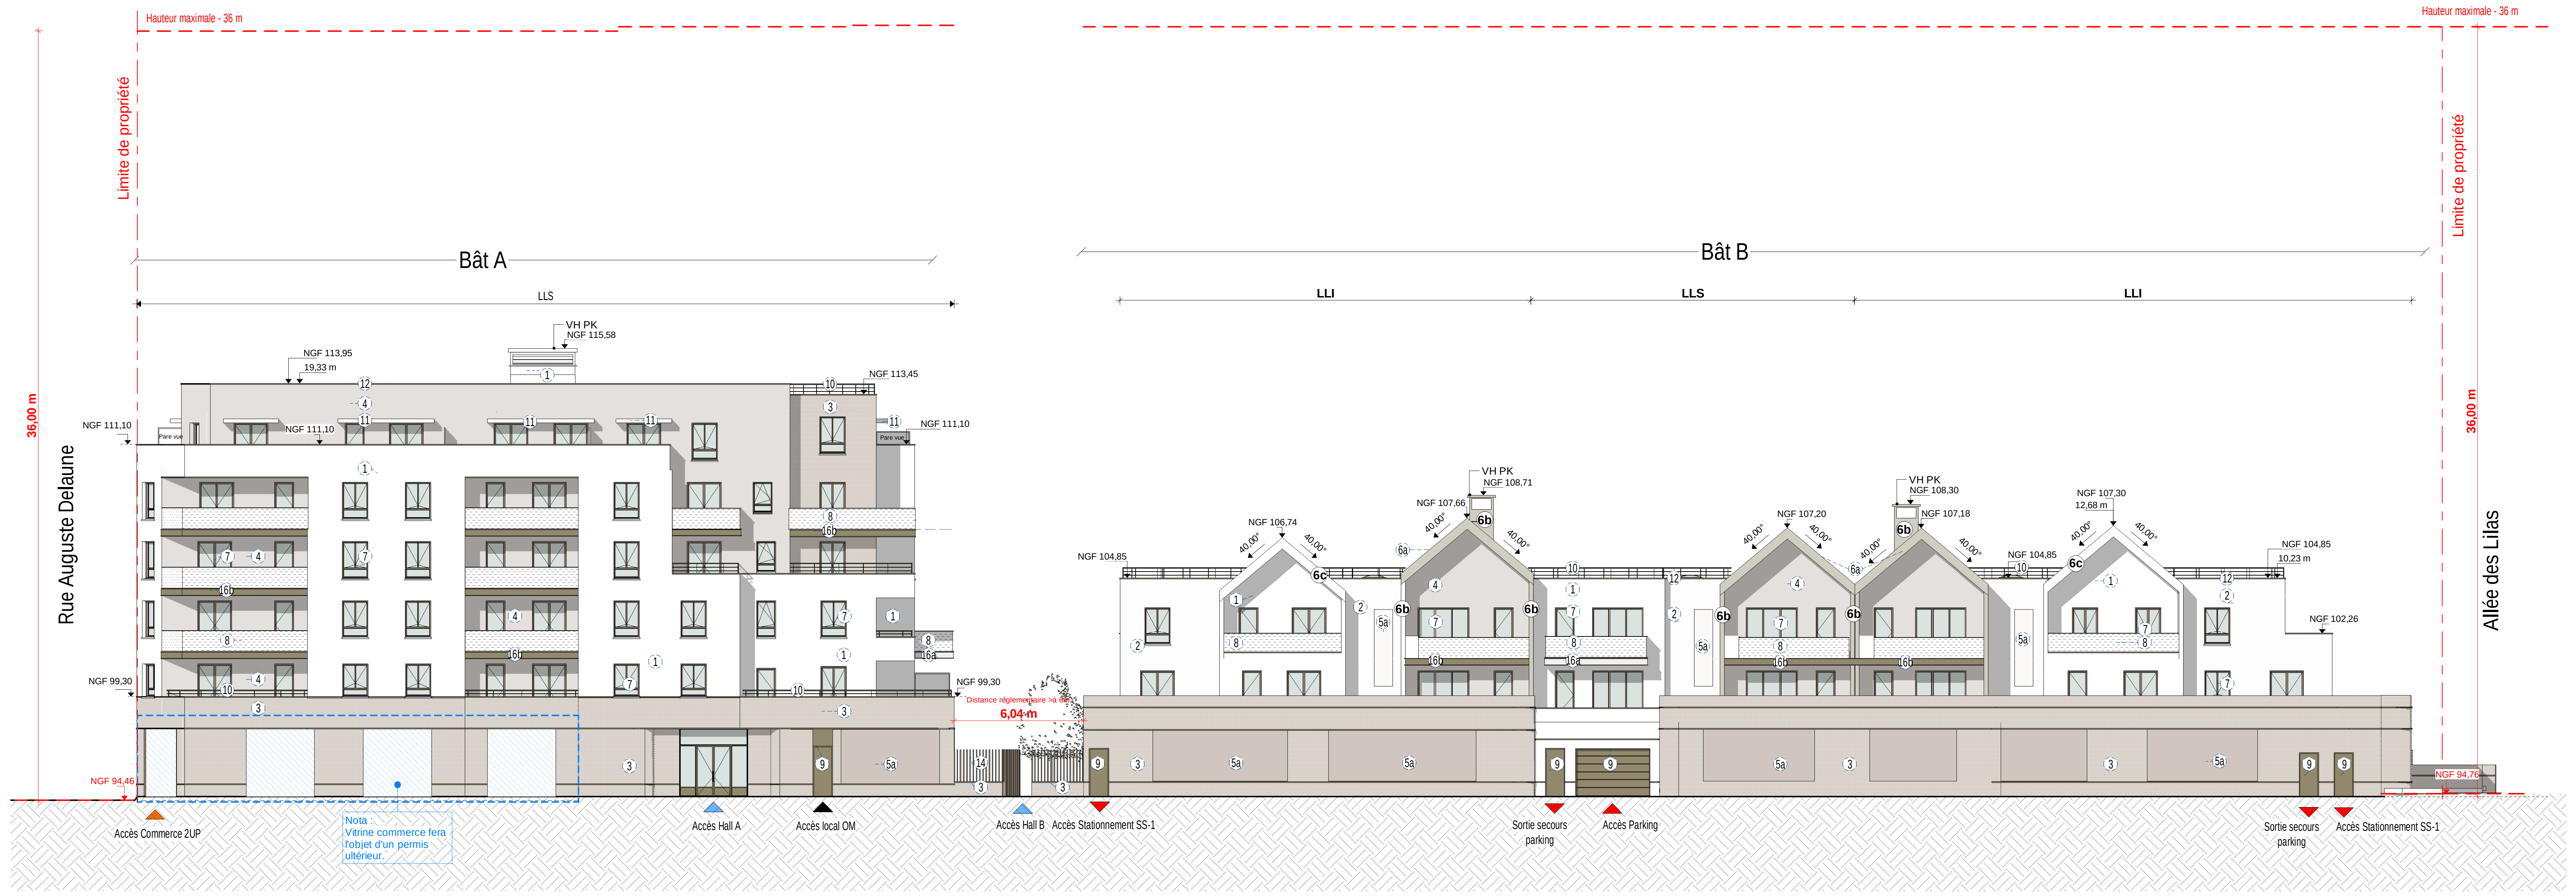

6. Façade SUD_Rue Lamartine
Echelle : 1 : 200ème

Les côtes NGF mentionnées sont données à titre indicatif et restent soumises à ultérieure synthèse avec le plan d'aménagement

0 4m 8m

Maîtrise d'Ouvrage

SCCV VILLEJUIF
LEBON LAMARTINE
FNE-FNO

121 Avenue de Malakoff 75116 Paris

Signed by:
François Daguet
B6701235FCC444D...

Rue LAMARTINE

PROJET A26 BLM

PROJET QUARTIER LEBON LAMARTINE

PC- FRANGE NORD OUEST- LEBON LAMARTINE

Pièce complémentaire

Titre			N°
Plan des façades - Art. R.431.10a			**PC5.1**
Date Mars 2026	Réf **3881**	Echelle 1/200	

Indice	Date	Modifications

- A26 BLM -
167 rue de Vaugirard-75015 PARIS
www.a26blm.eu - 01.45.67.09.02
SAS au capital de 33 100 €
NAF 7111Z-SIRET 410 007 249 00015
Ordre N°National S03534
TVA FR 67 410 007 249

Maîtrise d'Oeuvre

A26 BUILDING HARMONY

Architectes-Urbanistes
Agence certifiée ISO 9001 - ISO 14001

167, rue de VAUGIRARD - 75015 PARIS
Tél: 01.45.67.09.02 - email : contact-blm@a26.eu

LA COMPAGNIE DU PAYSAGE

Architectes-Paysagistes
11 rue Beauregard -75002 Paris
Tél: 01.53.26.77.32 - email : agence@compagniedupaysage.fr

apave

Infrastructures et Construction France
10 place Fulgence Bienvenue- 77600 Bussy Saint-Georges
Tél: 01.60.37.55.37 - email : marnevallee@apave.com

epdc

B.E.T
23 rue Raspail - 94200 Ivry-sur-Seine
Tél: 01.49.87.04.90 - email : contact@epdc.fr

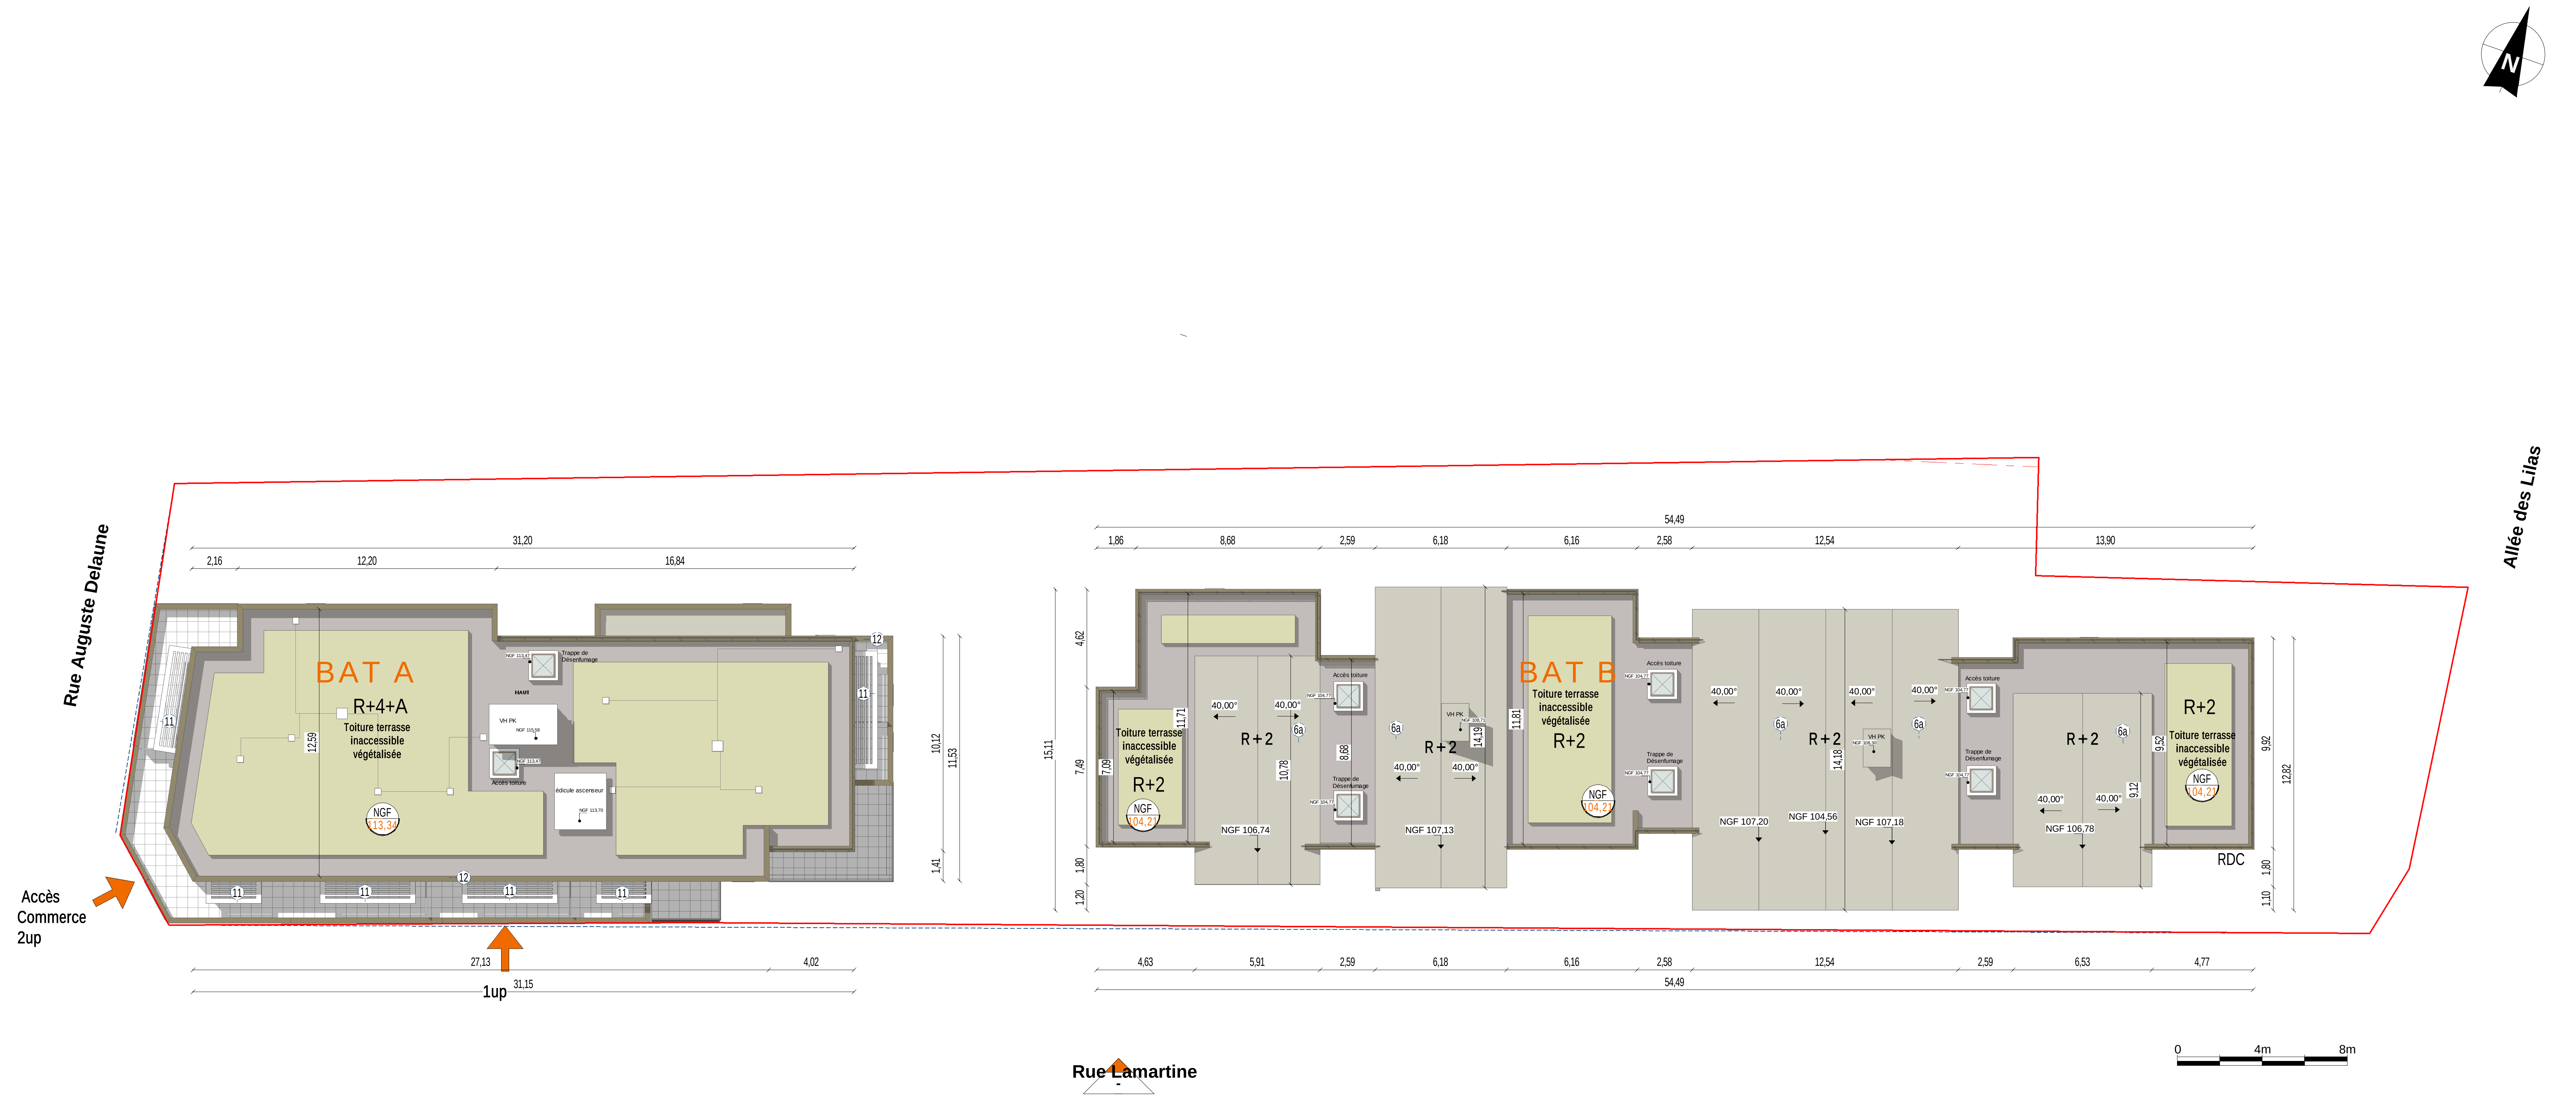

Maîtrise d'Ouvrage

SCCV VILLEJUIF
LEBON LAMARTINE
FNE-FNO

121 Avenue de Malakoff 75116 Paris

Signed by:
François Daguet
B6701235FCC444D...

Rue LAMARTINE

PROJET A26 BLM

PROJET QUARTIER LEBON LAMARTINE

PC- FRANGE NORD OUEST- LEBON LAMARTINE

Titre
Plan des toitures - Art. R.431.10a

N°
PC5.2

Date
Mars 2026

Réf
3881

Echelle
ECH : 1 : 200

Indice	Date	Modifications

- A26 BLM -
167 rue de Vaugirard-75015 PARIS
www.a26blm.eu - 01.45.67.09.02
SAS au capital de 33 100 €
NAF 7111Z-SIRET 410 007 249 00015
Ordre N°National S03534
TVA FR 67 410 007 249

Maîtrise d'Oeuvre

Architectes-Urbanistes
Agence certifiée ISO 9001 - ISO 14001

167, rue de VAUGIRARD - 75015 PARIS
Tél: 01.45.67.09.02 - email : contact-blm@a26.eu

Architectes-Paysagistes
11 rue Beauregard -75002 Paris
Tél: 01.53.26.77.32 - email : agence@compagniedupaysage.fr

Infrastructures et Construction France
10 place Fulgence Bienvenue- 77600 Bussy Saint-Georges
Tél: 01.60.37.55.37 - email : marnevallee@apave.com

B.E.T
23 rue Raspail - 94200 Ivry-sur-Seine
Tél: 01.49.87.04.90 - email : contact@epdc.fr

C:\Users\dcoco\Documents\0-REVIT-LOCALS\3881_VIL_EME_FNO_CENTRAL_dcocoAP3D2.rvt 05/03/2026 09:15:26

🟩 Clôture existante à conserver

🟪 Muret +serrurerie 1.80m de hauteur

🟦 Serrurerie 1.80m de hauteur

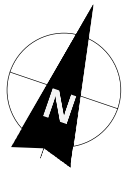

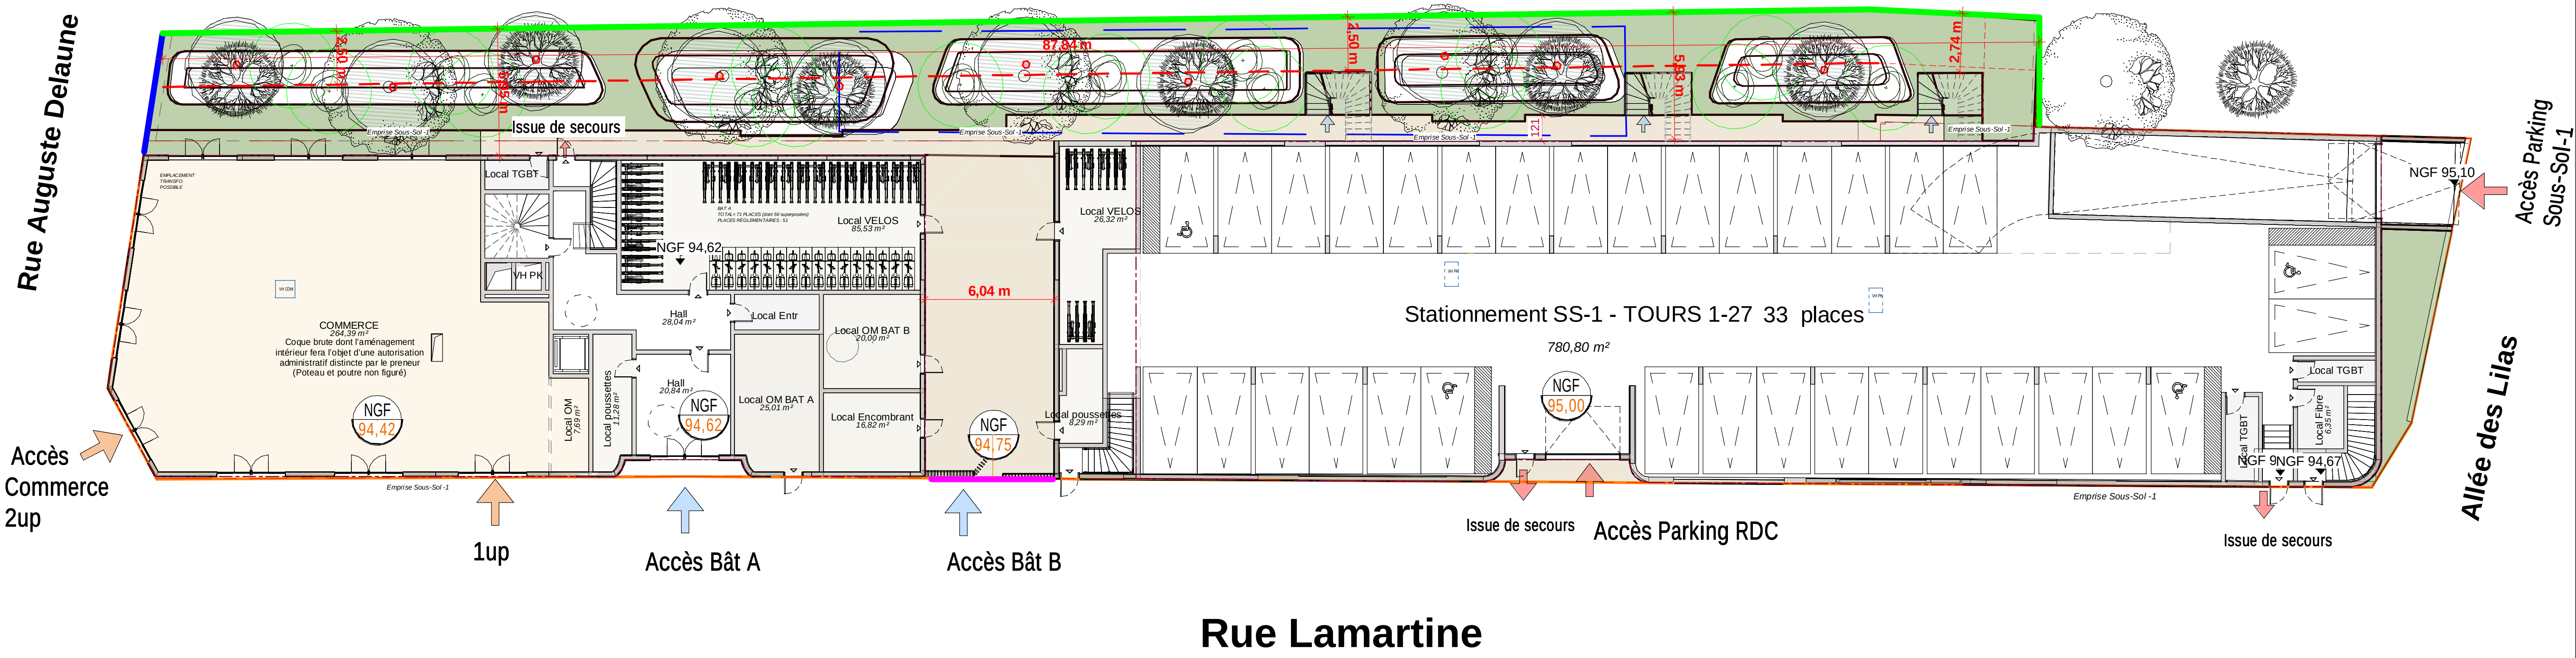

- A26 BLM -
167 rue de Vaugirard-75015 PARIS
www.a26blm.eu - 01.45.67.09.02
SAS au capital de 33 100 €
NAF 7111Z-SIRET 410 007 249 00015
Ordre N°National S03534
TVA FR 67 410 007 249

Maitre d'oeuvre : A26 BUILDING HARMONY	Maitre d'ouvrage :	PROJET A26 BLM	Plan de répérages des clôtures	PC5.3
		PC- FRANGE NORD OUEST- LEBON LAMARTINE	Date : Mars 2026 | Ech : 1 : 300 | 3881	